

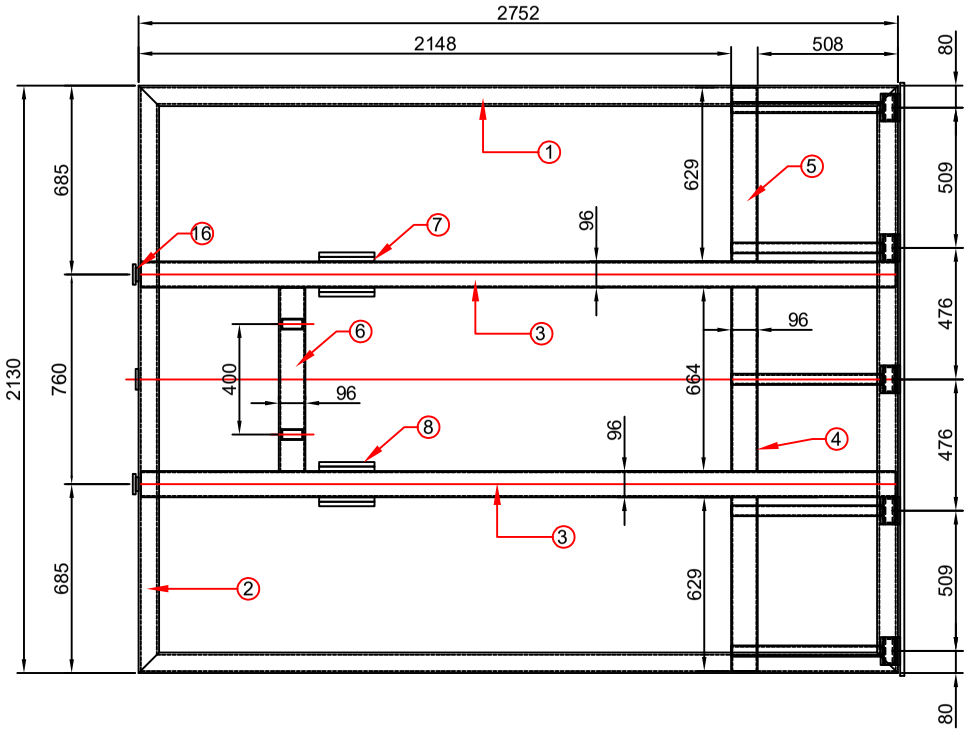


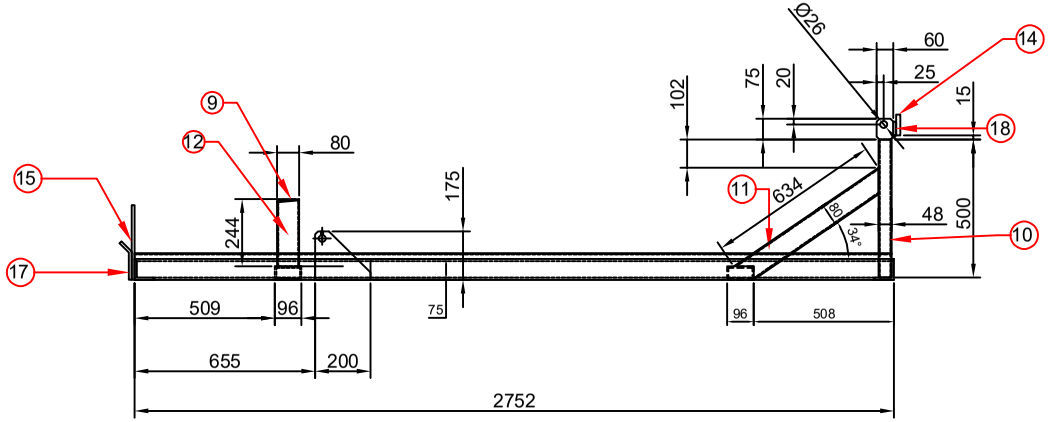

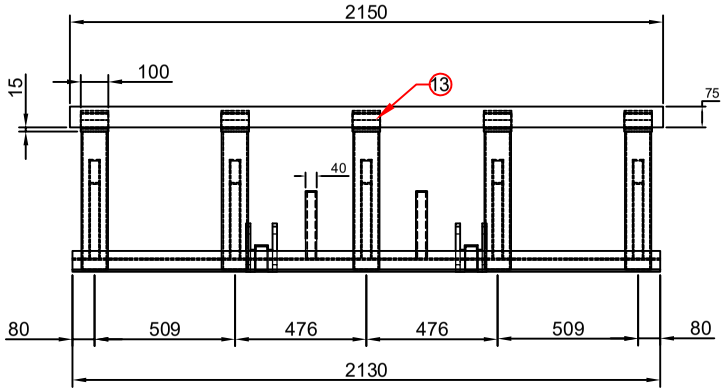

BOM			
SL NO.	DESCRIPTION	SPECIFICATION	QTY
1	ISA	75X75X8X2752	2NOS
2	ISA	75X75X8X2130	2NOS
3	RECT. TUBE	96X48X4.8X2736	2NOS
4	RECT. TUBE	96X48X4.8X664	2NOS
5	RECT. TUBE	96X48X4.8X629	1NO
6	RECT. TUBE	96X48X4.8X664	1NO
7	MS FLAT	75X16X200L	4NOS
8	CYLINEDER MTNG BKT	175X16X200L	4NOS
9	MS FLAT	50X5X100L	2NOS
10	RECT.TUBE	96X48X4.8X500	5NOS
11	RECT.TUBE	80X40X4X634	5NOS
12	RECT.TUBE	80X40X4.8X244	2NOS
13	MS BLOCK(DECK HLDNG BKT)	75X60X100	5NOS
14	MS FLAT	75X16X2150	1NO
15	MS FLAT	75X10X270	1NO
16	MS FLAT	50X10X75	2NOS
17	MS FLAT	75X10X155	2NOS
18	MS FLAT	50X10X100	5NOS

This drawing & design is the property of NIHVA TECHNOLOGIES. Not to be sold or copied to any other concern.

TITLE:- BASE FRAME

NIHVA TECHNOLOGIES PVT. LTD.

NIHVA TECHNOLOGIES PVT. LTD. PUNE
Tel : 020 66304033
Email:- info@nihva.com
Website:- www.nihva.com

	NAME	DATE	SIGN
DRAWN	SUJATA	30/12/2021	
CHECK	G.PATIL	31/12/2021	
APPRD.	A.K	31/12/2021	

CLIENT -
LOCATION -
PRODUCT -

If any queries contact : design@nihva.com

DWG NO:-NIHVA/21-22/MFG/007 REV- 0

ALL DIMENSION ARE IN mm

SCALE: NTS SCALE:-- 1:1 SHEET: 01 OF 01

Rev No.	Revision	Date	Revised By