Quote acceptance

To allow us to proceed with this work, please complete the details below and return to
E-mail:ashish.achuthan@assaabloy.com

Company name: NIHVA Technologies Pvt Ltd.

VAT number: GST NO- 27AAECN0437H1ZM

Contract value: US Dollar $ 24,36,660

Invoice address and e-mail: 8/1 Coromant Housing Society Sec No 27 Nigdi Pradhikaran Pune - 411044 India.

Site address: Seabird Karwar India.

Order number: NVA 533

Name: Mr. Vijay Tarak.

Phone: 8551093333.


E-mail: sales@nihva.com

Date: 27/08/2021

Signed by authorized Purchaser:

Printed name:

NIHVA TECHNOLOGIES PVT. LTD. CHINCHWAD PUNE

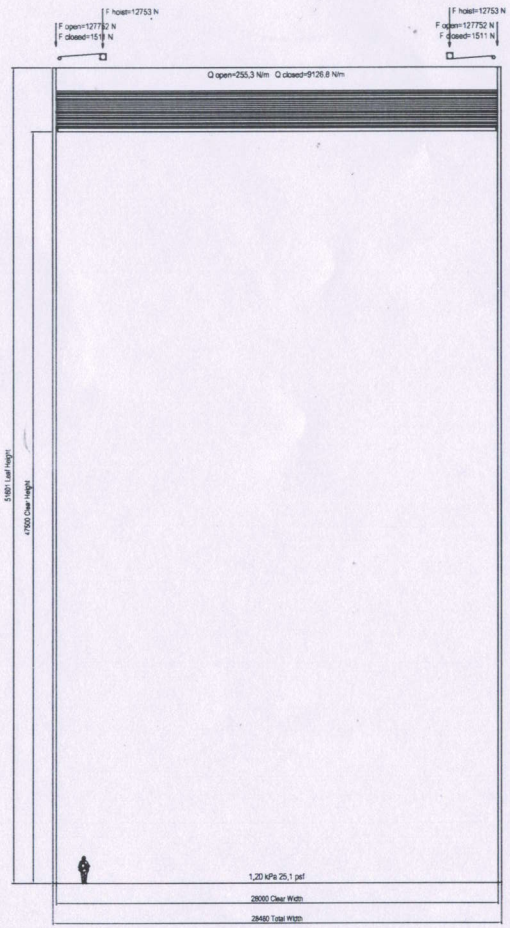

Quotation only. Do not use for design.
Nominal static vertical loads are indicated.
A dynamic surface factor of 1,25 should be added to door leaf loads in open position.
Includes items provided by ASSA ABLOY Entrance Systems only.
Total weight: 32217 kg
Total static weight: 29744 kg
Total motor power: 42,0 kW
Total rated current: 78,2 A
Total peak current: 484,8 A
Power supply: 400V/50Hz/3ph
(max. allowed voltage drop at start: 5%)
Control system: 24V
Mains power to control panel supplied by others than ASSA ABLOY Entrance Systems.

Contact Information
Mats Brännström
Senior Design Engineer, Mechanical
MEGADOOR/
ASSA ABLOY Entrance Systems
Servicegatan 6
P.O. Box 383
SE-931 24 Skellefteå
SWEDEN
Phone: +46 (0)10 47 47 190
Direct: +46 (0)10 47 47 754
E-mail: mats.brannstrom@assaabloy.com
www.megadoor.com

NIHVA TECHNOLOGIES PVT. LTD. CHINCHWAD PUNE


ASSA ABLOY

SALES REP. Mats Brännström	DATE ISSUED 2019-08-21
SALES No. 215-165	DATE DRAWN 2019-08-21
SCALE N.T.S.	
DRAWING No. 215-165	REVISION F

AECOM, Indian Navy

India (EN 12604)

Load diagram

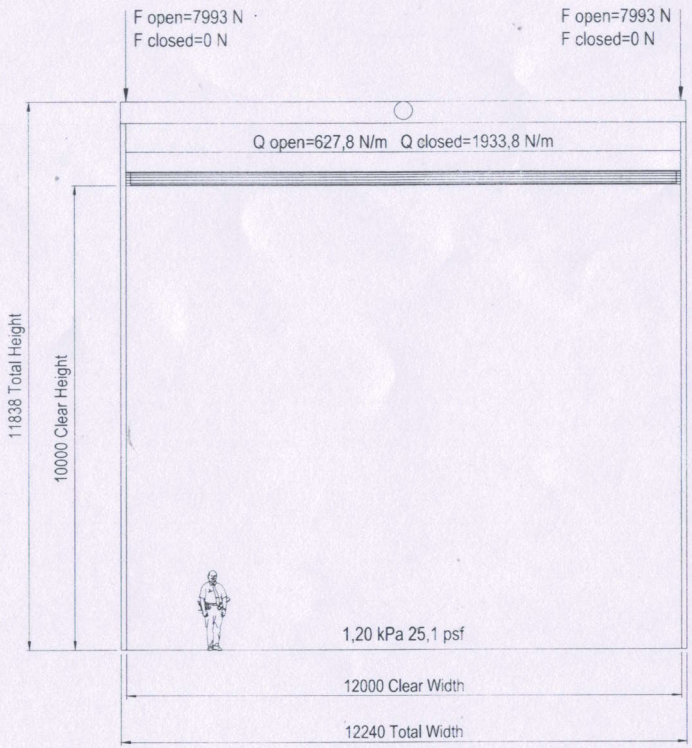

Quotation only. Do not use for design.
Nominal static vertical loads are indicated.
A dynamic surload factor of 1.25 should be added to door leaf loads in open position.
Includes items provided by ASSA ABLOY Entrance Systems only.
Total weight: 2641 kg
Total static weight: 2421 kg
Total motor power: 5,0 kW
Total rated current: 10,2 A
Total peak current: 45,0 A
Power supply: 400V/50Hz/3ph
(max. allowed voltage drop at start: 5%)
Control system: 24V
Mains power to control panel supplied by others than ASSA ABLOY Entrance Systems.

Contact Information
Henk v.d. Heijden
Project Manager
MEGADOOR/
ASSA ABLOY Entrance Systems
Servicegatan 6
P.O. Box 383
SE-931 24 Skellefteå
SWEDEN
Direct: +31 (0)65 323 61 77
Switchboard: +46 (0)10 47 47 190
E-mail: henk.van.der.heijden@assaabloy.com
www.megadoor.com

NIHVA TECHNOLOGIES PVT. LTD. CHINCHWAD PUNE

ASSA ABLOY

SALES REP. Ashish Nair	DATE ISSUED 2-8-2019
SALES No. 215-165	DATE DRAWN 2-8-2019
SCALE N.T.S.	
DRAWING No. 215-165	REVISION C

Aecom Navy
India

Load diagram