




1

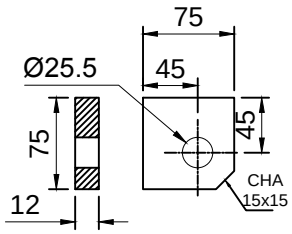


5

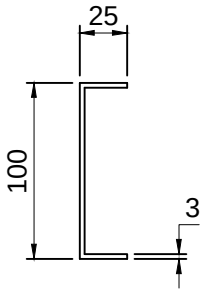


9

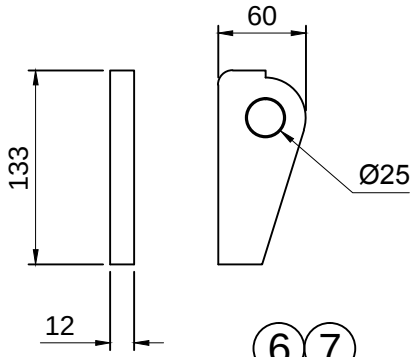

6 7

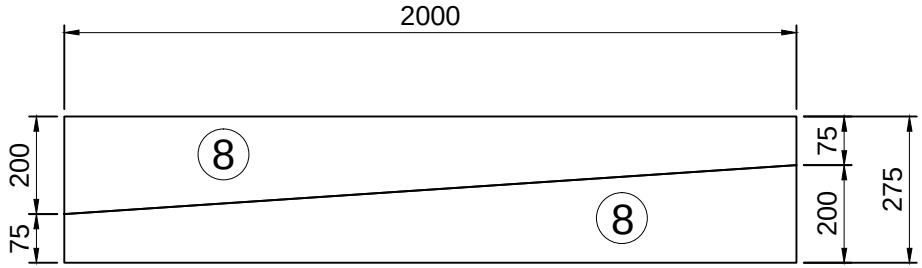

14

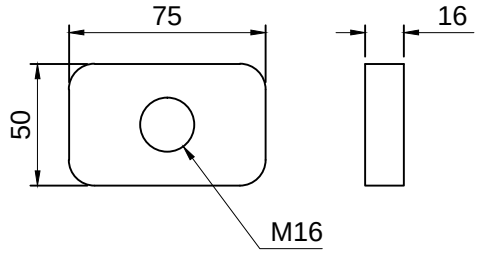

This drawing & design is the property of NIHVA TECHNOLOGIES. Not to be sold or copied to any other concern.

TITLE: DECK DETAILS				NIHVA TECHNOLOGIES PVT. LTD. PUNE Tel : 020 66304033 Email:- info@nihva.com Website:- www.nihva.com	
	NAME	SIGN	DATE		
DRAWN	P.A		20.02.2020	CLIENT -	
CHECK	G.J		20.02.2020	PROJECT -	
APPRD.				SITE LOCATION -	
If any queries contact : design@nihva.com				DWG. NO. : NIHVA/19-20/VDR/314	
ALL DIMENSION ARE IN mm				SCALE: NTS	WT: REV- 00