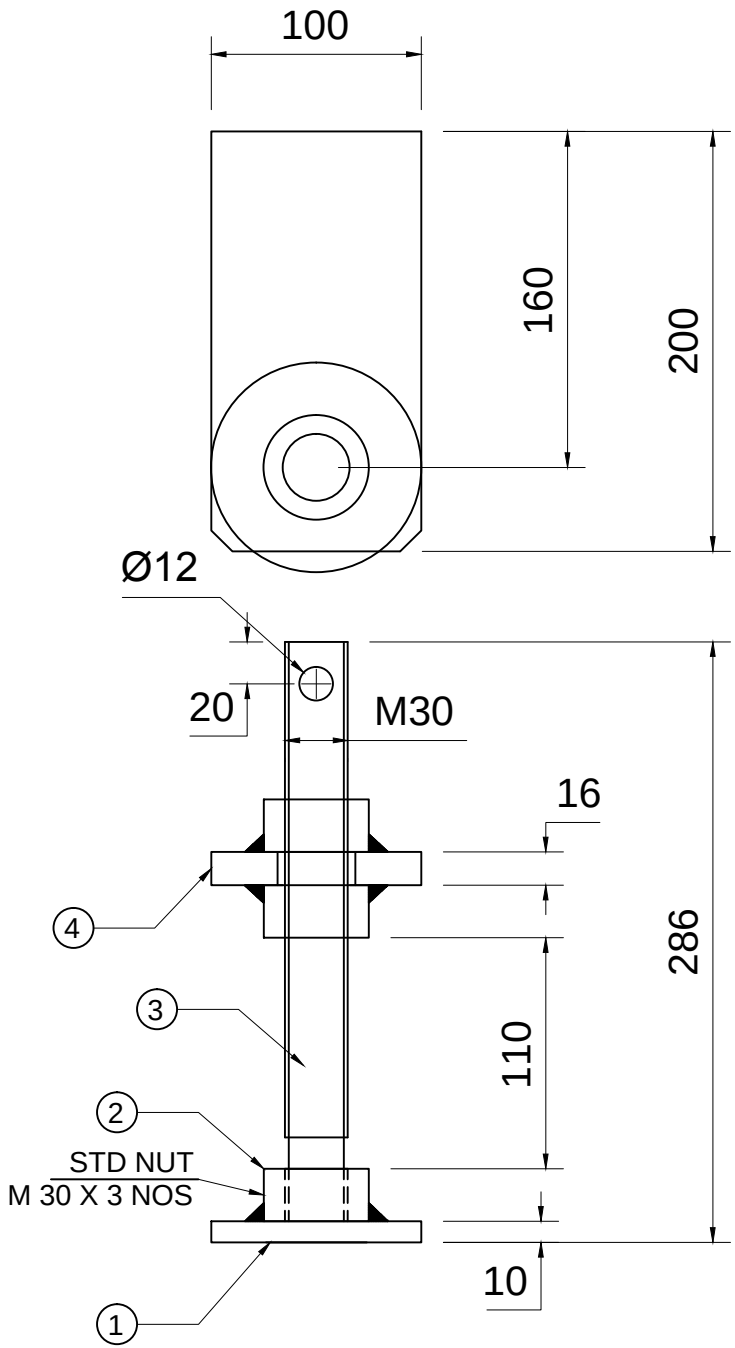


FLOOR LOCK ASSLY = 04 NOS

1. ROUND Ø100 X 10THK = 1 NOS
2. STD NUT M 30 = 3 NOS
3. STUD M 30 X 280L = 1 NO
4. FLAT 100 X 16 X 200 = 1 NO
5. MS BAR Ø12 X 200L = 4 NOS

This drawing & design is the property of NIHVA TECHNOLOGIES. Not to be sold or copied to any other concern.

TITLE : - FLOOR LOCK ASSLY			NIHVA TECHNOLOGIES PVT. LTD.
	SIGN	DATE	
DRAWN	P.A	04.10.2018	CLIENT -
CHECK	R.D	04.10.2018	PROJECT -
REV.			SITE -
APPROVAL			DWG. NO. : NIHVA/18-19/MFG/NSL/1018/016
If any queries contact : projects@nihva.com			SCALE: NTS / WT: / SHEET: 01 OF 01
ALL DIMENSION ARE IN mm			

NIHVA TECHNOLOGIES PVT. LTD. PUNE
Tel : 020 66304033
Email:- info@nihva.com
Website:- www.nihva.com