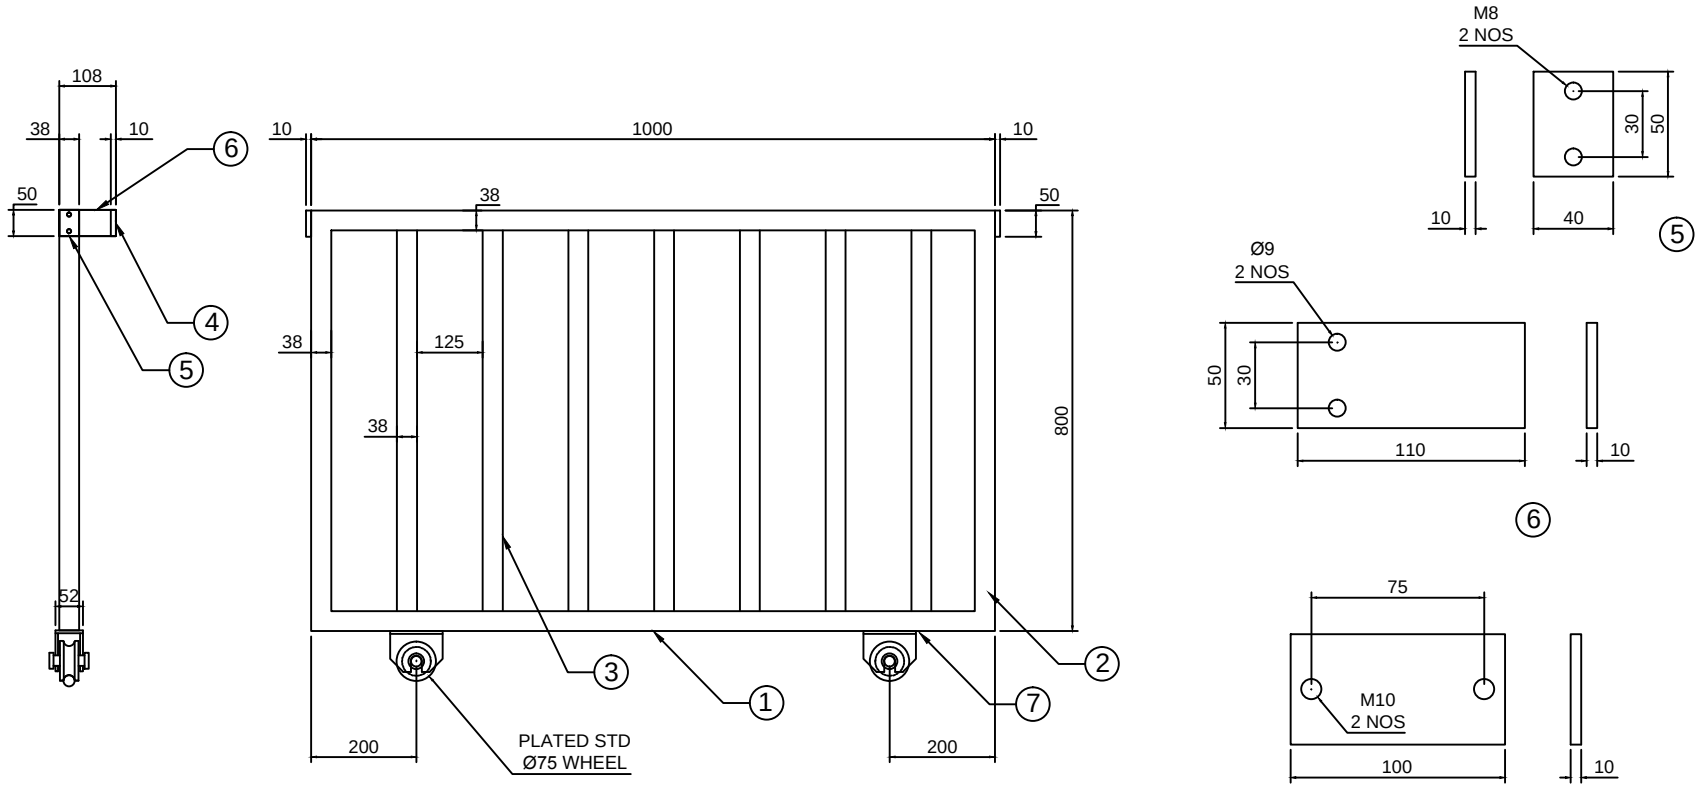


SR NO	DESCRIPTION	SPECIFICATION	QTY
7	MS FLAT	50 X 10 X 100L	2 NOS
6	MS FLAT	50 X 10 X 110L	2 NOS
5	MS FLAT	40 X 10 X 50L	2 NOS
4	MS FLAT	50 X 10 X 1000L	1 NO
3	SQ. TUBE	38 X 38 X 4 THK X 724L	5 NOS
2	SQ. TUBE	38 X 38 X 4 THK X 800L	2 NOS
1	SQ. TUBE	38 X 38 X 4 THK X 1000L	2 NOS

QTY : 2 NOS

This drawing & designing is the property of NIHVA TECHNOLOGIES. Not to be sold or copied to any other concern.

TITLE
1ST & 2ND LEAF

NIHVA TECHNOLOGIES
PVT. LTD. PUNE
Tel : 020 66304033
Email:- info@nihva.com
Website:- www.nihva.com

	NAME	SIGN	DATE
DRAWN	P.A		10.12.19
CHECKED	G.J		10.12.19
APPROVED			

CLIENT -
PROJECT -
SITE LOCATION -
DWG. NO. : NIHVA/19-20/VDR/239 REV: R00
If any queries contact : projects@nihva.com
SCALE: NTS WT: SHEET: 01 OF 01
ALL DIMENSION ARE IN mm