

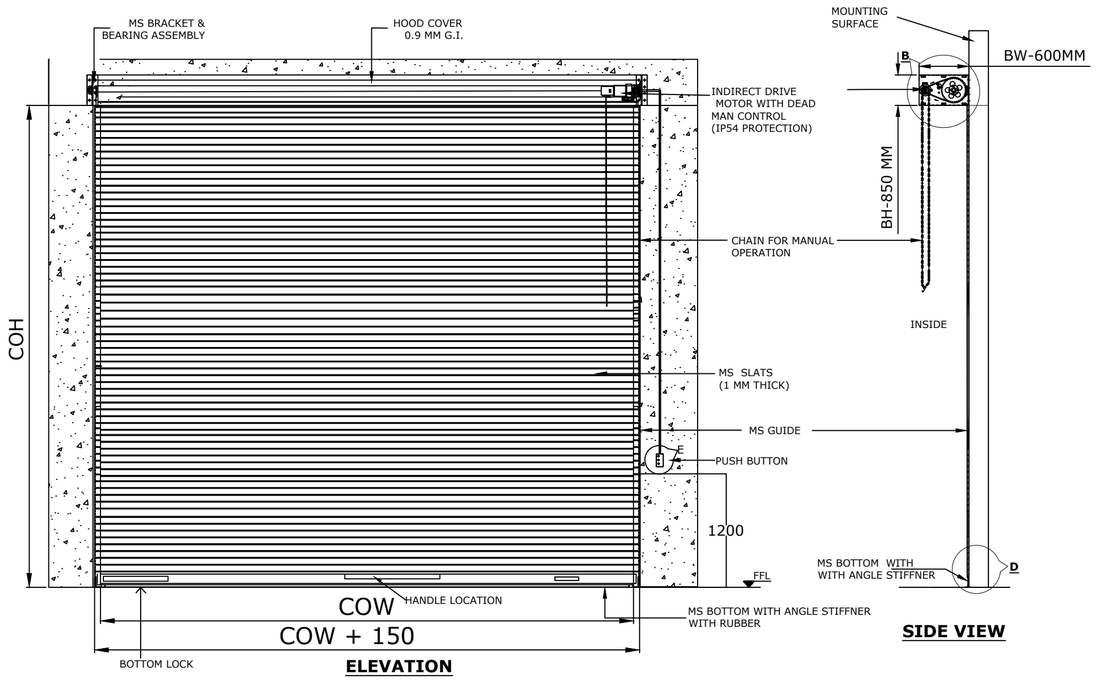


ELEVATION


SIDE VIEW

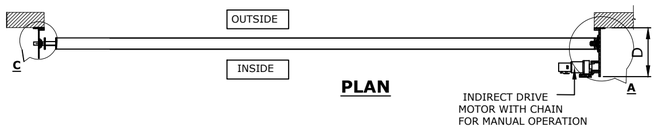

PLAN

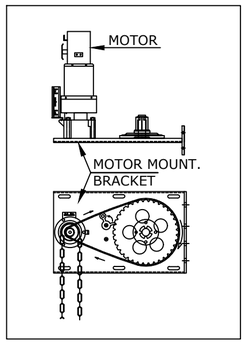


DETAILS : A & B

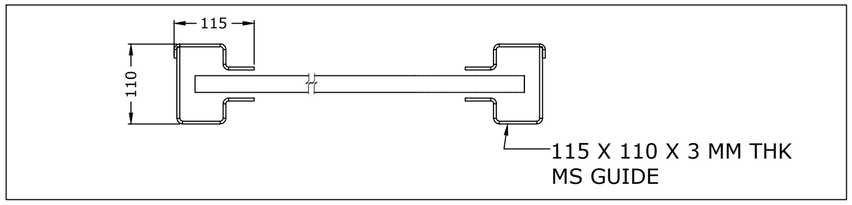


NOTES-

1. REFER RAL SHADE CHART & CONFIRM RAL SHADE FOR PAINTING .(IF ANY OTHER , KINDLY INFORM TO NIHVA).
   PRIMER: EPOXY POLYAMIDE BASED ZINC PHOSPHATE PRIMER.
2. MOUNTING OF ROLLING SHUTTER GUIDES WILL BE ON MS STRUCTURE, PLEASE CONFIRM THE SAME.
3. IF REQUIRED ALL CIVIL WORK , STRUCTURE & ITS FITTING IS IN CLIENT SCOPE .
4. SPACE OF 550 MM IS REQUIRED ABOVE CLEAR OPENING HEIGHT FOR INSTALLATION OF SHUTTER.
5. CLEAR OPENING HEIGHT AFTER SHUTTER INSTALLATION WILL BE 150 MM LESS THAN WALL OPENING HEIGHT .
6. MANUAL CHAIN IS ONLY USED FOR EMERGENCY OPERATION.

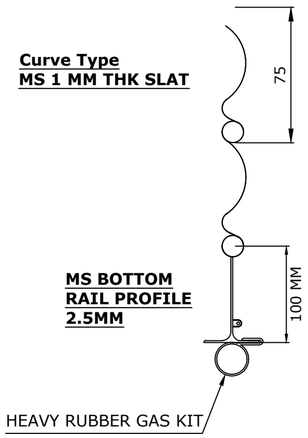

DETAILS : D

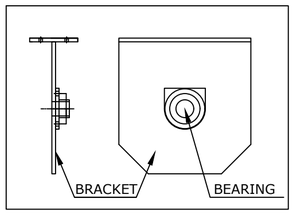

DETAILS : C

SR NO	CLEAR OPENING WIDTH (COW)	CLEAR OPENING HEIGHT (COH)		RAL COLOR FOR PAINTING
1	4500	6000	6 NOS	SCPECIFIED BY CLIENT
2	4000	5000	1 NOS	SCPECIFIED BY CLIENT
3	4000	3800	2 NOS	SCPECIFIED BY CLIENT
4	3000	3800	1 NOS	SCPECIFIED BY CLIENT

RAL CODE	SHADE	COLOUR
RAL 9001	CREAM	
RAL 9002	GREY WHITE	
RAL 9010	PURE WHITE	
RAL 5002	ULTRAMARINE BLUE	
RAL 7035	LIGHT GREY	
RAL 7001	SILVER GREY	

This drawing & design is the property of NIHVA TECHNOLOGIES. Not to be sold or copied to any other concern.

TITLE

MOTORIZED ROLLING SHUTTER

NIHVA TECHNOLOGIES PVT. LTD.
NIHVA TECHNOLOGIES PVT. PUNE
Tel : 020 66304033
Email:- info@nihva.com
Website:- www.nihva.com

	NAME	SIGN	DATE
DRAWN	G.I.P.		18.08.2021
CHECK	A.K.		18.08.2021
APPRD.	V.T.		18.08.2021

CLIENT -

PROJECT -

SITE LOCATION -

If any queries contact :design@nihva.com | DWG. NO. : NIHVA/21-22/VDR/0152 | REV- 00

ALL DIMENSION ARE IN mm | SCALE: NTS | WT: | SHEET: