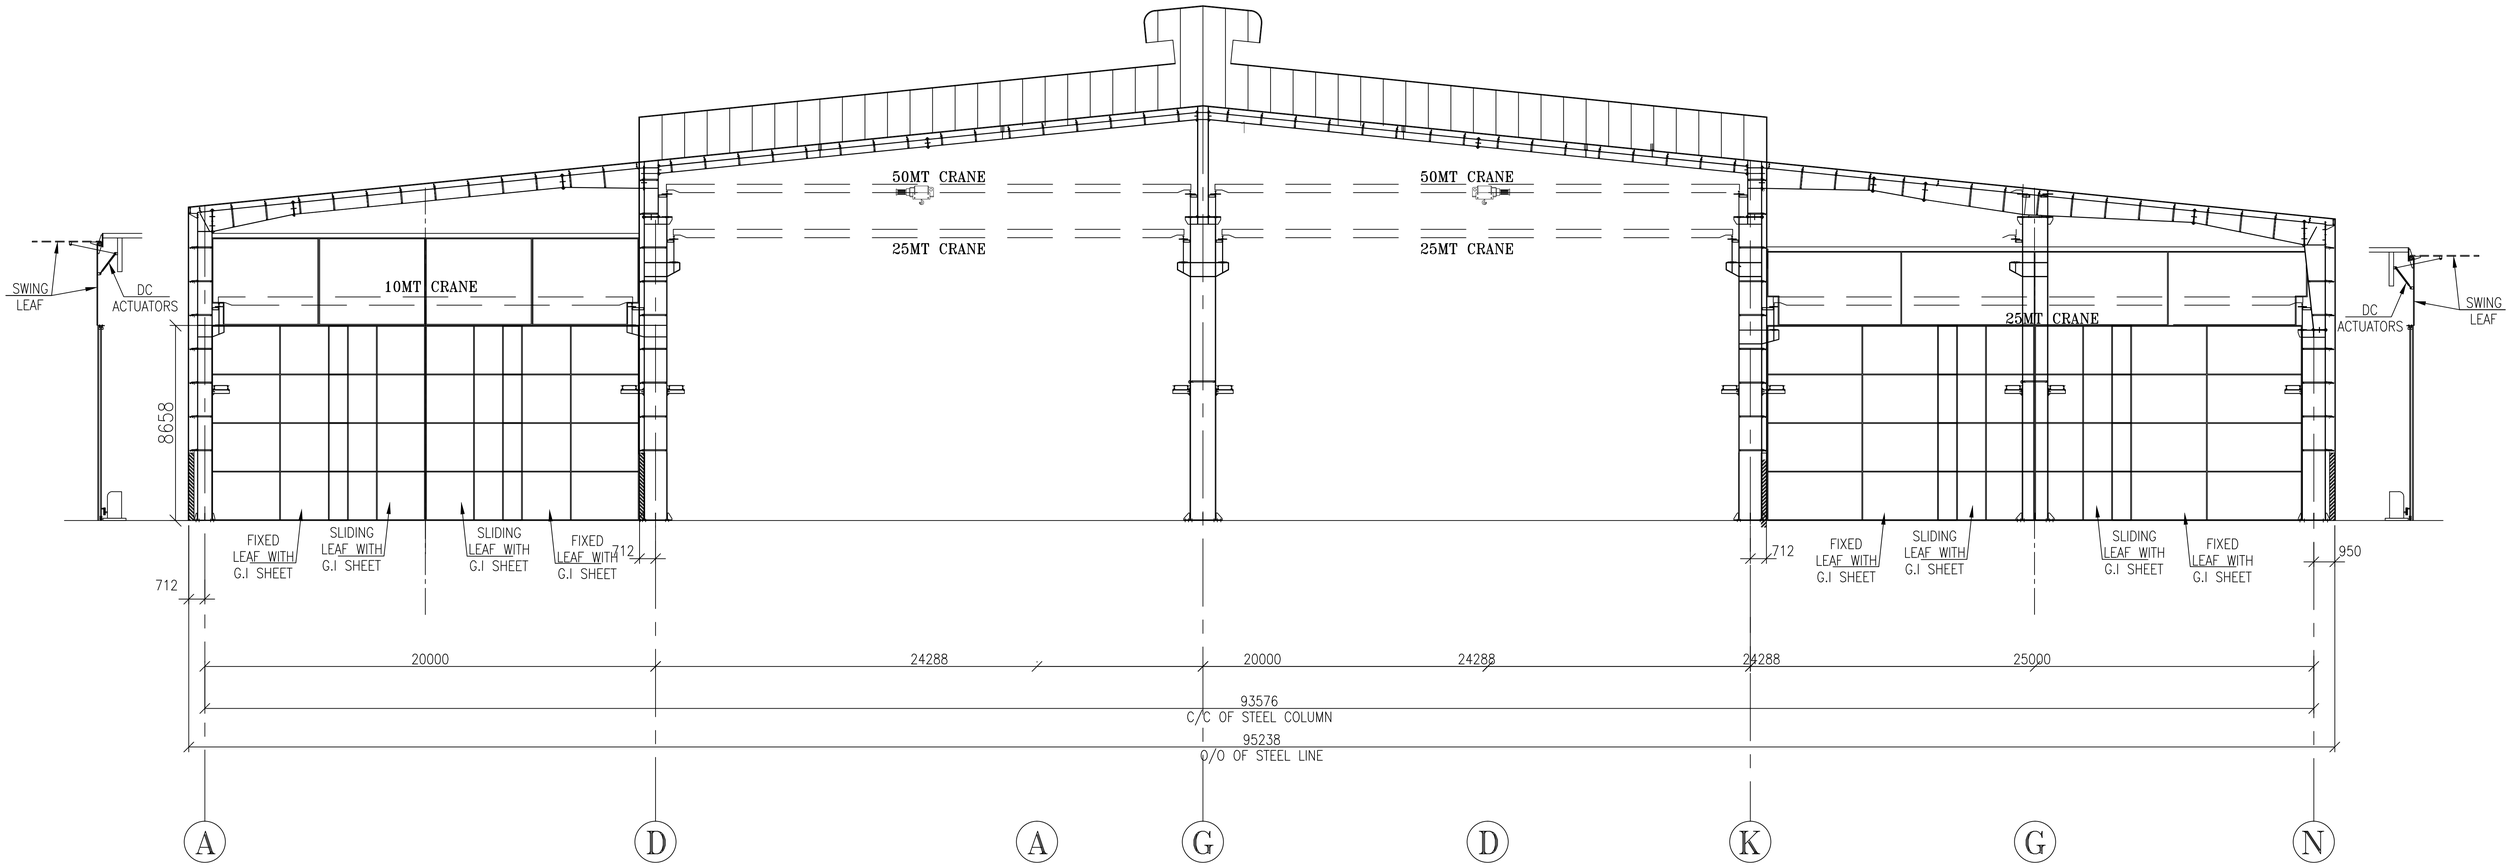


TOLERANCE :- ± 10mm

CONSULTANT NAME : SPECTRUM PHARMATECH CONSULTANT PVT LTD.

This drawing & design is the property of NIHVA TECHNOLOGIES. Not to be sold or copied to any other concern.

TITLE

CRANE DOOR

	NAME	SIGN	DATE
DRAWN	P.V.A		09.09.19
CHECK	V.M.T		09.09.19
APPRD.			

If any queries contact : design@nihva.com

ALL DIMENSION ARE IN mm

NIHVA
NIHVA TECHNOLOGIES PVT. LTD.
Website:- www.nihva.com

NIHVA TECHNOLOGIES PVT. LTD. PUNE
Tel : 020 66304033
Email:- info@nihva.com

CLIENT -

PROJECT -

SITE LOCATION -

DWG. NO. : NIHVA/19-20/ REV- 00

SCALE: NTS WT: SHEET: 01 OF 01