


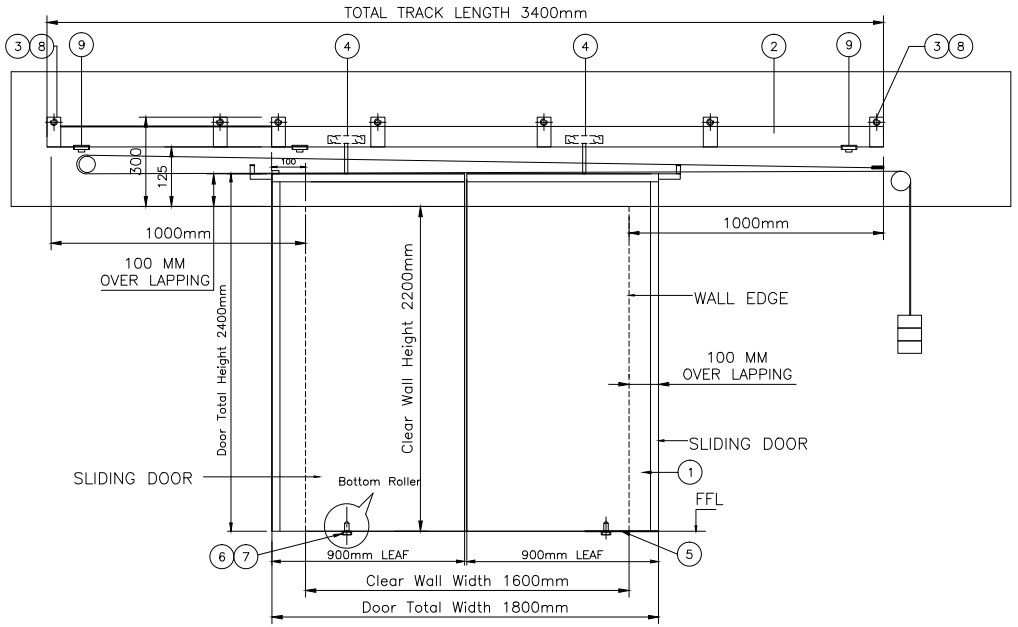


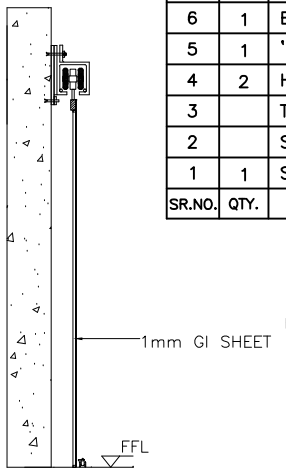

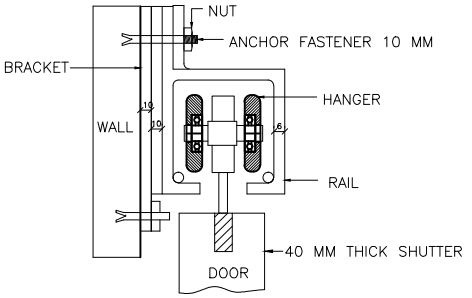

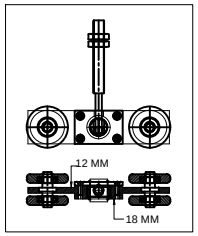


DETAIL AT 'B'

9	1	STOPPER (FOR HANGER ASSLY.)
8	1	COVER (FOR TRACK BKT.)
7	1	BOTTOM ROLLER MTG. FLAT (BOTTOM ROLLER BKT.)
6	1	BOTTOM ROLLER ASSLY.
5	1	'Z' SECTION
4	2	HANGER ROLLER ASSLY.
3		TRACK BRACKET
2		SLIDING TRACK
1	1	SLIDING DOOR & FRAME / BACK SUPPORT SQ. TUBE
SR.NO.	QTY.	DESCRIPTION



DETAIL–'A'

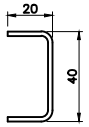

DETAIL–C PROFILE FOR FRAME

NOTE : DOOR OVERLAPING 100mm AT RH & LH AND TOP SIDE
ALL DIMENSIONS ARE IN MM.
CLIENT SHOULD CONFIRM DOOR OPENING DIRECTION.

TOLERANCE:- ± 10mm

DOOR DIMENSION		
CLEAR WIDTH	CLEAR HEIGHT	
1600mm	2200mm	01NOS

Panel Make : - Radient Safe Door Make

REV	DESCRIPTION	DRAWN	DATE
R01	PANEL DETAIL ADDED	A.K.	28.11.2018

This drawing & designing is the property of NIHVA TECHNOLOGIES. Not to be sold or copied to any other concern.

TITLE				
AUTOMATIC SLIDING DOOR				NIHVA TECHNOLOGIES PVT. LTD.
	NAME	SIGN	DATE	Website:- www.nihva.com
DRAWN	SURAJ		21/11/18	CLIENT - RATNARUP PROJECT PVT. LTD.
CHECK	P.A		20/11/18	PROJECT -RATNARUP PROJECT PVT. LTD.
APPROVAL	R.D		20/11/18	SITE - BANNER,PUNE.

NIHVA TECHNOLOGIES PVT. LTD. PUNE
Tel : 020 66304033
Email:- info@nihva.com

If any queries contact : design@nihva.com	DWG. NO. : NIHVA/18-19/0181/R01		REV-01
ALL DIMENSION ARE IN mm	SCALE: NTS	WT:	SHEET: 01 OF 01