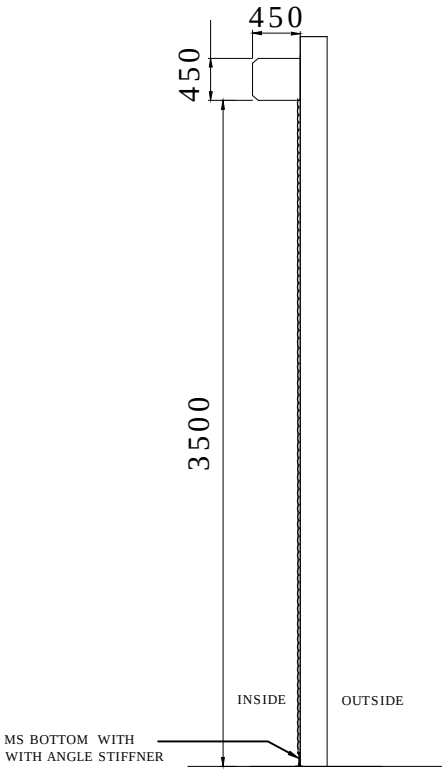

SIDE VIEW

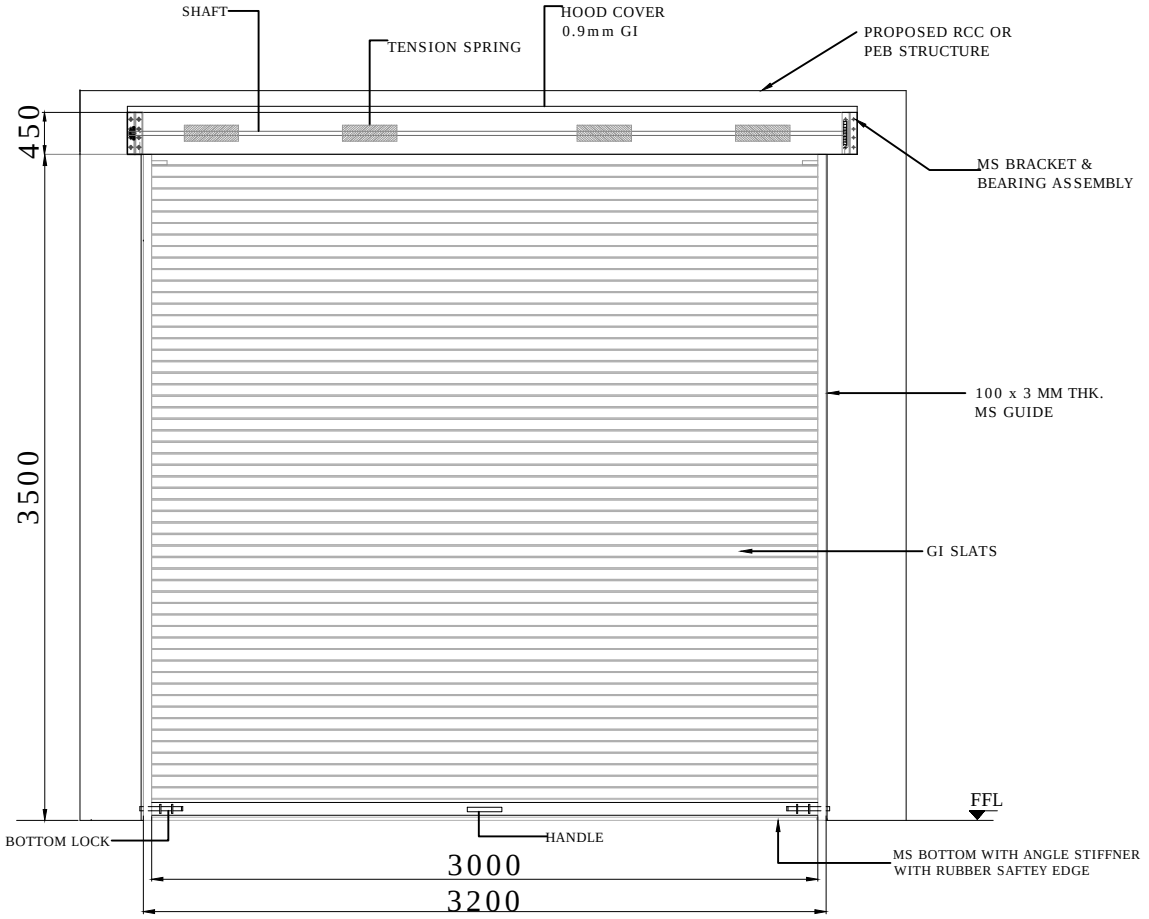

INSIDE ELEVATION

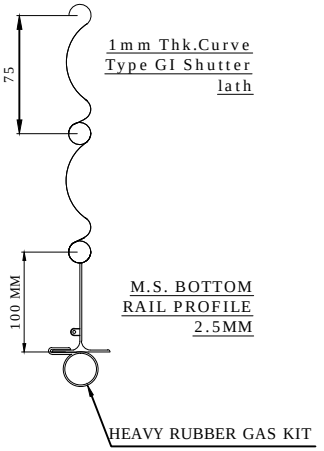

M.S. BOTTOM RAIL PROFILE 2.5MM

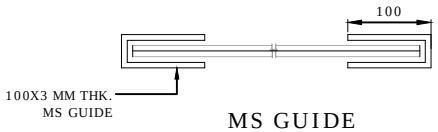

MS GUIDE

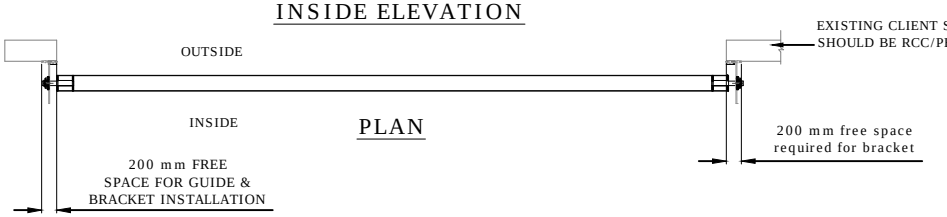

PLAN

NOTE:-
1. PAINTING WILL BE IN CLIENT'S SCOPE.
2. REQUIRED STRUCTURE WILL BE IN CLIENT SCOPE.

CLEAR WIDTH (CW)	CLEAR HEIGHT (CH)	QUANTITY
3000	3500	7

This drawing & designing is the property of NIHVA TECHNOLOGIES. Not to be sold or copied to any other concern.

TITLE
MANUAL ROLLING SHUTTER

NIHVA TECHNOLOGIES PVT. LTD. PUNE
Tel : 020 66304033
Email:- info@nihva.com
Website:- www.nihva.com

	SIGN	DATE
DRAWN	OMKAR	22/11/17
CHECK	SHEKHAR	22/11/17
APPROVAL	SHEKHAR	22/11/17
MFG.		

If any queries contact : design@nihva.com

ALL DIMENSION ARE IN mm

CLIENT -
PROJECT -
SITE -
DWG. NO. : NIHVA/17-18/VDR/0185 | REV-0
SCALE: NTS | WT: | SHEET: 01 OF 01