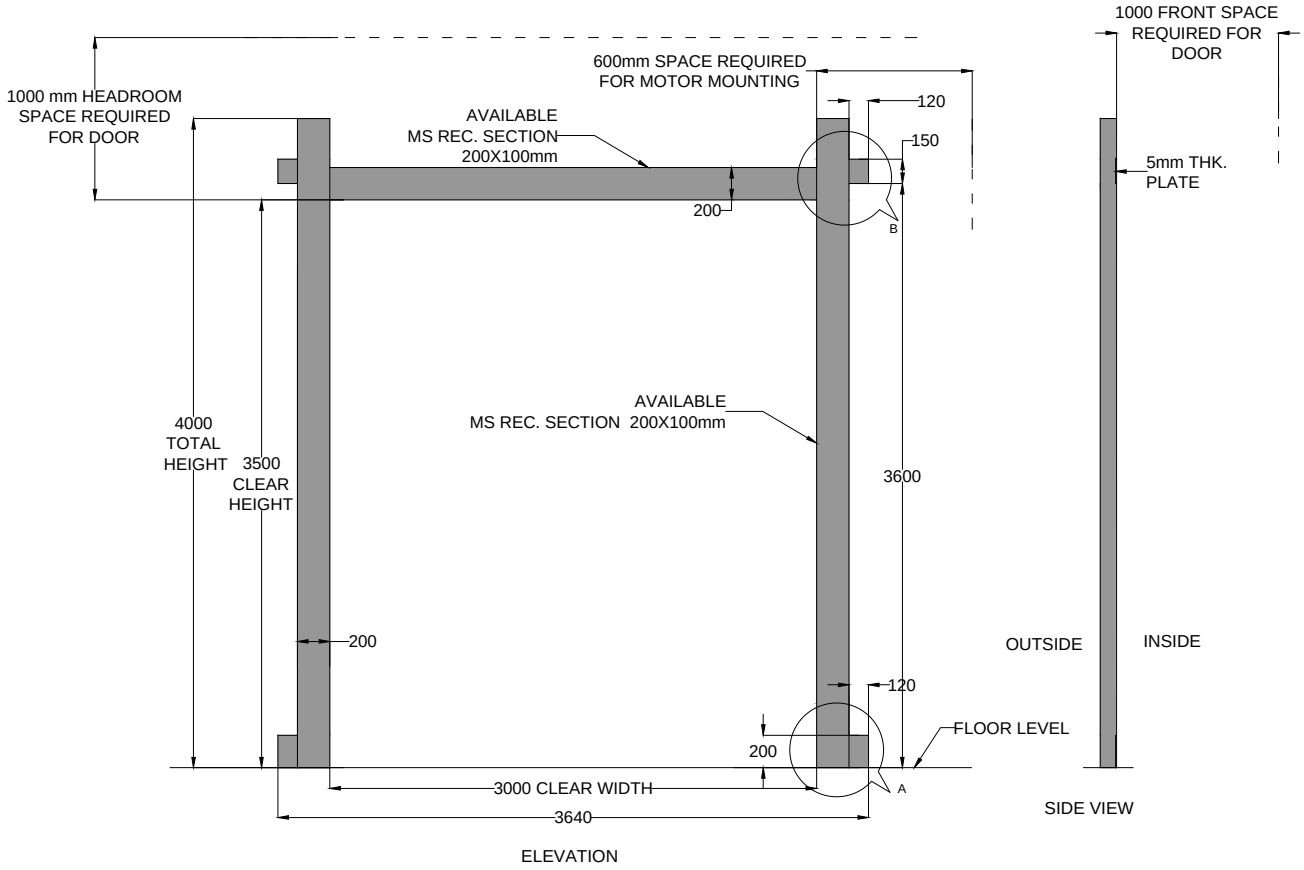

ELEVATION

SIDE VIEW

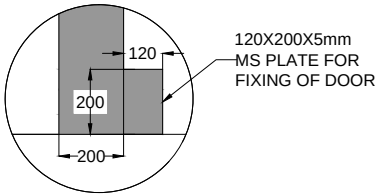

DETAILED VIEW OF A

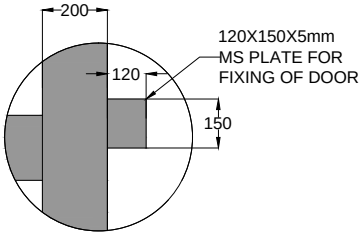

DETAILED VIEW OF B

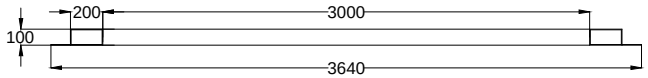

PLAN

DOOR WIDTH	DOOR HEIGHT	QUANTITY
3000 mm	3500 mm	1 NOS

REV NO	DATE	DESCRIPTION
REV -0	22/09/17	INITIAL DRAWING
REV -1	24/11/17	STRUCTURE SECTIONS ARE REVISED ISMC150 TO RHS 200X100

This drawing & design is the property of NIHVA TECHNOLOGIES. Not to be sold or copied to any other concern.

TITLE: STRUCTURE FOR HSD RR 3000 ISO

	SIGN	DATE
DRAWN	OMKAR	22/09/17
CHECK	SHEKHAR	22/09/17
REV.		
APPROVAL	SHEKHAR	22/09/17

If any queries contact : design@nihva.com

ALL DIMENSION ARE IN mm

NIHVA TECHNOLOGIES PVT. LTD.
NIHVA TECHNOLOGIES PVT. LTD. PUNE
Tel : 020 66304033
Email:- info@nihva.com
Website:- www.nihva.com

CLIENT - FERRERO INDIA PVT. LTD.

PROJECT -

SITE - BARAMATI

DWG. NO. : NIHVA/17-18/0211/R01 | REV -1

SCALE: NTS | WT: | SHEET: 01 OF 01