


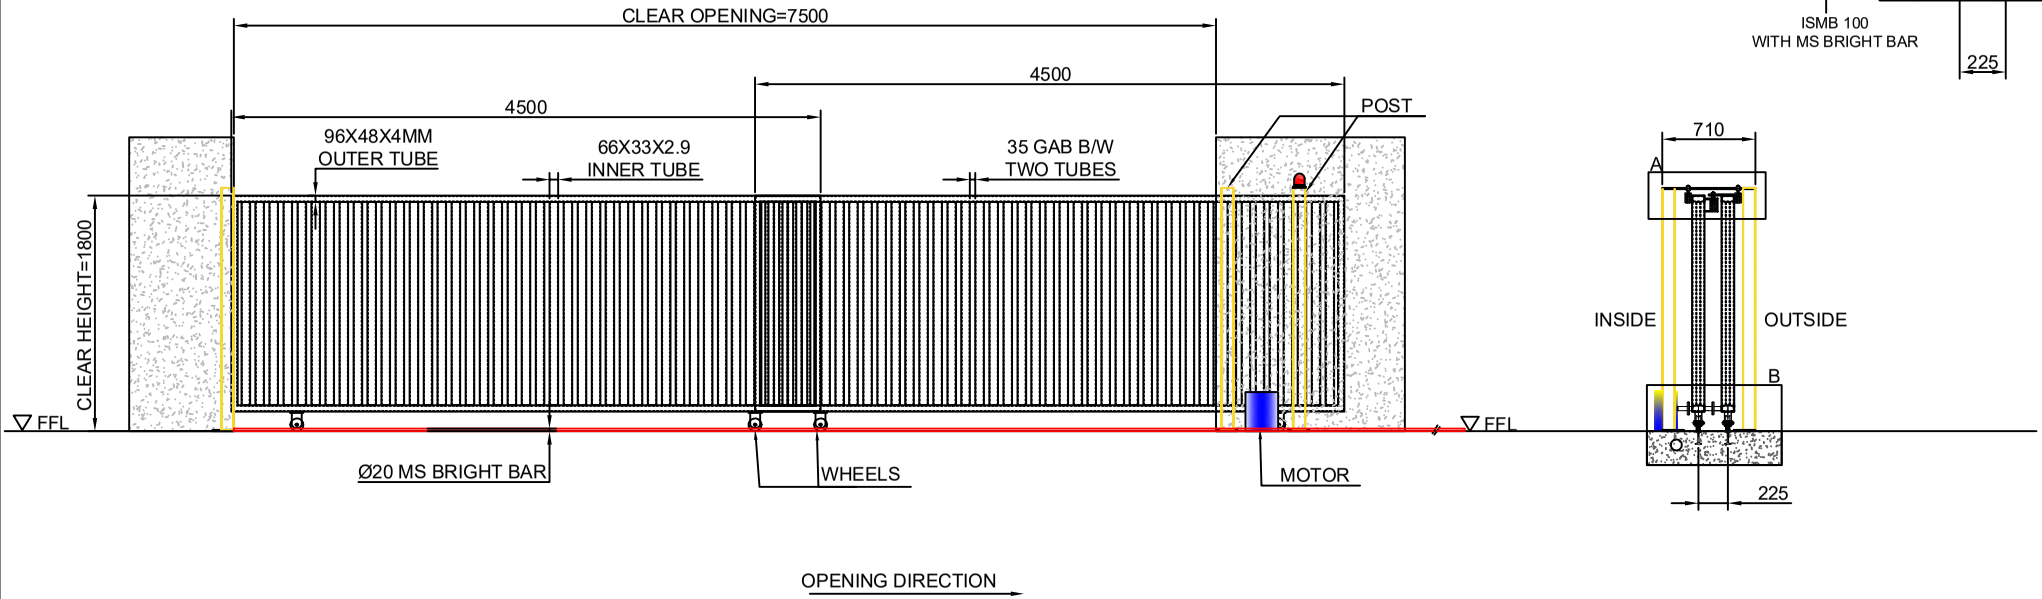

NOTE:-

1.ALL DIMENSION ARE IN MM

2.FIBRICATION TOLERANCE WILL BE ±10MM

3.REQUIRED ALL CIVIL WORK WILL BE IN CLIENT SCOPE

4.REQUIRED PARKING WILL BE 4600MM

This drawing & design is the property of NIHVA TECHNOLOGIES. Not to be sold or copied to any other concern.

TITLE:- Two Leaf for tel.sliding gate	NAME	DATE	SIGN
DRAWN	SUJATA	02/03/2022	
CHECK	G.PATIL	02/03/2022	
APPRD.	P.J	02/03/2022	

NIHVA TECHNOLOGIES PVT. LTD.
NIHVA TECHNOLOGIES PVT. LTD. PUNE
Tel : 020 66304033
Email:- info@nihva.com
Website:- www.nihva.com

CLIENT - Kunal Structure Ind. Pvt. Ltd			
LOCATION - Gujrat (Diyodar)			
PRODUCT - Tel.sliding gate			QTY-
If any queries contact : design@nihva.com	DWG NO:- NIHVA/21-22/CLT/0357		REV- 0
ALL DIMENSION ARE IN mm	SCALE: NTS	SCALE:-- 1:1	SHEET: 01 OF 01

Rev No.	Revision	Date	Revised By