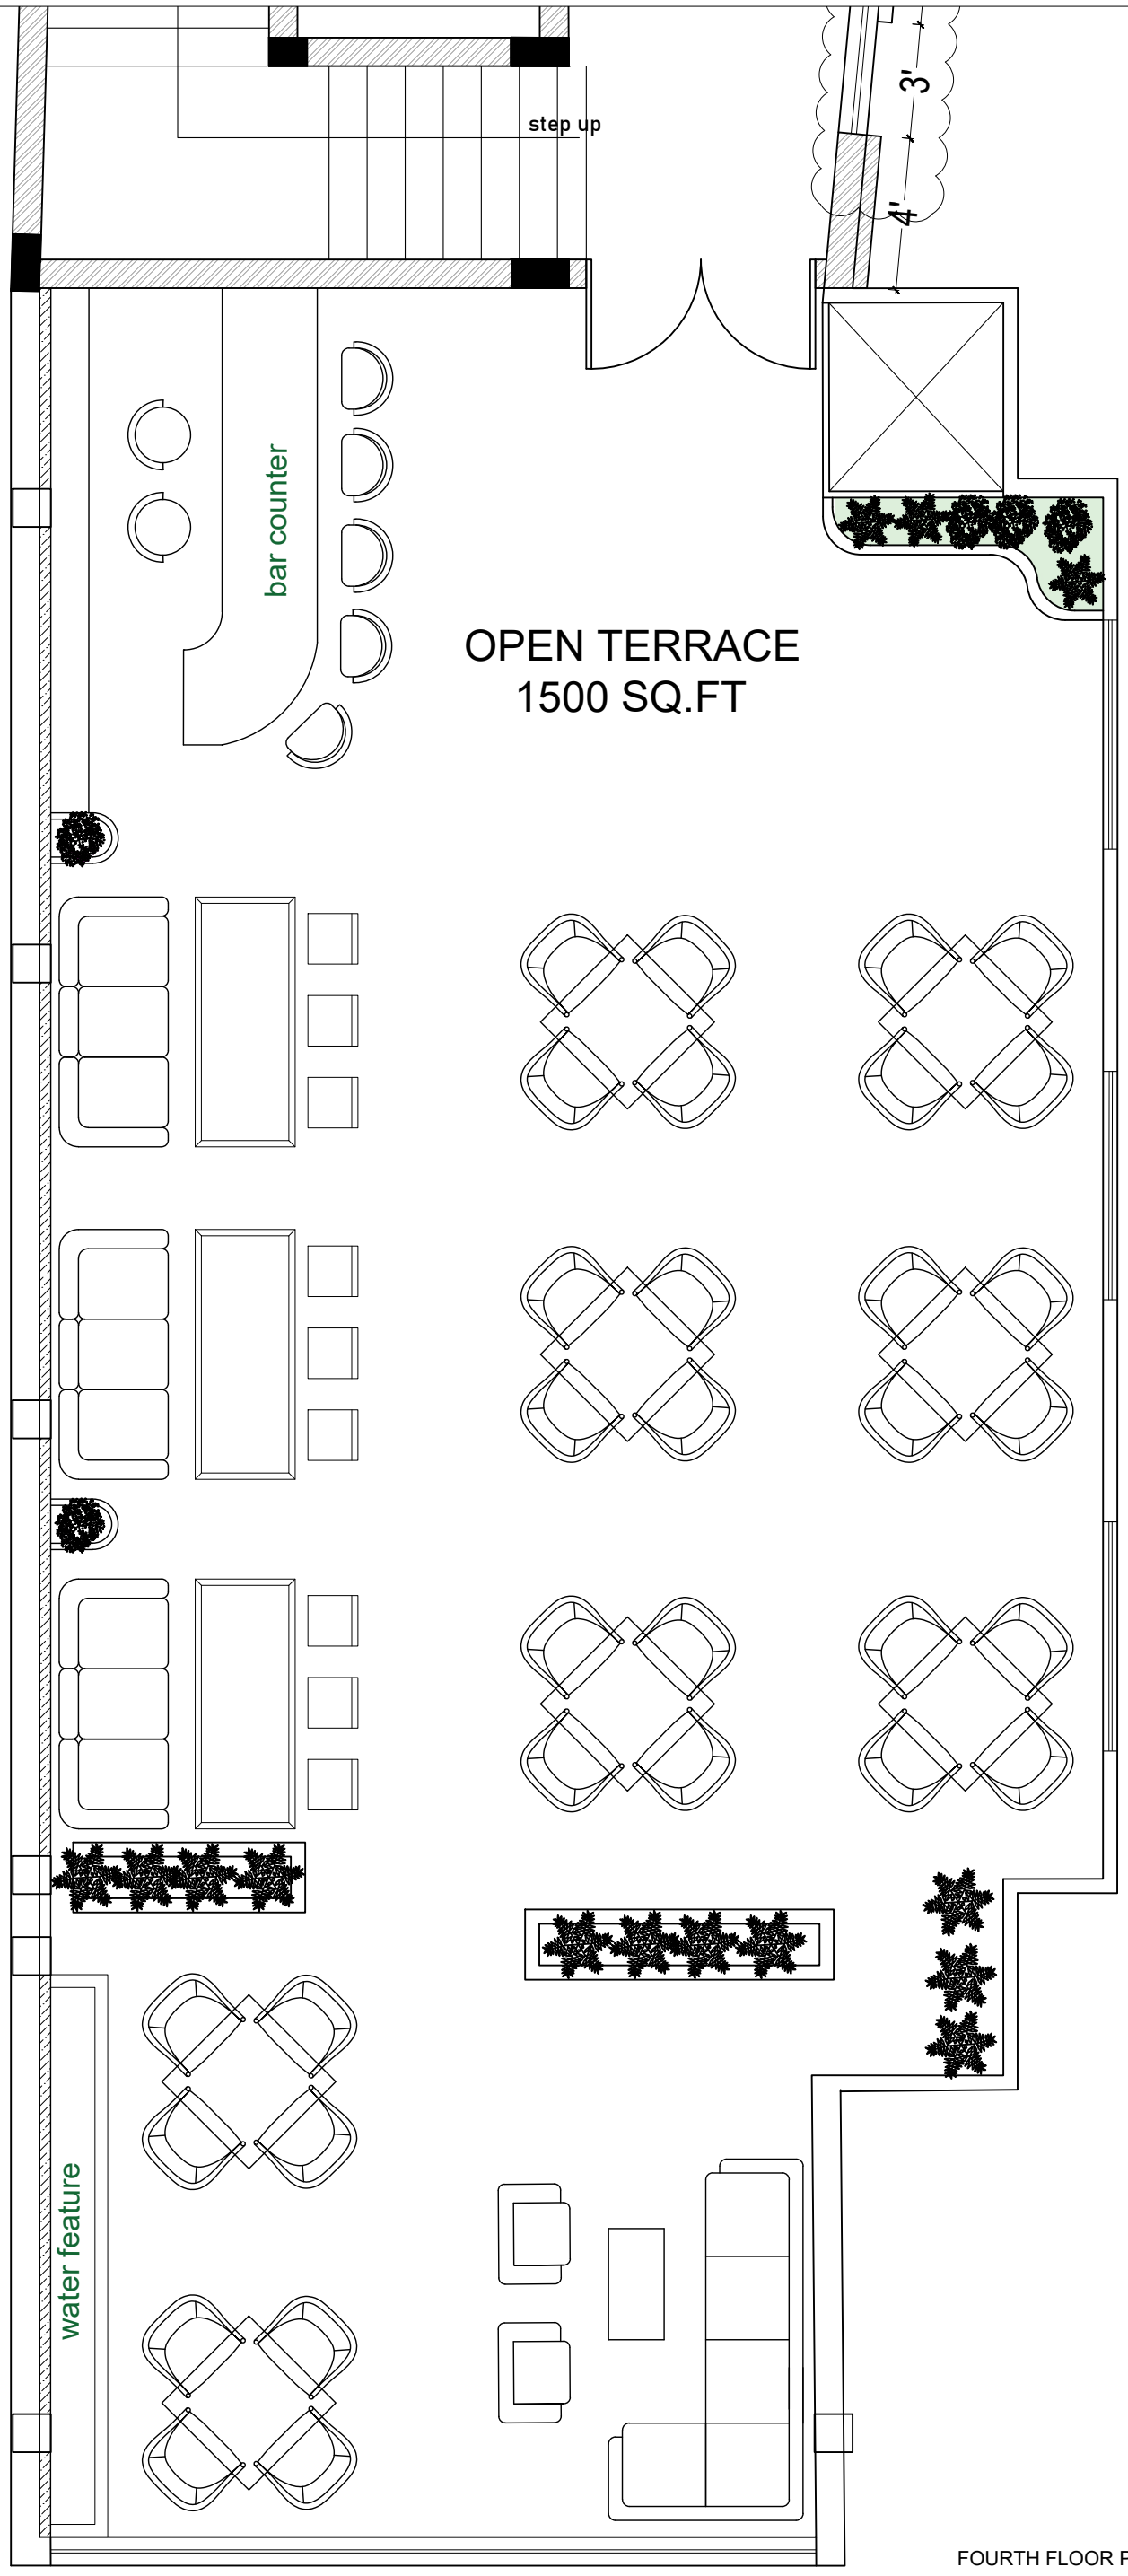


FOURTH FLOOR PLAN

N

These drawing are the COPYRIGHT of Design Legends Group. Unauthorised copying is not permitted.

NOTES

- ALL Dimensions Are in FEET & INCHES
- Dimensions are not to be scaled only written dimensions to be followed
- Contractor must verify all dimensions at site before commencement of any work.
- Contractor must notify Architect and/or Project Manager of all discrepancies in the drawing.
- All drawings are inter-related and shall be read in conjuction with relevant Architectural, structural & Services DRG.

KEY PLAN

DRAWING TYPE:-
GOOD FOR CONSTRUCTION.

ARCHITECT & DESIGNER:-
AR. MADHUR GUPTA
INTERIOR DESIGNER:-
ID. NITIKA MAHAJAN

DESIGN LEGENDS GROUP
ARCHITECTURE.INTERIORS.CONSTRUCTIONS
Pathankot office:
1st. floor, Shama iron & H/W Store,
Sujanpur, Pathankot - 145023
Website:- www.designlegends.in
e-mail:- info@designlegends.in
Ph.07696617111, 9056617111

LEGEND:

E. SHAFT= ELECTRICAL SHAFT
P. SHAFT= PLUMBING SHAFT

Drawing Remarks:

Area	Sq.ft
SERVICE CORE	510sq.ft
RESTAURANT	1290 sq. ft
BANQUET HALL	1828 sq. ft
KITCHEN	1336 sq. ft
STAFF CAFETERIA	150 sq. ft
TERRACE GARDEN	1502 sq. ft
GUEST LOBBY	465 sq.ft
PUBLIC WASHROOM	283 sq.ft
TERRACE GARDEN	1502 sq. ft
TOTAL SLAB AREA	8275 sq.ft

CLIENT:-
MARSHAL HOSPITALITIES

PROJECT TITLE:-

MARSHAL HOSPITALITIES
ABOVE TATA CROMA
DALHOUSIE ROAD MAMOON
CHOWK
PATHANKOT

DRAWING TITLE:-

TERRACE PLAN WITH SEATING

DRAWN BY : AABHA GAUTAM
CHECKED BY :
SCALE : N.T.S
DATE : 13-06-26

REV. NO- R9