

Abbrevation's:
WOW-Wall Opening Width
WOH-Wall Opening Height
UC-Under Cut
FFL-Finished Floor Level

ASSESORIES DETALES

(a) HINGES: SS Ball bearing butt hinges size 100x75x3mm

(b) LOCK : Mortise Dead lock,Cylinder(Both side key) with Escutcheon

(c) DOOR CLOSER


(d) HANDLE : 1) SS D Handle(254 mm) FROM OUTSIDE
2) SS PUSH PLATE FROM INSIDE.

(e) CONCEALED FLUSH BOLT-300mm

(f) VISION PANEL- FRAME LESS VISION PANEL OF DOUBLE POLYCARBONATE SHEET OF SIZE 350X750mm.

Shutter thickness : 47 mm
Frame Sheet thick : 1.2mm
Shutter sheet thick :0.8mm
Fixing : On Soliid Brick plasterd wall with Anchors


NOTE:- *All Dimensions are in mm.
*Tolerance:-All Linear Dimensions ±3mm,Others ±0.5mm.
*The Drawing Is For Location of Hardware only. Drawing Does Not Represent The Hardware For More Clarity, Please Go Through Hardware Broucher.

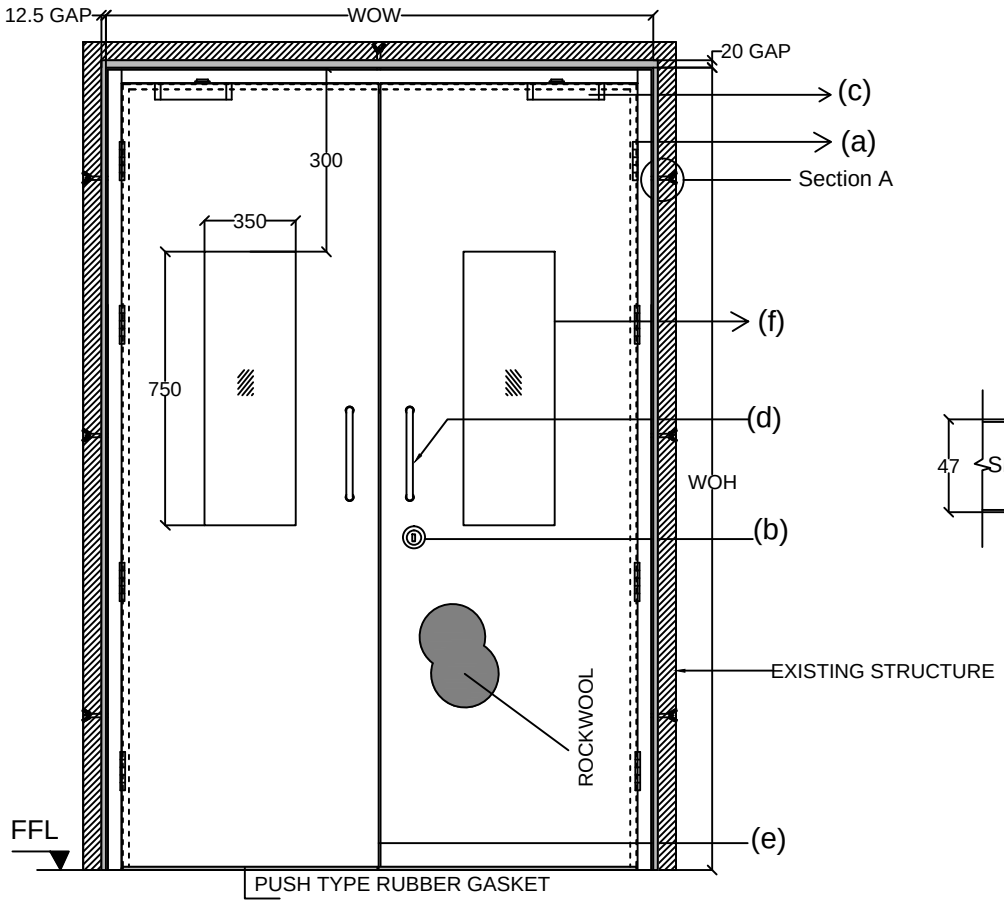

OUTSIDE ELEVATION



PLAN

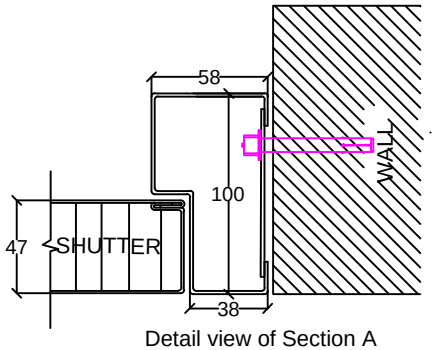

Detail view of Section A

Steel door size		
WOW	WOH	QUANTITY
1970	2200	1

ORIENTATION- TYPE 8 RIGHT HAND REVERSE ACTIVE

COLOR:- Sapphire Blue(RAL 5003)

This drawing & designing is the property of NIHVA TECHNOLOGIES. Not be sold or copy to any other concern.

STEEL DOOR

CLIENT APPROVAL

ALL DIMENSION ARE IN mm

	NAME	DATE	SIGN.
DRAWN	OMKAR	06/09/16	
CHECK	ANIL	06/09/16	
REV.	0		
APPRD.			
MFG			

NIHVA TECHNOLOGIES PVT. LTD.

NIHVA TECHNOLOGY PVT. LTD. PUNE
Tel : 020 66304033
Email:- info@nihva.com
Website:-www.nihva.com

CLIENT - MARS INTERNATIONAL
PROJECT -
SITE - KHED CITY
DWG. NO. - NIHVA/16-17/0072
SCALE:NTS | WT: | SHEET: 01 OF 01
If any queries contact : projects@nihva.com