A

C1 C2 C3 C4 C5 C6 C7 C8 C9 C10 C11

C12

C13 C14 C15 C16 C17 C18 C19 C20

230thk
r.c.c. deck

LD LIFT
2.17X1.94

C21 C22

C23 C24 C25 C26 C27 C28

C35 C36 C37

C38 C39

4250

C29 C30 C31 C32 C33 C34

C40 C41

C50

C42 C43 C44 C45 C46 C47 C48 C49

SB


C51 C52

C53 C54

C55 C56 C57 C58 C59 C60 C61 C62 C63 C64 C65 C66

A

ROOF COVER PLAN

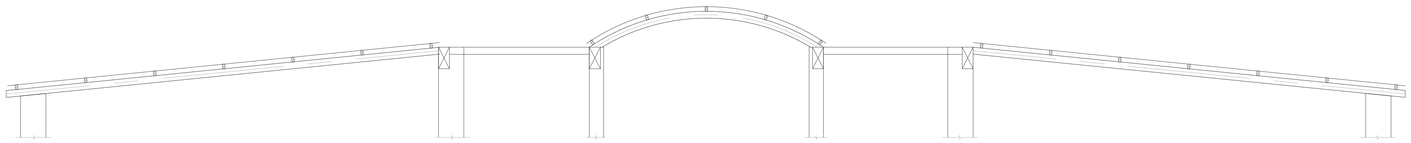

SECTION A-A