
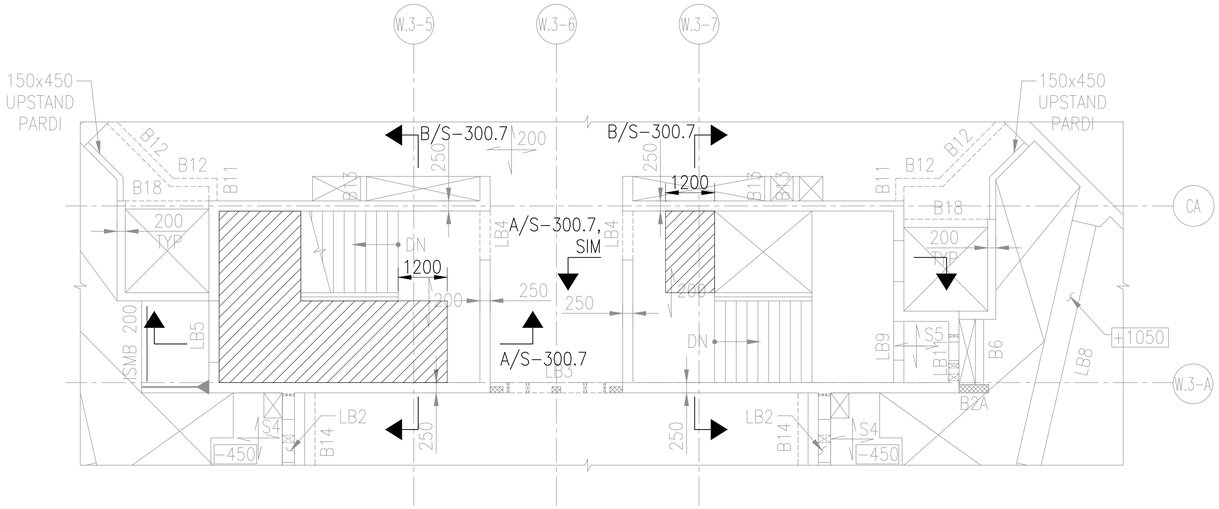


- EXISTING CONDITION & DEMOLITION

REF: S-129, R4 REVISION

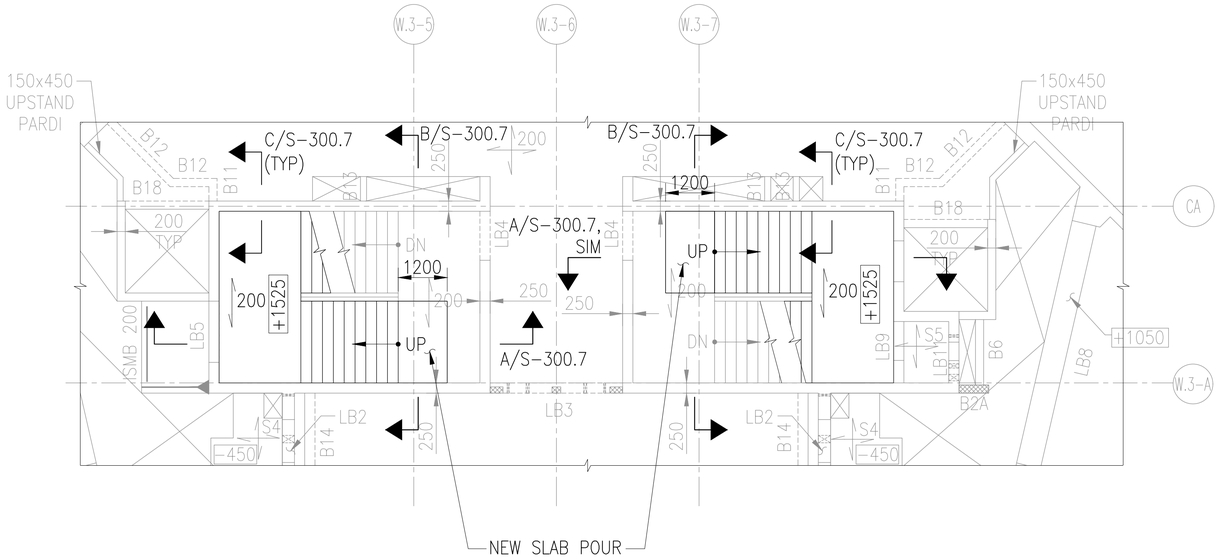

- NEW FRAMING

REF: S-129, R5 REVISION

A PART PLAN - L29

NOTE:

1. ▨ INDICATES EXTENT OF SLAB DEMOLITION.

LERA

Leslie E. Robertson Associates
Consulting Engineers (India), Pvt. Ltd.
The Ruby, North Wing, 23rd Floor,
29 Senapati Bapat Marg,
Dadar West, Mumbai – 400 028 India
Tel: 91 22 2437 6001 and 91 22 2437 6003

Client

Oberoi Realty Limited
Commerz, 3rd Floor, International Business Park,
Oberoi Garden City, Mumbai – 400 063 India
Tel: +91 22 6677 3333 Fax: +91 22 6677 3334

No.	Revision/Issue	Date
R0	ISSUED FOR CONSTRUCTION	27 JAN 23

Warning:

© Copyright LESLIE E. ROBERTSON ASSOCIATES, CONSULTING ENGINEERS (INDIA), PVT. LTD. IT IS A VIOLATION OF LAW FOR ANY PERSON, UNLESS ACTING UNDER THE DIRECTION OF A PROFESSIONAL, LICENSED IN THE STATE OF THIS PROJECT, TO ALTER IN ANY WAY THESE DRAWINGS. WHERE ANY ITEM IS ALTERED, THE SUPERVISING PROFESSIONAL SHALL AFFIX TO THE ITEM HIS SEAL AND THE INSCRIPTION "ALTERED BY" FOLLOWED BY HIS SIGNATURE, THE DATE, AND A SPECIFIC DESCRIPTION OF THE ALTERATIONS.

Professional Stamp:

Phase:
GOOD FOR CONSTRUCTION

Project Title:
MAXIMA

Drawing Title:
SECTIONS & DETAILS

Drawn: LERA	Design: LERA
Check: LERA	Date: 27 JANUARY 2023
Scale: 1:75	Project Number: P 992

Sheet:
S-300.6