

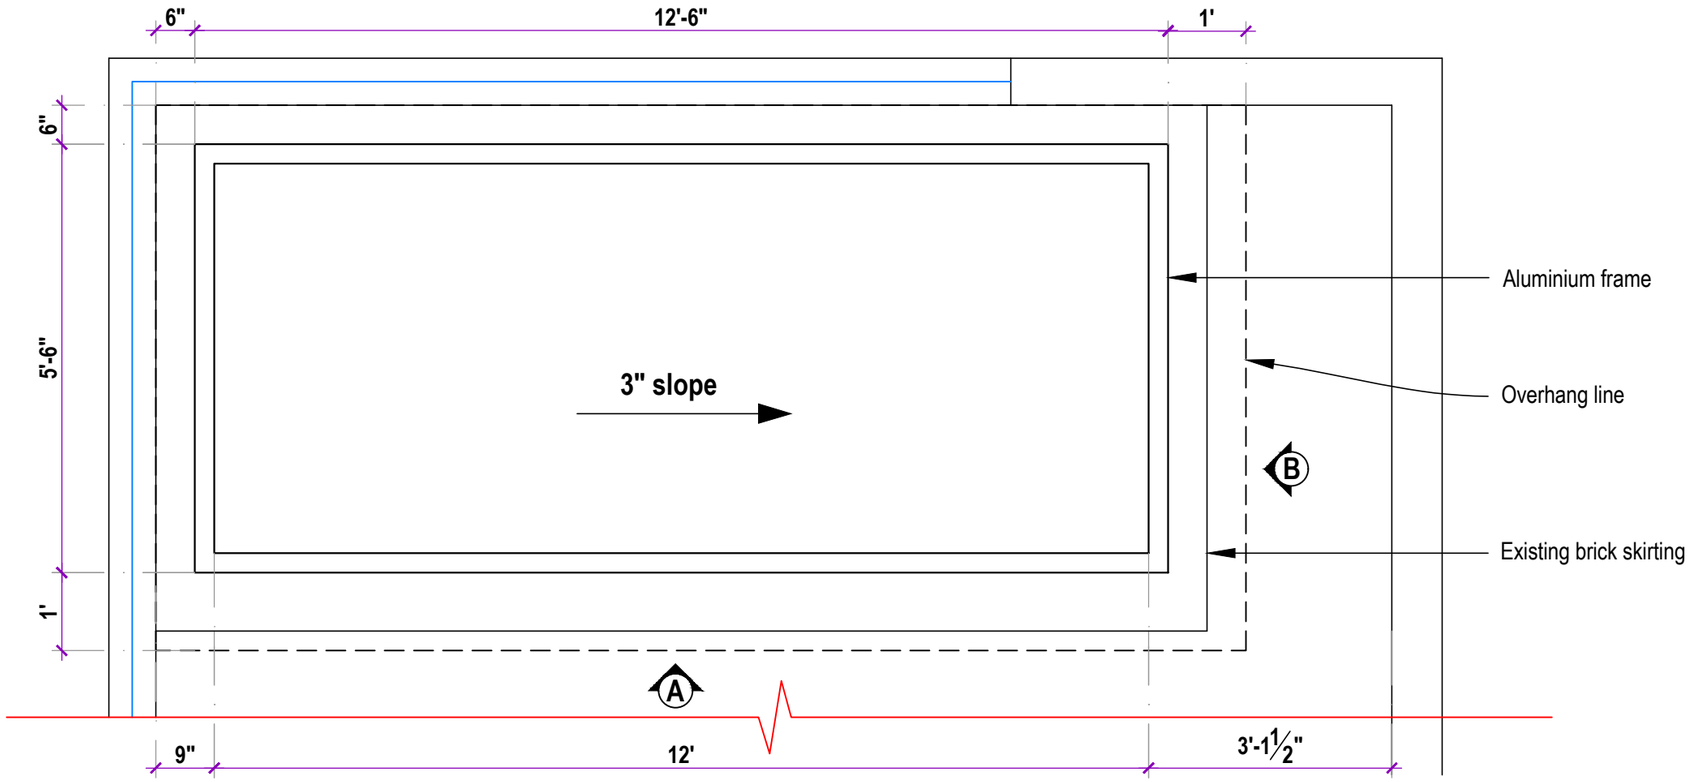


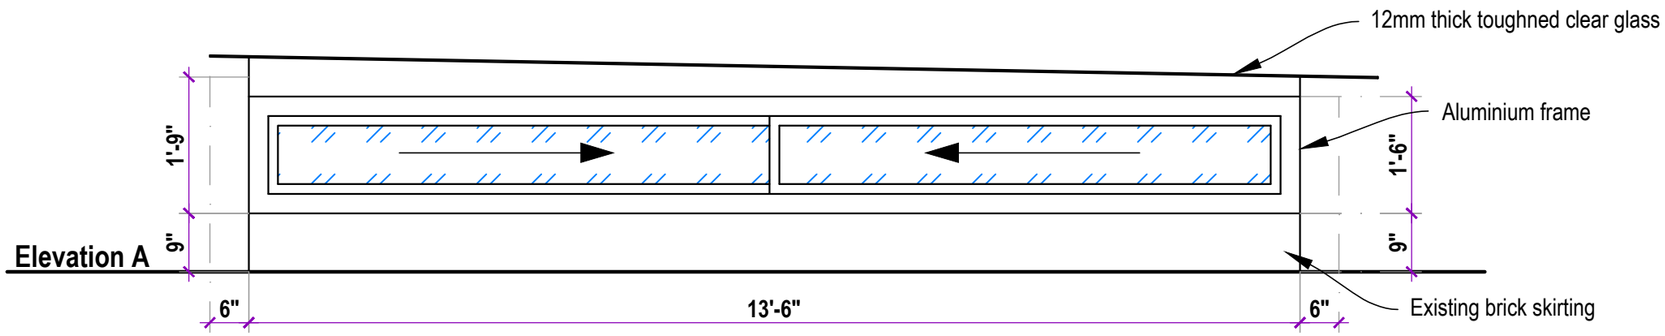

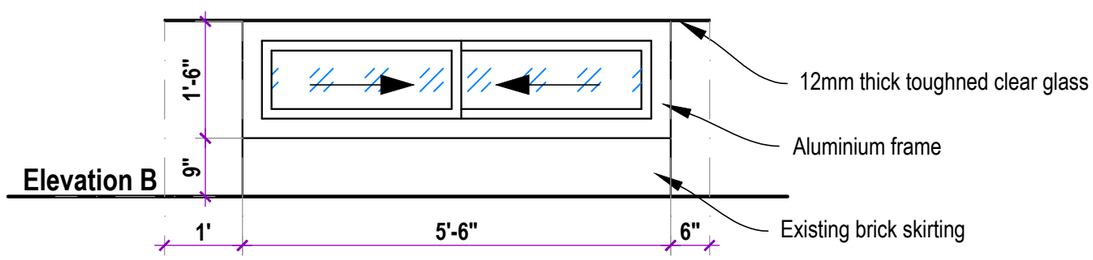

PLEASE NOTE:

This drawing is the copyright of Design Harmony.
This drawing should not be reprinted or copied without prior permission of Design Harmony for any purpose - academic, personal or commercial.
All measurements are to be read only.
Any intended deviations at site from details in drawing need to be approved by Design Harmony.
Any noted discrepancies from drawing to site status need to be brought to the notice of Design Harmony immediately.

S.NO.	REVISION	DATE

PROJECT TITLE
PROPOSED RESIDENTIAL INTERIORS FOR MR. SRIKANTH AND MRS. SUPRIYA AT VILLA 47, NCC URBAN GREENS

DRAWING TYPE
GFC

DRAWING TITLE
SKYLIGHT DETAILS

Dwg no.	236/gfc/
Date	20-03-2023
Drawn By	Thushara

POETRY OF SPACE
design harmony
Sustainable Architecture I Interiors I Landscape
2, Gospaze, Fourth Floor SSR Complex,
Thubarahalli, Whitefield Bengaluru-66
+919686669602 jaya@designharmony.in