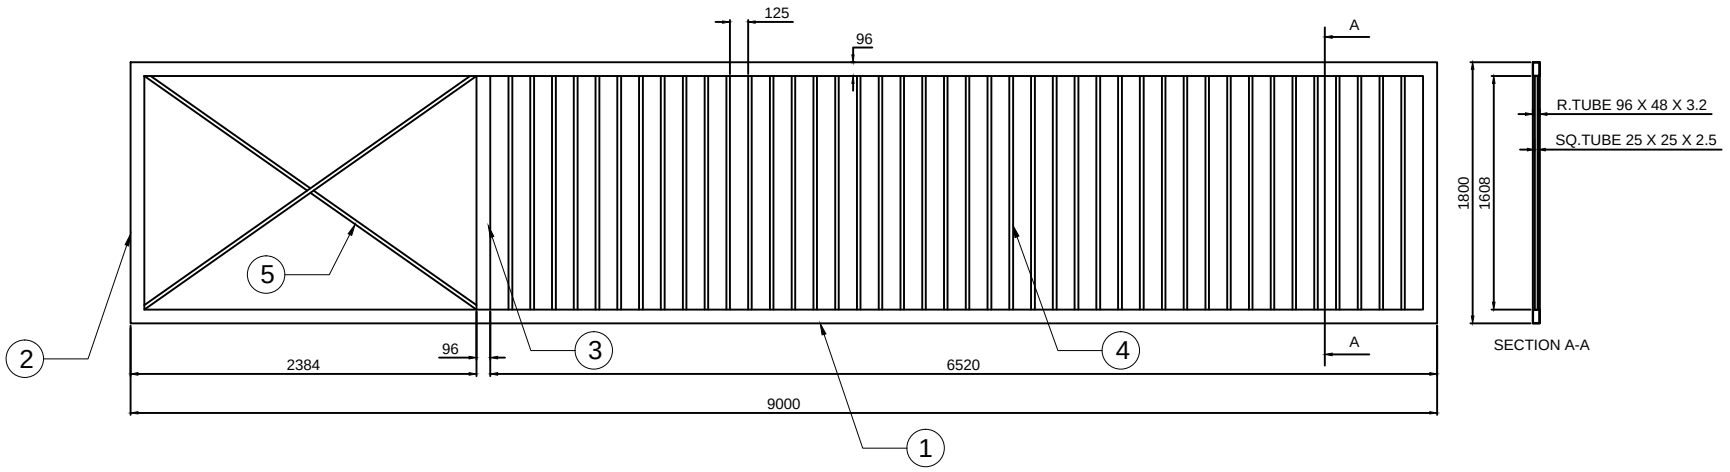


SR NO	DESCRIPTION	SPECIFICATION	QTY
5	SQ.TUBE	25 X 25 X 2.6 THK X 2800L	2 NOS
4	SQ.TUBE	25 X 25 X 2.6 THK X 1608L	43 NOS
3	R.TUBE	100 X 50 X 3.2 THK X 1608L	1 NO
2	R.TUBE	100 X 50 X 3.2 THK X 1800L	2 NOS
1	R.TUBE	100 X 50 X 3.2 THK X 9000L	2 NOS

TOLERANCE- ±2mm

This drawing & design is the property of NIHVA TECHNOLOGIES. Not to be sold or copied to any other concern.

TITLE: LEAF

NIHVA TECHNOLOGIES PVT. LTD.

NIHVA TECHNOLOGIES PVT. LTD. PUNE
Tel : 020 66304033
Email:- info@nihva.com
Website:- www.nihva.com

	NAME	SIGN	DATE
DRAWN	P.A		01.02.2020
CHECK	G.J		01.02.2020
APPRD.			

CLIENT -

PROJECT -

SITE LOCATION -

If any queries contact : design@nihva.com

DWG. NO. : NIHVA/19-20/VDR/306 REV- R00

ALL DIMENSION ARE IN mm

SCALE: NTS WT: SHEET: