
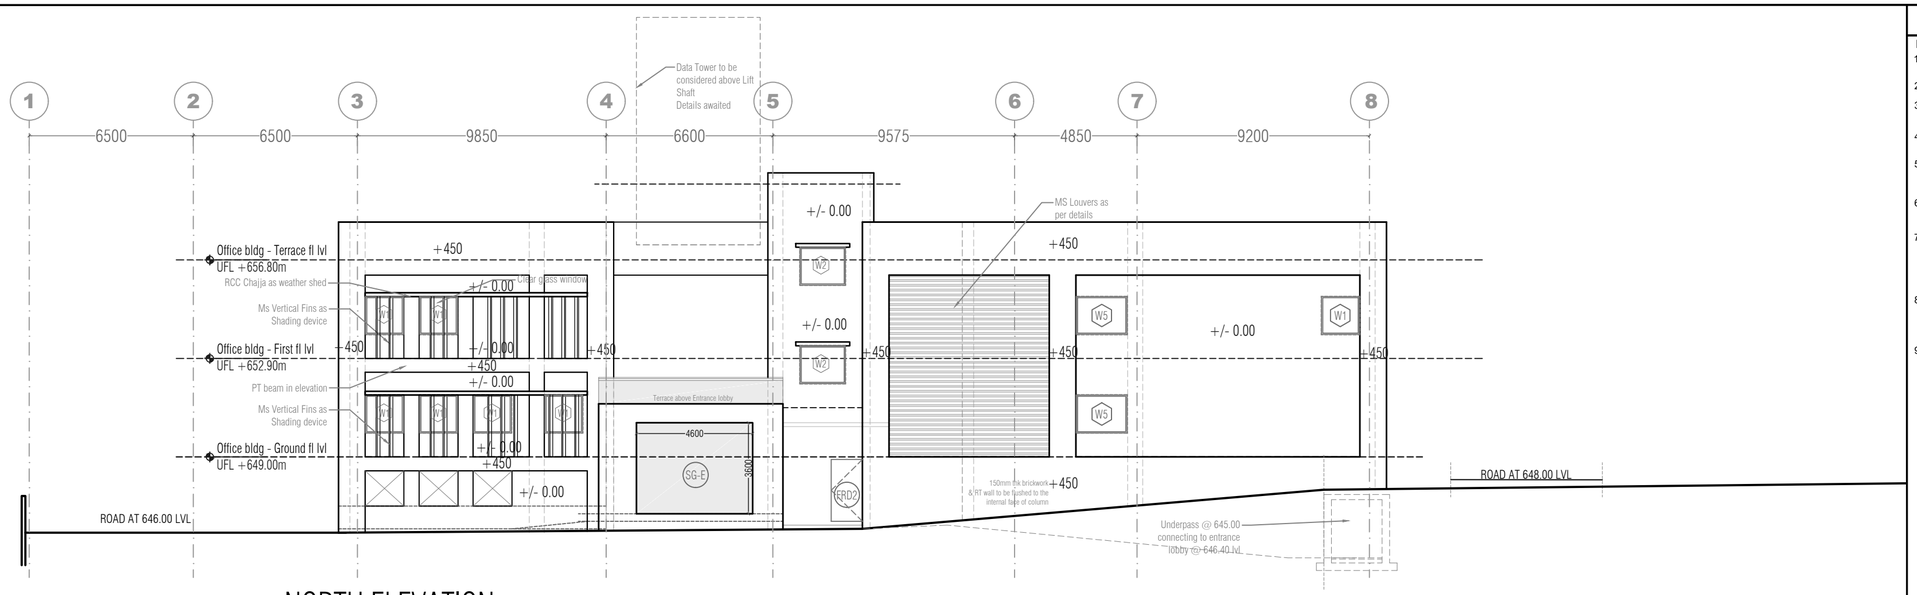


NORTH ELEVATION

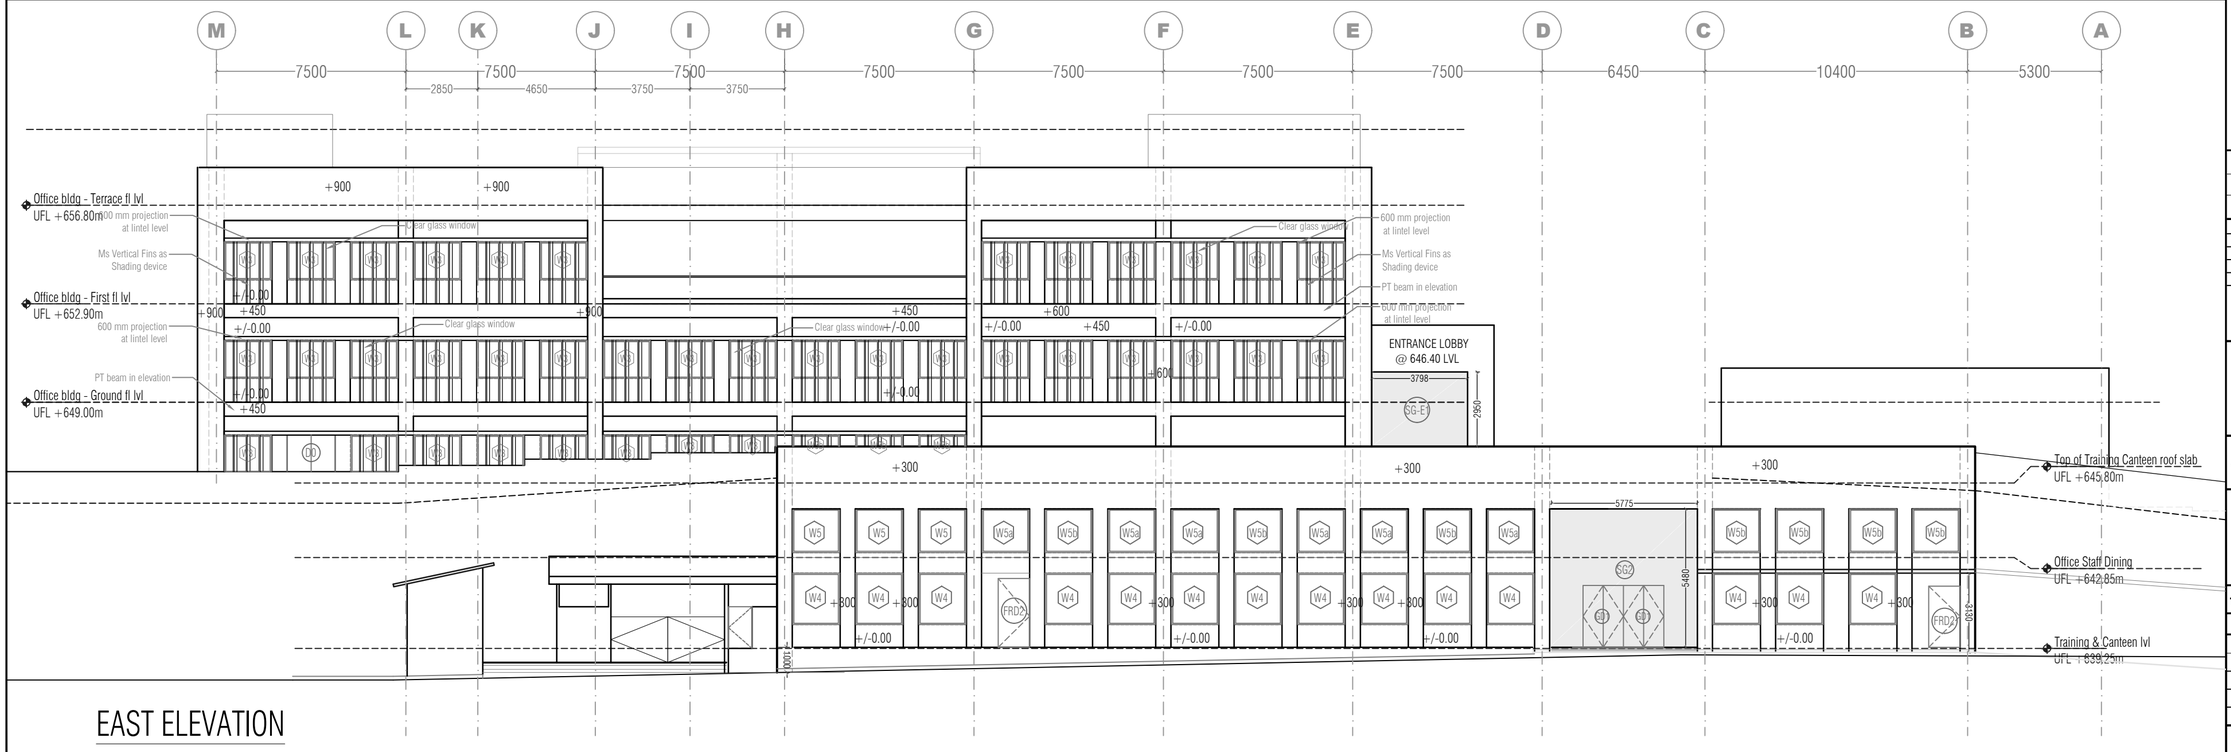

EAST ELEVATION

OFFICE & ANCILLARY BLDG.

NOTES :

1. ALL DIMENSIONS ARE IN MM UNLESS OTHERWISE MENTIONED
2. ONLY WRITTEN DIMENSIONS SHALL BE FOLLOWED
3. DIMENSIONS SHALL BE CHECKED AND CORRELATED WITH STRUCTURAL DRAWINGS
4. LARGER SCALED DRAWINGS SUPERSEDE SMALLER SCALED DRAWINGS
5. ANY DISCREPANCY IN THE DRAWING SHALL BE IMMEDIATELY BROUGHT TO THE NOTICE OF THE ARCHITECT
6. NO WORK ON SITE SHALL PROCEED WITHOUT THE APPROVAL OF **FOURTH DIMENSION ARCHITECTS PVT. LTD**
7. THIS DRAWING IS THE SOLE PROPERTY OF **FOURTH DIMENSION ARCHITECTS PVT. LTD** AND IS NOT TO BE REPRODUCED OR COPIED IN PART OR WHOLE IN ANY FORM AND ON COMPLETION OF PROJECT SHALL BE RETURNED TO ARCHITECS
8. THIS DRAWING CONTAINS COPYRIGHT MATERIAL AND TRADE SECRET INFORMATION BELONGING TO **FOURTH DIMENSION ARCHITECTS PVT LTD** AND ITS CLIENT AS NOTED ABOVE
9. ANY UNAUTHORIZED USE , DISCLOSURE DISSEMINATION OR DUPLICATION OF ANY OF THE INFORMATION CONTAINED HEREIN MAY RESULT IN LIABILITY UNDER APPLICABLE LAW.

NO	REVISION	DATE

LEGEND :

150 MM THK WALL	EXTERNAL & MAIN DIVISION WALLS
300 MM SUNK	
200 MM SUNK	
150 MM SUNK	

ALL SINGLE LAYER EXTERNAL WALLS 150THK AAC BLOCK MASONRY WALL
100 THK AAC BLOCK MASONRY SHOWN AS
300 THK AAC BLOCK MASONRY SHOWN AS
ALL TOILET INTERNAL WALLS 100THK AAC BLOCK MASONRY WALL UNLESS MENTIONED.

PROJECT :

PROPOSED PLANT FOR WILO MATHER & PLATT Pumps Pvt. Ltd. LIMITED, AT CHORDIA INDUSTRIAL PARK, SHIRWAL, SATARA.

CLIENT :

WILO MATHER & PLATT PUMPS PVT. LTD.

FOURTH DIMENSION ARCHITECTS PVT. LTD.
FDAPL ARCHITECTS, PLANNERS, INTERIOR, LANDSCAPE DESIGNERS & LEISURE CONSULTANTS
FD House, Lane No 8, Prabhat Road,
Deccan Gymkhana, Pune – 411004.
Telephone No's : 020- 41000999, +91 9922921701 / 02;
Fax +91-02041000888

TITLE : NORTH & EAST ELEVATIONS

DRAWING STATUS: FOR TENDER

DATE	: 25-Mar-22	**NORTH**
SCALE	: AS MENTIONED	
JOB NO.	: W-IND-0320	
DRAWN BY	: NUPOOR	
CHECK BY	: TEJAL	

DRAWING NO :	**REVISION NO :**
OB-A-302	R0