

Abbrevation's:
WOW-Wall Opening Width
WOH-Wall Opening Height
UC-Under Cut
FFL-Finished Floor Level

ASSESORIES DETALES

(a) HINGES: SS Ball bearing butt hinges size 100x75x3mm

(b) LOCK : Mortise Dead lock,Cylinder(Both side key) with Escutcheon


(c) DOOR CLOSER

(d) HANDLE : D Handle


(e) CONCEALED FLUSH BOLT

Shutter thickness : 47 mm
Frame Sheet thick : 1.2mm
Shutter sheet thick :0.8mm
Fixing : On Soliid Brick plasterd wall with Anchors
Electrostatic powder coated

NOTE:- *All Dimensions are in mm.
*Tolerance:-All Linear Dimensions ±3mm,Others ±0.5mm.
*The Drawing Is For Location of Hardware only. Drawing Does Not Represent The Hardware For More Clarity, Please Go Through Hardware Broucher.

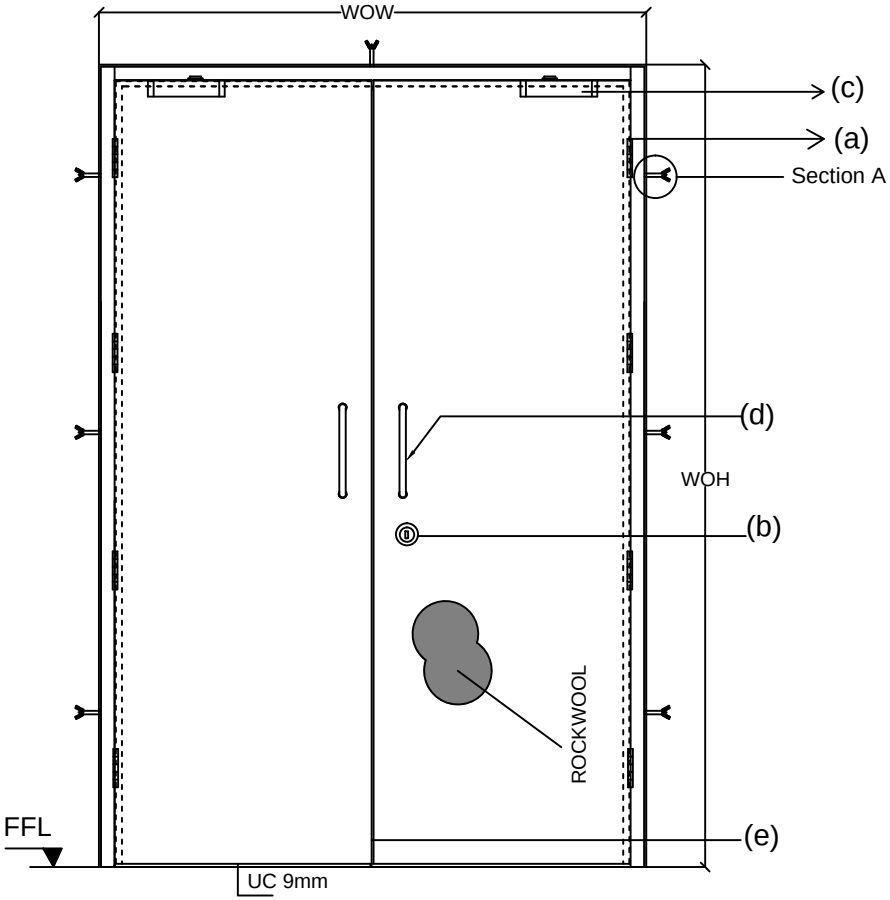

Elevation

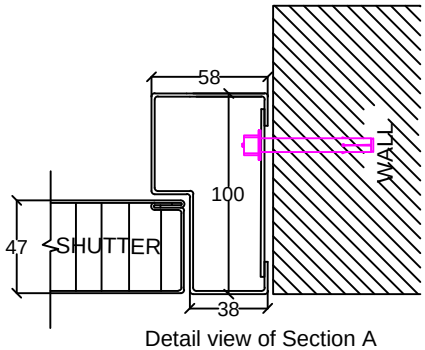

Detail view of Section A

Steel door size

WOW	WOH	TYPE 5	TYPE 6	TYPE 7	TYPE 8	QUANTITY
1500	2200					22
2400	2200					1

NOTE- 1. CLIENT SHOULD SELECT DOOR TYPE FROM DOOR HANDLING SHEET.
2. CLIENT SHOULD MENTION COLOR FOR DOOR.



Top View

COLOR
1.TRAFFIC WHITE (RAL 9016)
2.LIGHT GREY (RAL 7035)
3.GENTION BLUE (RAL 5010)
4.SIGNAL RED (RAL 3001)

This drawing & designing is the property of NIHVA TECHNOLOGIES. Not be sold or copy to any other concern.

STEEL DOOR (DOUBLE LEAF)

CLIENT APPROVAL

ALL DIMENSION ARE IN mm

	NAME	DATE	SIGN.
DRAWN	OMKAR	29/12/16	
CHECK	SAGAR P.	29/12/16	
REV.			
APPRD.	R.K.		
MFG			

NIHVA TECHNOLOGIES PVT. LTD.
NIHVA TECHNOLOGY PVT. LTD. PUNE
Tel : 020 66304033
Email:- info@nihva.com
Website:-www.nihva.com

CLIENT - ZAMIL STEEL BUILDINGS INDIA PVT.LTD.
PROJECT -
SITE -
DWG. NO. - NIHVA/16-17/0119
SCALE:NTS | WT: | SHEET: 01 OF 01
If any queries contact : projects@nihva.com