



PRODUCED BY AN AUTODESK EDUCATIONAL PRODUCT

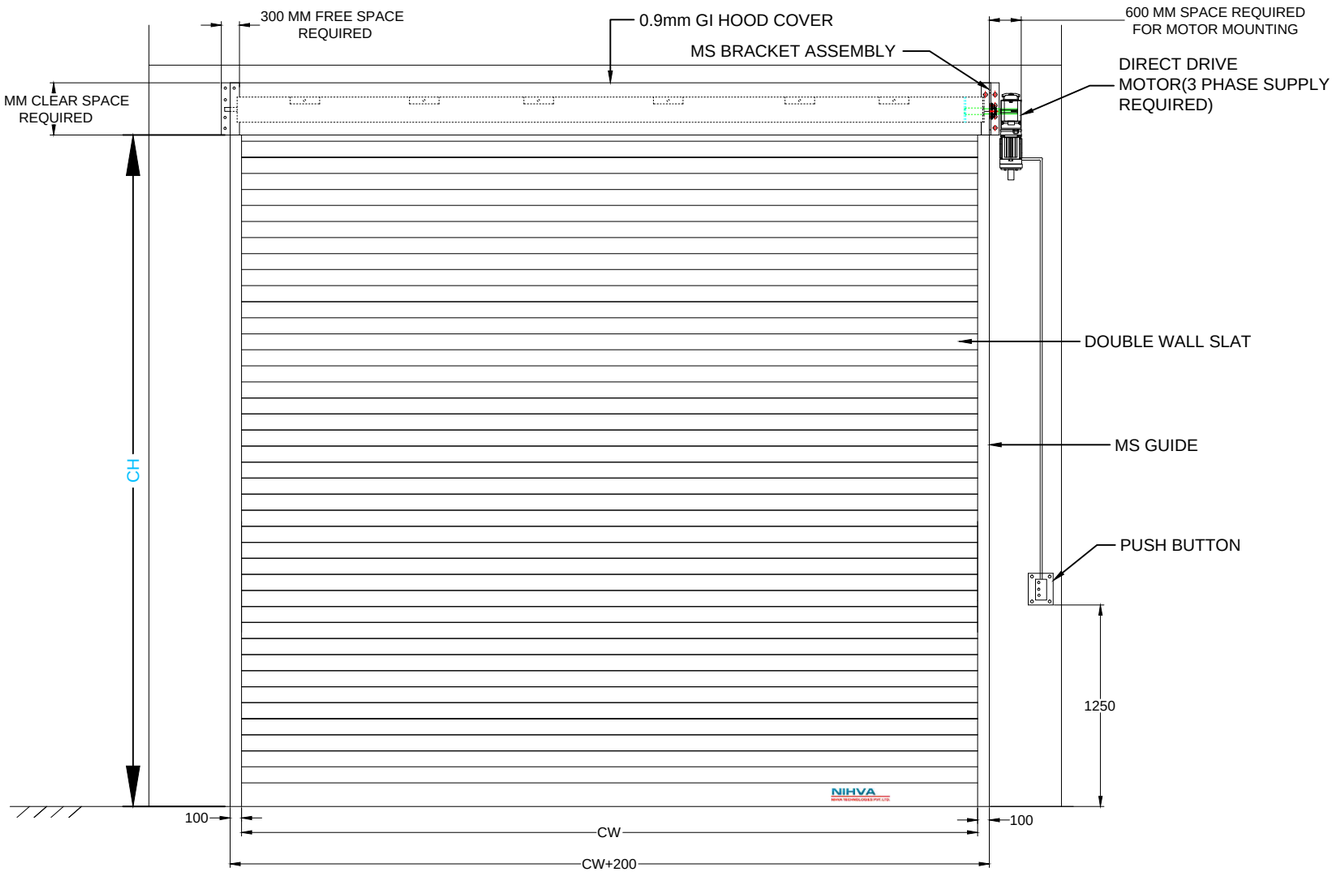

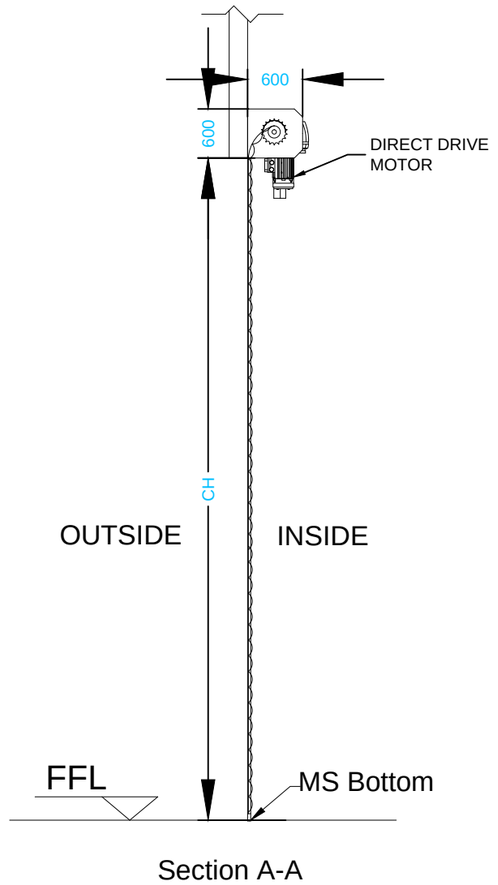


Section A-A

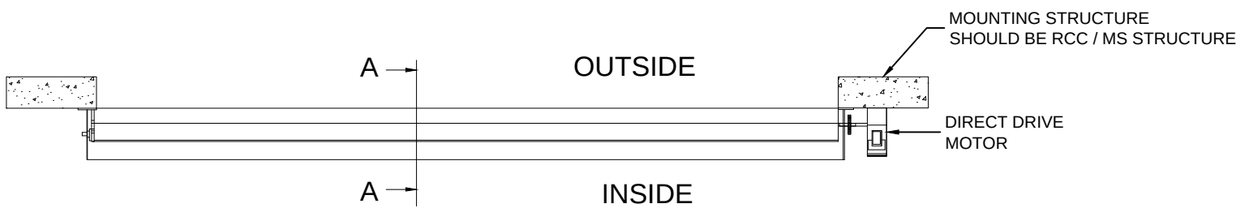

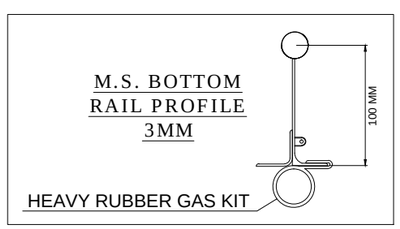

Main Slats
Double Wall Rolling Shutter

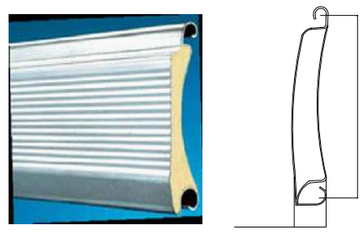

COLOR OF SLATS & SHUTTER -RAL9002 (GRAY WHITE)

DIMENSION :

CLEAR WIDTH	CLEAR HEIGHT	QUANTITY
4600 mm	3900 mm	2 NOS

NOTE:-

1.STRUCTURE FOR SHUTTER WILL BE IN CLIENT'S SCOPE.
2. 3 PHASE SUPPLY SHOULD BE PROVIDED.

NIHVA TECHNOLOGIES PVT. LTD.
NIHVA TECHNOLOGIES PVT. LTD. PUNE
Email:- info@nihva.com
Website:- www.nihva.com

TITLE:

DOUBLE WALL ROLLING SHUTTER
01. LGF south side
02. LGF south side

CLIENT'S APPROVAL :

CLIENT - AJAY KALE AND ASSOSIATE

PROJECT -

SITE LOCATION - PIRANGUT

DWG. NO. : NIHVA/21-22/CLT/280

SCALE: NTS	WT:	SHEET:01 OF 02


DRAWN BY: G.P.	DATE: 23-12-2021
CHECKED BY: A.K.	DATE: 23-12-2021
APPROVED BY :	


If any queries contact : design@nihva.com


NOTE: ALL DIMENSIONS ARE IN mm

THIS DRAWING & DESIGN IS THE PROPERTY OF NIHVA TECHNOLOGIES, NOT TO BE SOLD OR COPIED TO ANY OTHER CONCERN.
PRODUCED BY AN AUTODESK EDUCATIONAL PRODUCT
PRODUCED BY AN AUTODESK EDUCATIONAL PRODUCT

PRODUCED BY AN AUTODESK EDUCATIONAL PRODUCT

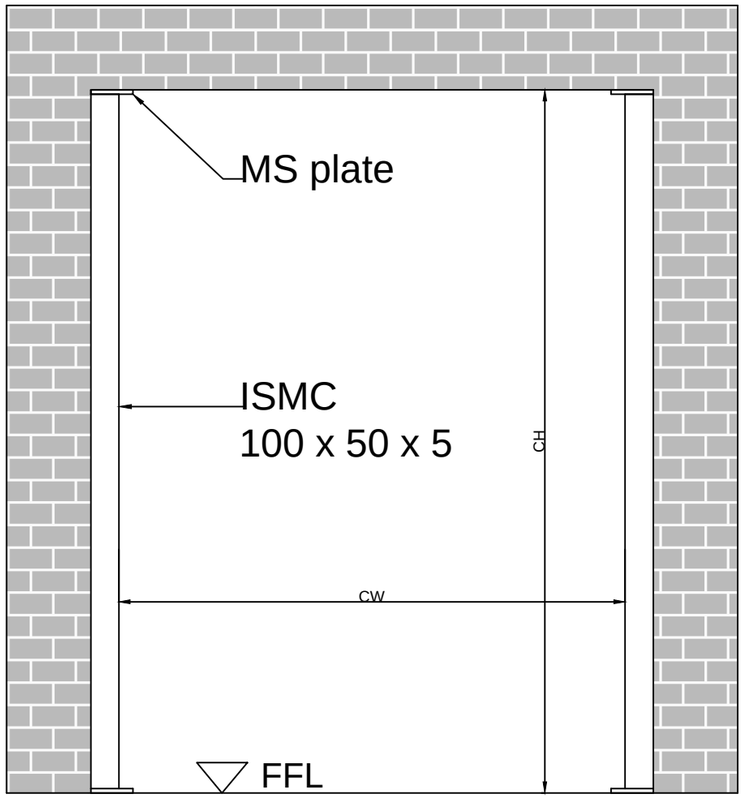

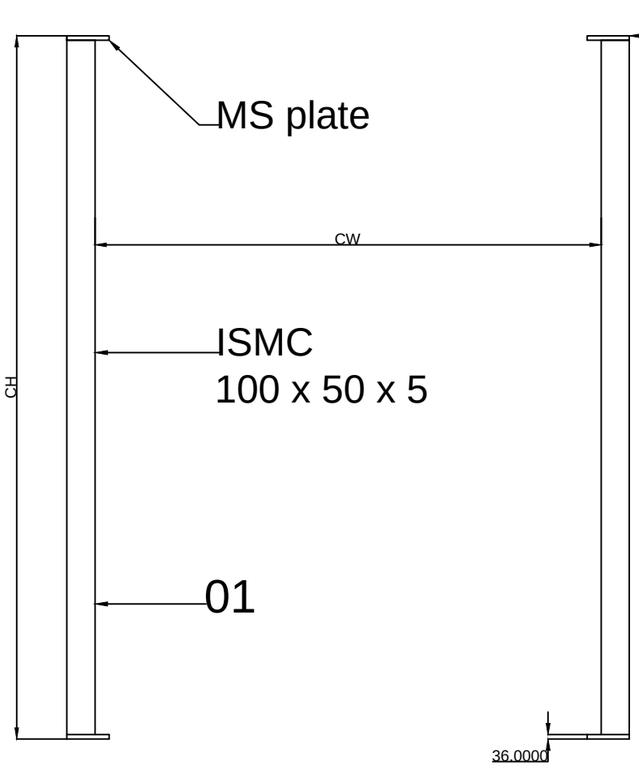

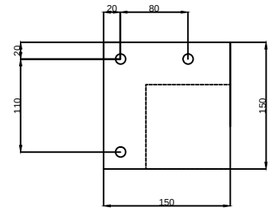

MS plate
Scale: 3:1

Door
Structure

CLEAR WIDTH	CLEAR HEIGHT	Qty
4600	3900	2 nos

This drawing & design is the property of NIHVA TECHNOLOGIES. Not to be sold or copied to any other concern.

TITLE	STRUCTURE			NIHVA TECHNOLOGIES PVT. LTD. PUNE Tel : 020 66304033 Email:- info@nihva.com Website:- www.nihva.com
	NAME	SIGN	DATE	
DRAWN	G.P.		23.12.21	CLIENT :- AJAY KALE AND ASSOSIATE
CHECK	A.K.		23.12.21	PROJECT :-
APPV'ED	V.T		23.12.21	LOCATION :-
If any queries contact : design@nihva.com				DWG. NO. :- NIHVA/21-22/CLT/280 REV :- R00
ALL DIMENSION ARE IN mm				SCALE: NTS WT: SHEET: 02 OF 02

PRODUCED BY AN AUTODESK EDUCATIONAL PRODUCT