
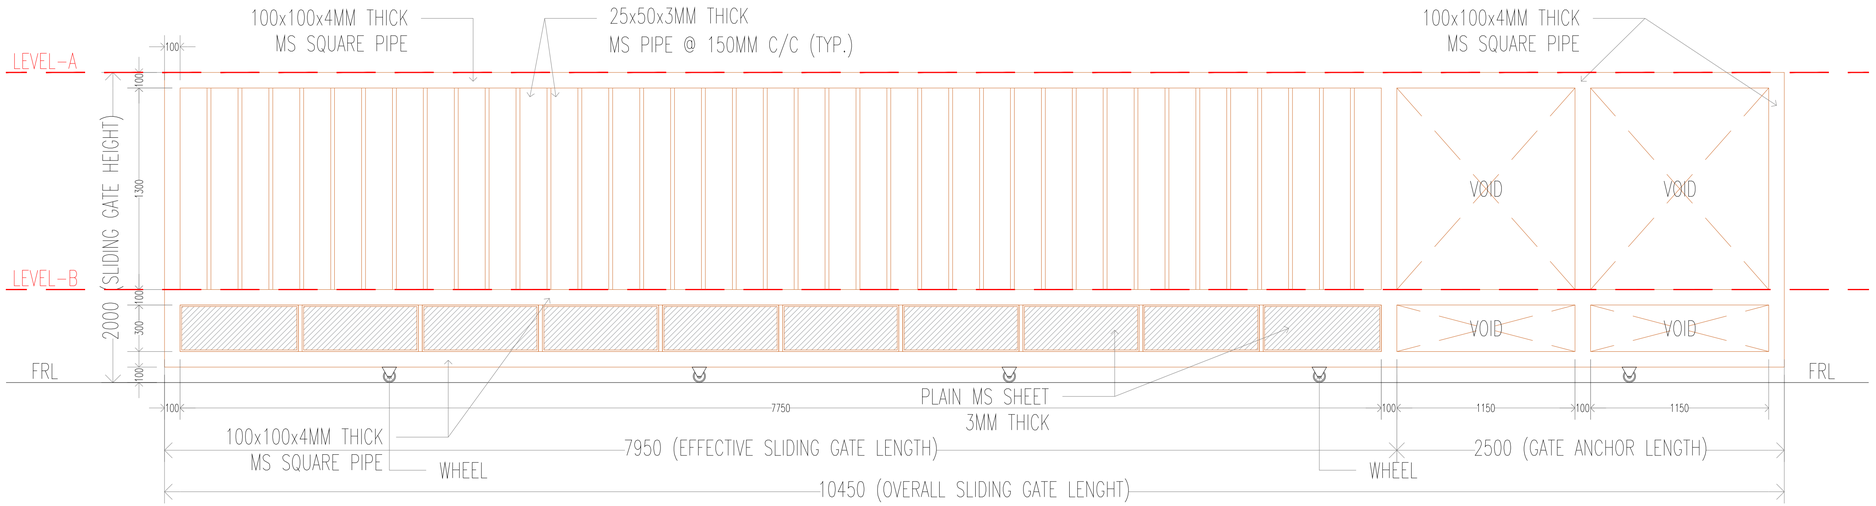



GATE DETAILED ELEVATION

SCALE-1:20

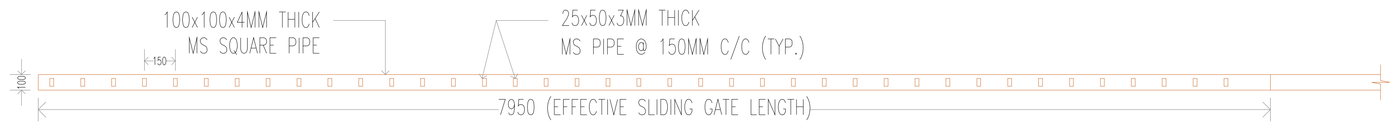


ENTRANCE GATE PLAN AT LEVEL-A

SCALE-1:20

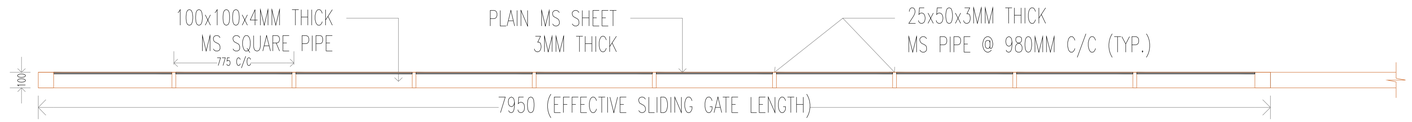


ENTRANCE GATE PLAN AT LEVEL-B

SCALE-1:20

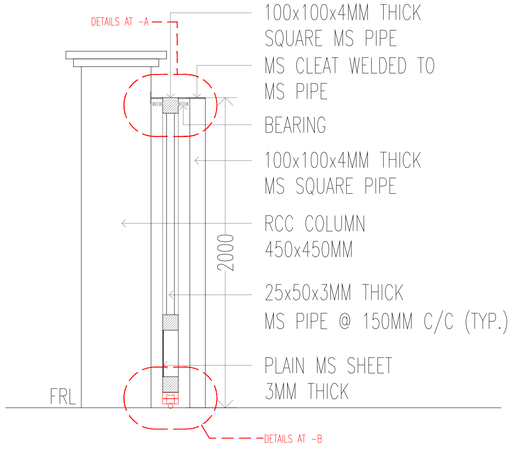


SECTIONAL VIEW

SCALE-1:20

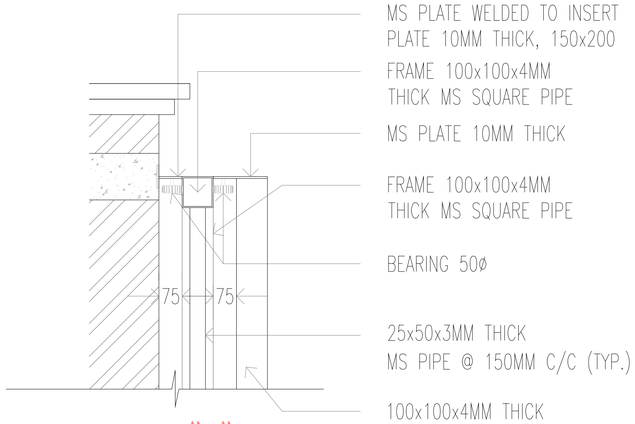

DETAIL AT-"A"

SCALE-1:10

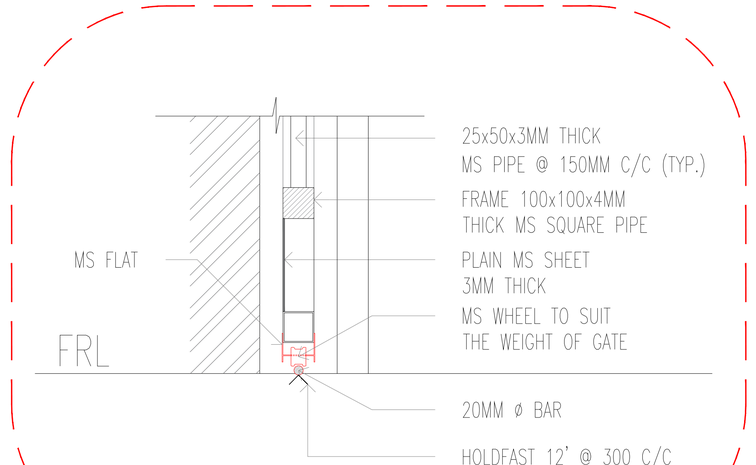

DETAIL AT-"B"


SCALE-1:10

NOTES :

1) ONLY WRITTEN DIMENSIONS ARE TO BE FOLLOWED.
2) READ THIS DRAWING ALONG WITH THE RELEVANT DEPT. DRAWING.
3) ANY AMBIGUITY IN THIS DRAWING TO BE REFERED TO THE CONSULTANT BEFORE EXECUTION OF THE WORK
4) ALL DIMENSIONS ARE IN mm
5)
6)

REVISIONS :

NO.	DATE	REMARKS
R0	18.04.23	RELEASED FOR TENDER

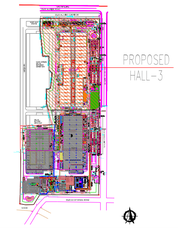Bauherr / client	**Schaeffler India Limited** SCHAEFFLER (Formerly Known as FAG Bearings India Ltd.) GIDC, Savli, Vadodara 391 775. Gujarat, India
Projectname & -address	F4T EXPANSION SAVLI PHASE-2.2 AT-SAVLI, VADODARA, GUJARAT
Übersicht / general plan	 PROPOSED HALL-3
Projekt-management / project management	**Schaeffler Technologies AG & Co. KG** Industriestraße 1-3, 91074 Herzogenaurach, Germany
Entwurfs-verfasser / Designer	ARCHITECTURAL ENGINEERING PROJECTS PVT.LTD. Office No.2016,202,Sai Empire, Baner, PUNE-411045, MAHARASHTRA,INDIA. PH:91-20-66294444,460 www.archivistaindia.com
Status/status Inhalt/content	**TENDER DRAWING** **DETAILS OF ENTRANCE GATE FOR STAFF ENTRY**

Discipline	ARCHITECTURAL	Projektnummer / project number	SCH517	Planformat / plan format	DIN
Datum / date	Gezeichnet	Gepruft	Maßstab / scale	Zeichnungsnummer / plan number	
18.04.2023	G.RAMESHKUMAR	RPJ	AS SHOWN	SCH517_TD_ARCH_SITE_ENT-GATE_006-03_R0	A1

THIS DRAWING IS THE PROPERTY OF ARCHIVISTA ENGINEERING PROJECTS PVT. LTD IT IS ISSUED FOR PRELIMINARY ENGINEERING & APPROVAL. ANY MISUSE, DUPLICATION, ALTERATION OR REUSE FOR ANOTHER PURPOSE IS STRICTLY PROHIBITED & SHALL BE DEALT LEGALLY.ALL RIGHTS RESERVED WITH THE COMPANY.