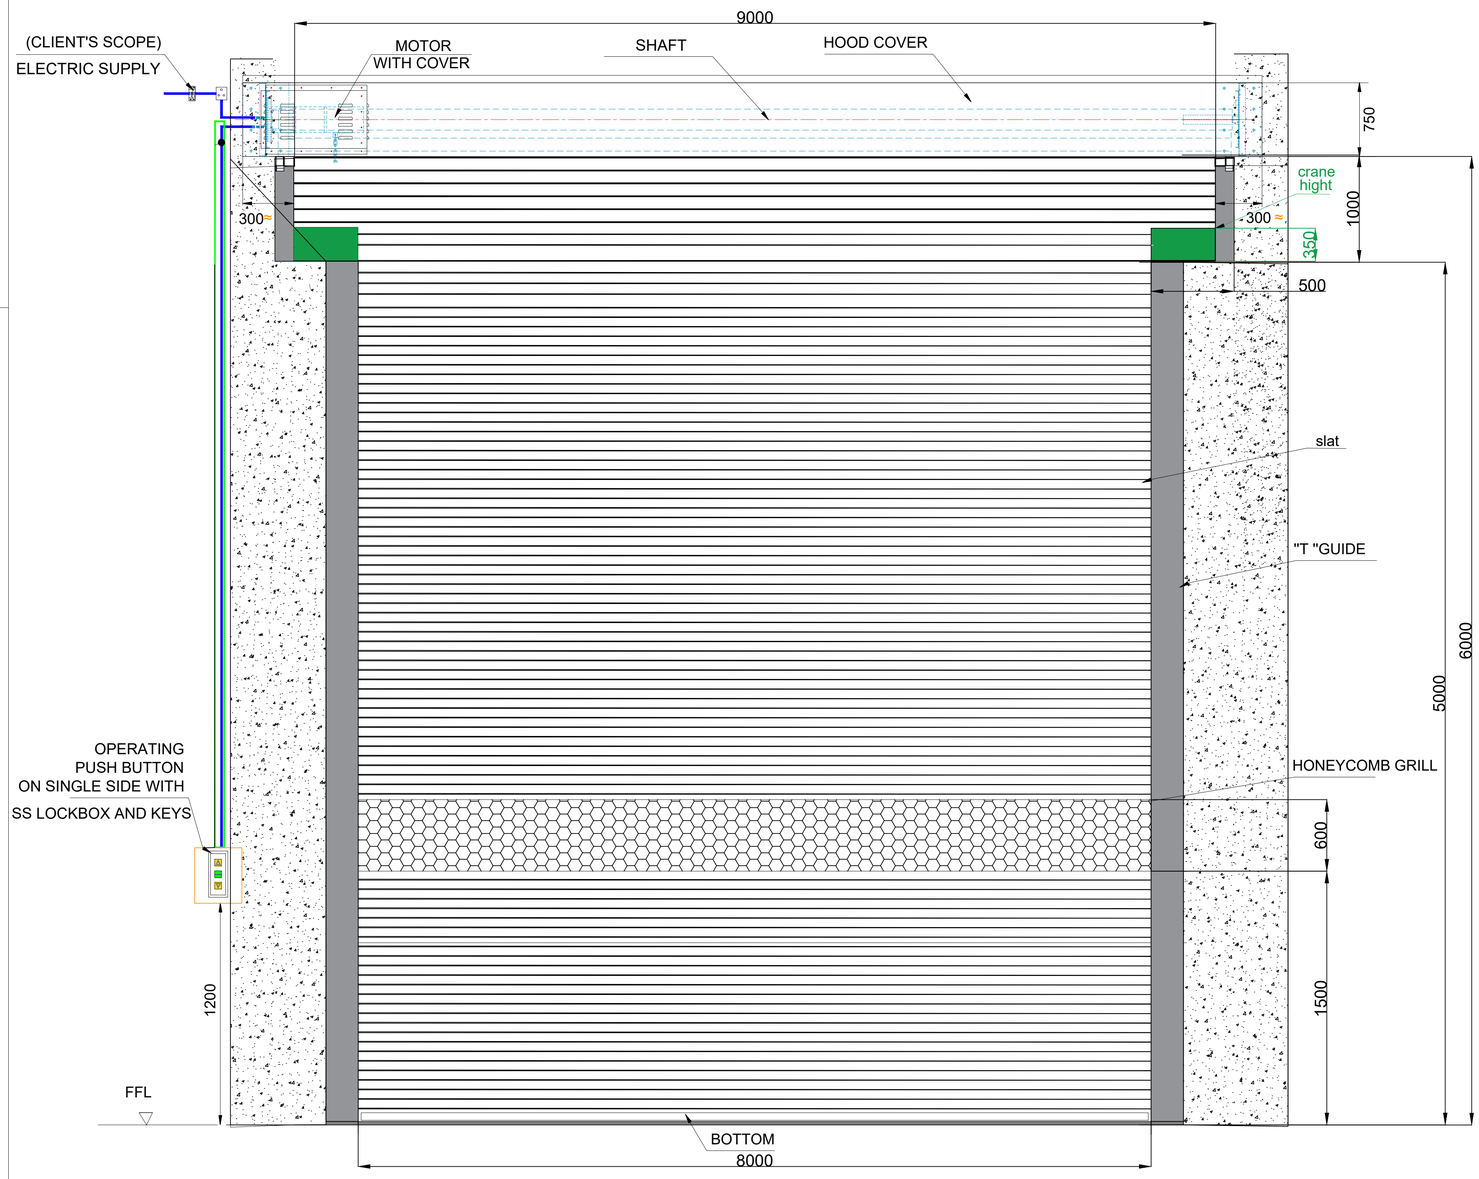


Note:-
1. All Dimensions are in mm
2. shutter mounting position is outside.

R01:- CRANE HEIGHT IS NOT MENTION PREVIOUS GA DWG -06-08-2025

R01:- HONEYCOMB GRILL IS NOT MENTION IN PREVIOUS DWG-14-08-2025

This drawing & design is the property of NIHVA TECHNOLOGIES. Not to be sold or copied to any other concern.

TITLE:- CRANE DOOR INPUT DRG.

NIHVA TECHNOLOGIES PVT. LTD.
NIHVA TECHNOLOGIES PVT. LTD. PUNE
Tel : 020 66304033
Email:- info@nihva.com
Website:- www.nihva.com

	NAME	SIGN	DATE
DRAWN	B.S.		29-07-2025
CHECK & APPRD	V.T.		29-07-2025

CLIENT - SAKSHI MEDTECH

PROJECT - CRANE DOOR INPUT DRG.

FORMAT NO - NIHVA-DD-F-03

If any queries contact :

DWG. NO. : NTPL-292-PM | REV- 02

ALL DIMENSION ARE IN mm | SCALE: NTS | WT: | SHEET:

A

4 3 2 1