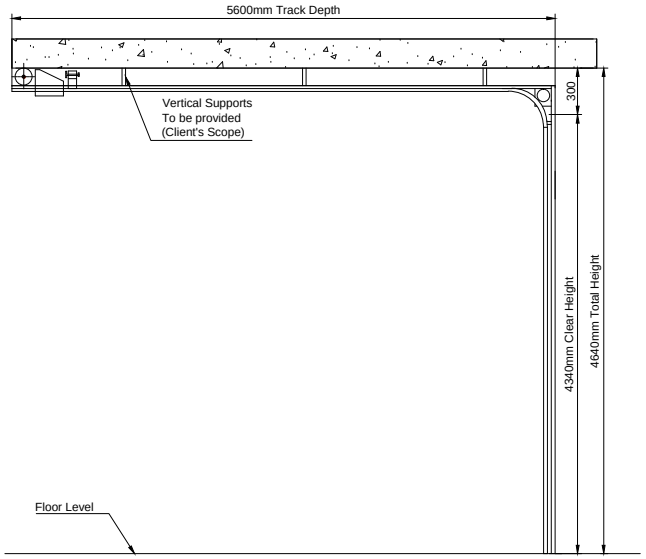

SIDE VIEW

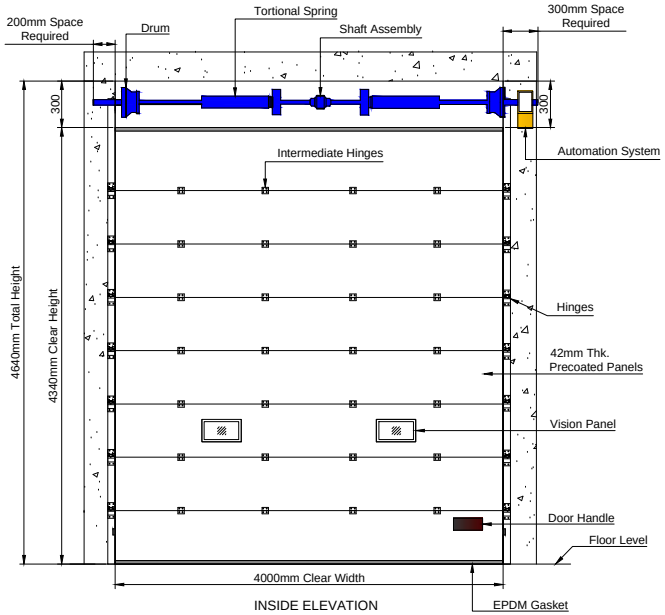

INSIDE ELEVATION

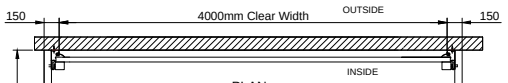

PLAN

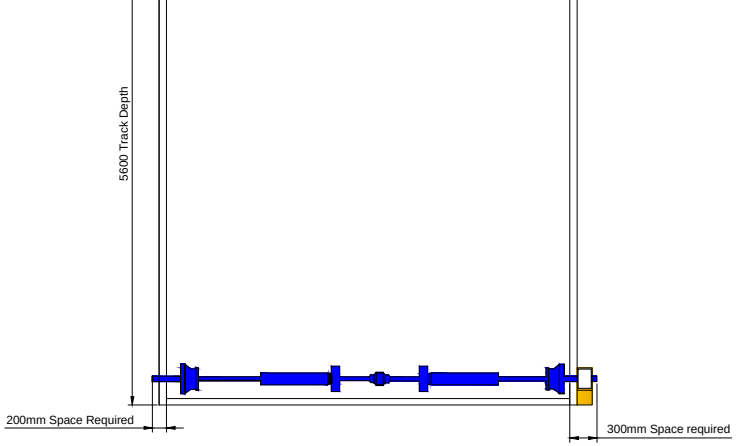

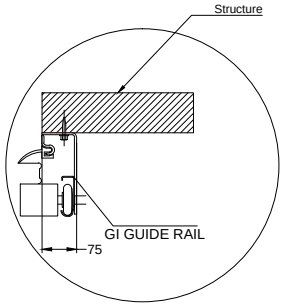

TRACK DETAILS

DIMENSION :

CLEAR WIDTH	CLEAR HEIGHT	QUANTITY
4000 mm	4340 mm	5

TECHNICAL DATA :

COMPONENTS	MATERIALS	SPECIFICATIONS
DOOR PANELS	GI & PUF	42mm CFC- FREE POLYURETHANE WITH 0.5mm THK, GI PRECOATED PANELS.
DOOR HINGE	———	HEAVY DUTY HINGES FOR INTERLOCKING OF PANELS
SHAFT ASSEMBLY	STD.	TORSIONAL SPRING WITH SHAFT & BEARING PLATES
FINISH		ENAMEL PAINT WITH APPROVED SHADE

ACCESSORIES-
1. SAFETY PHOTOCELL- 1 PAIR /DOOR

IMPORTANT NOTES:

1. REQUIRED STRUCTURE FOR DOOR SHALL BE IN CLIENT'S SCOPE.
2.SINGLE PHASE POWER SUPPLY REQUIRED AT DOOR LOCATION.
3.ALL CIVIL WORK SHALL BE CLIENT'S SCOPE.

NIHVA TECHNOLOGIES PVT. LTD. PUNE
Email:- info@nihva.com
Website:- www.nihva.com

TITLE:

SECTIONAL DOOR LL (MOTORIZED)

CLIENT'S APPROVAL :

CLIENT - MAVIN ARCHITECTURAL SOLUTIONS PVT. LTD.

PROJECT - CHENNAI TRADE CENTRE

SITE LOCATION - CHENNAI

DWG. NO. : NIHVA/17-18/0334 | REV- 0

SCALE: NTS | WT: | SHEET:1 OF 1

DRAWN BY: OMKAR | DATE: 12-01-2018

CHECK BY: SHEKHAR | DATE: 12-01-2018

APPROVED BY : SHEKHAR | DATE: 12-01-2018

If any queries contact : design@nihva.com

NOTE: ALL DIMENSIONS ARE IN mm

THIS DRAWING & DESIGNING IS THE PROPERTY OF NIHVA TECHNOLOGIES. NOT TO BE SOLD OR COPIED TO ANY OTHER CONCERN.