
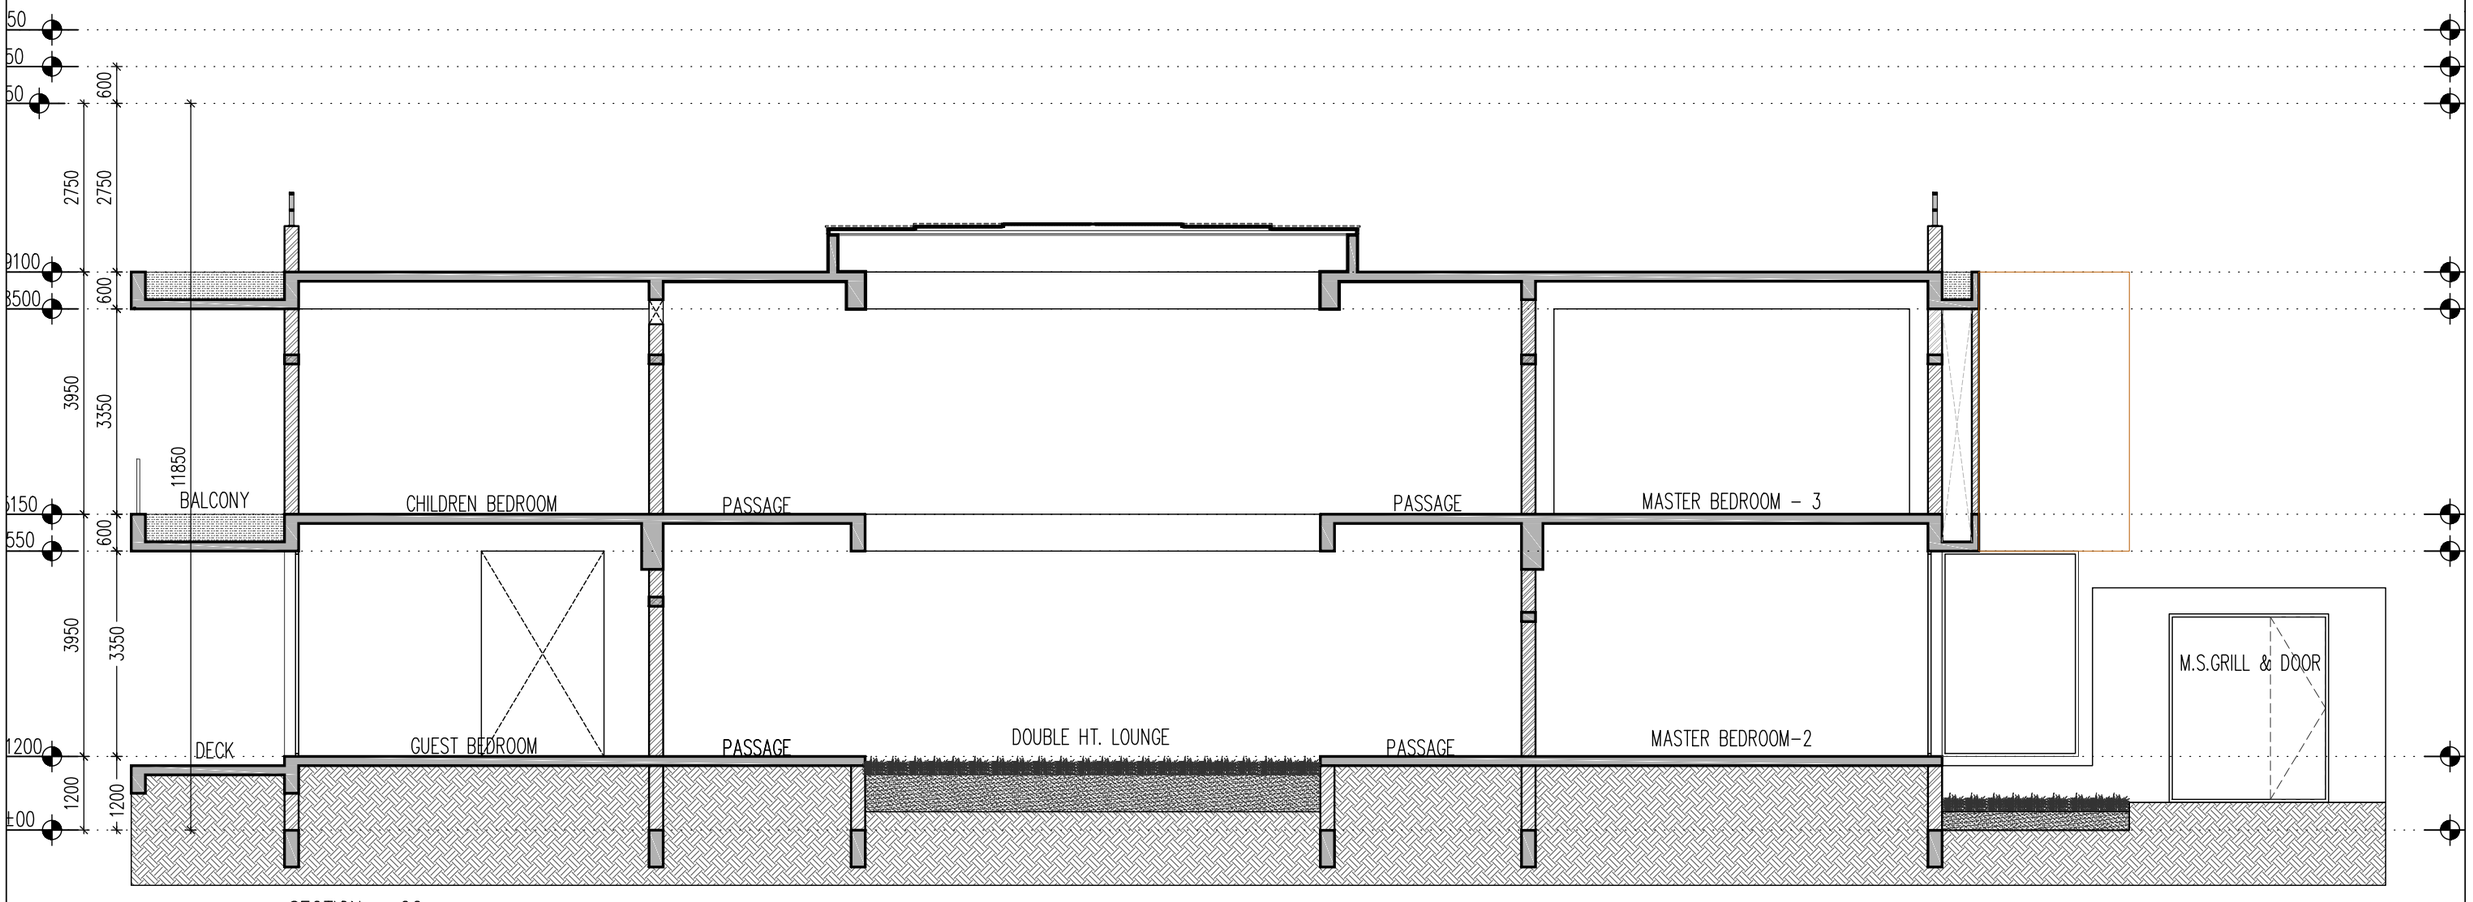


SECTION – CC

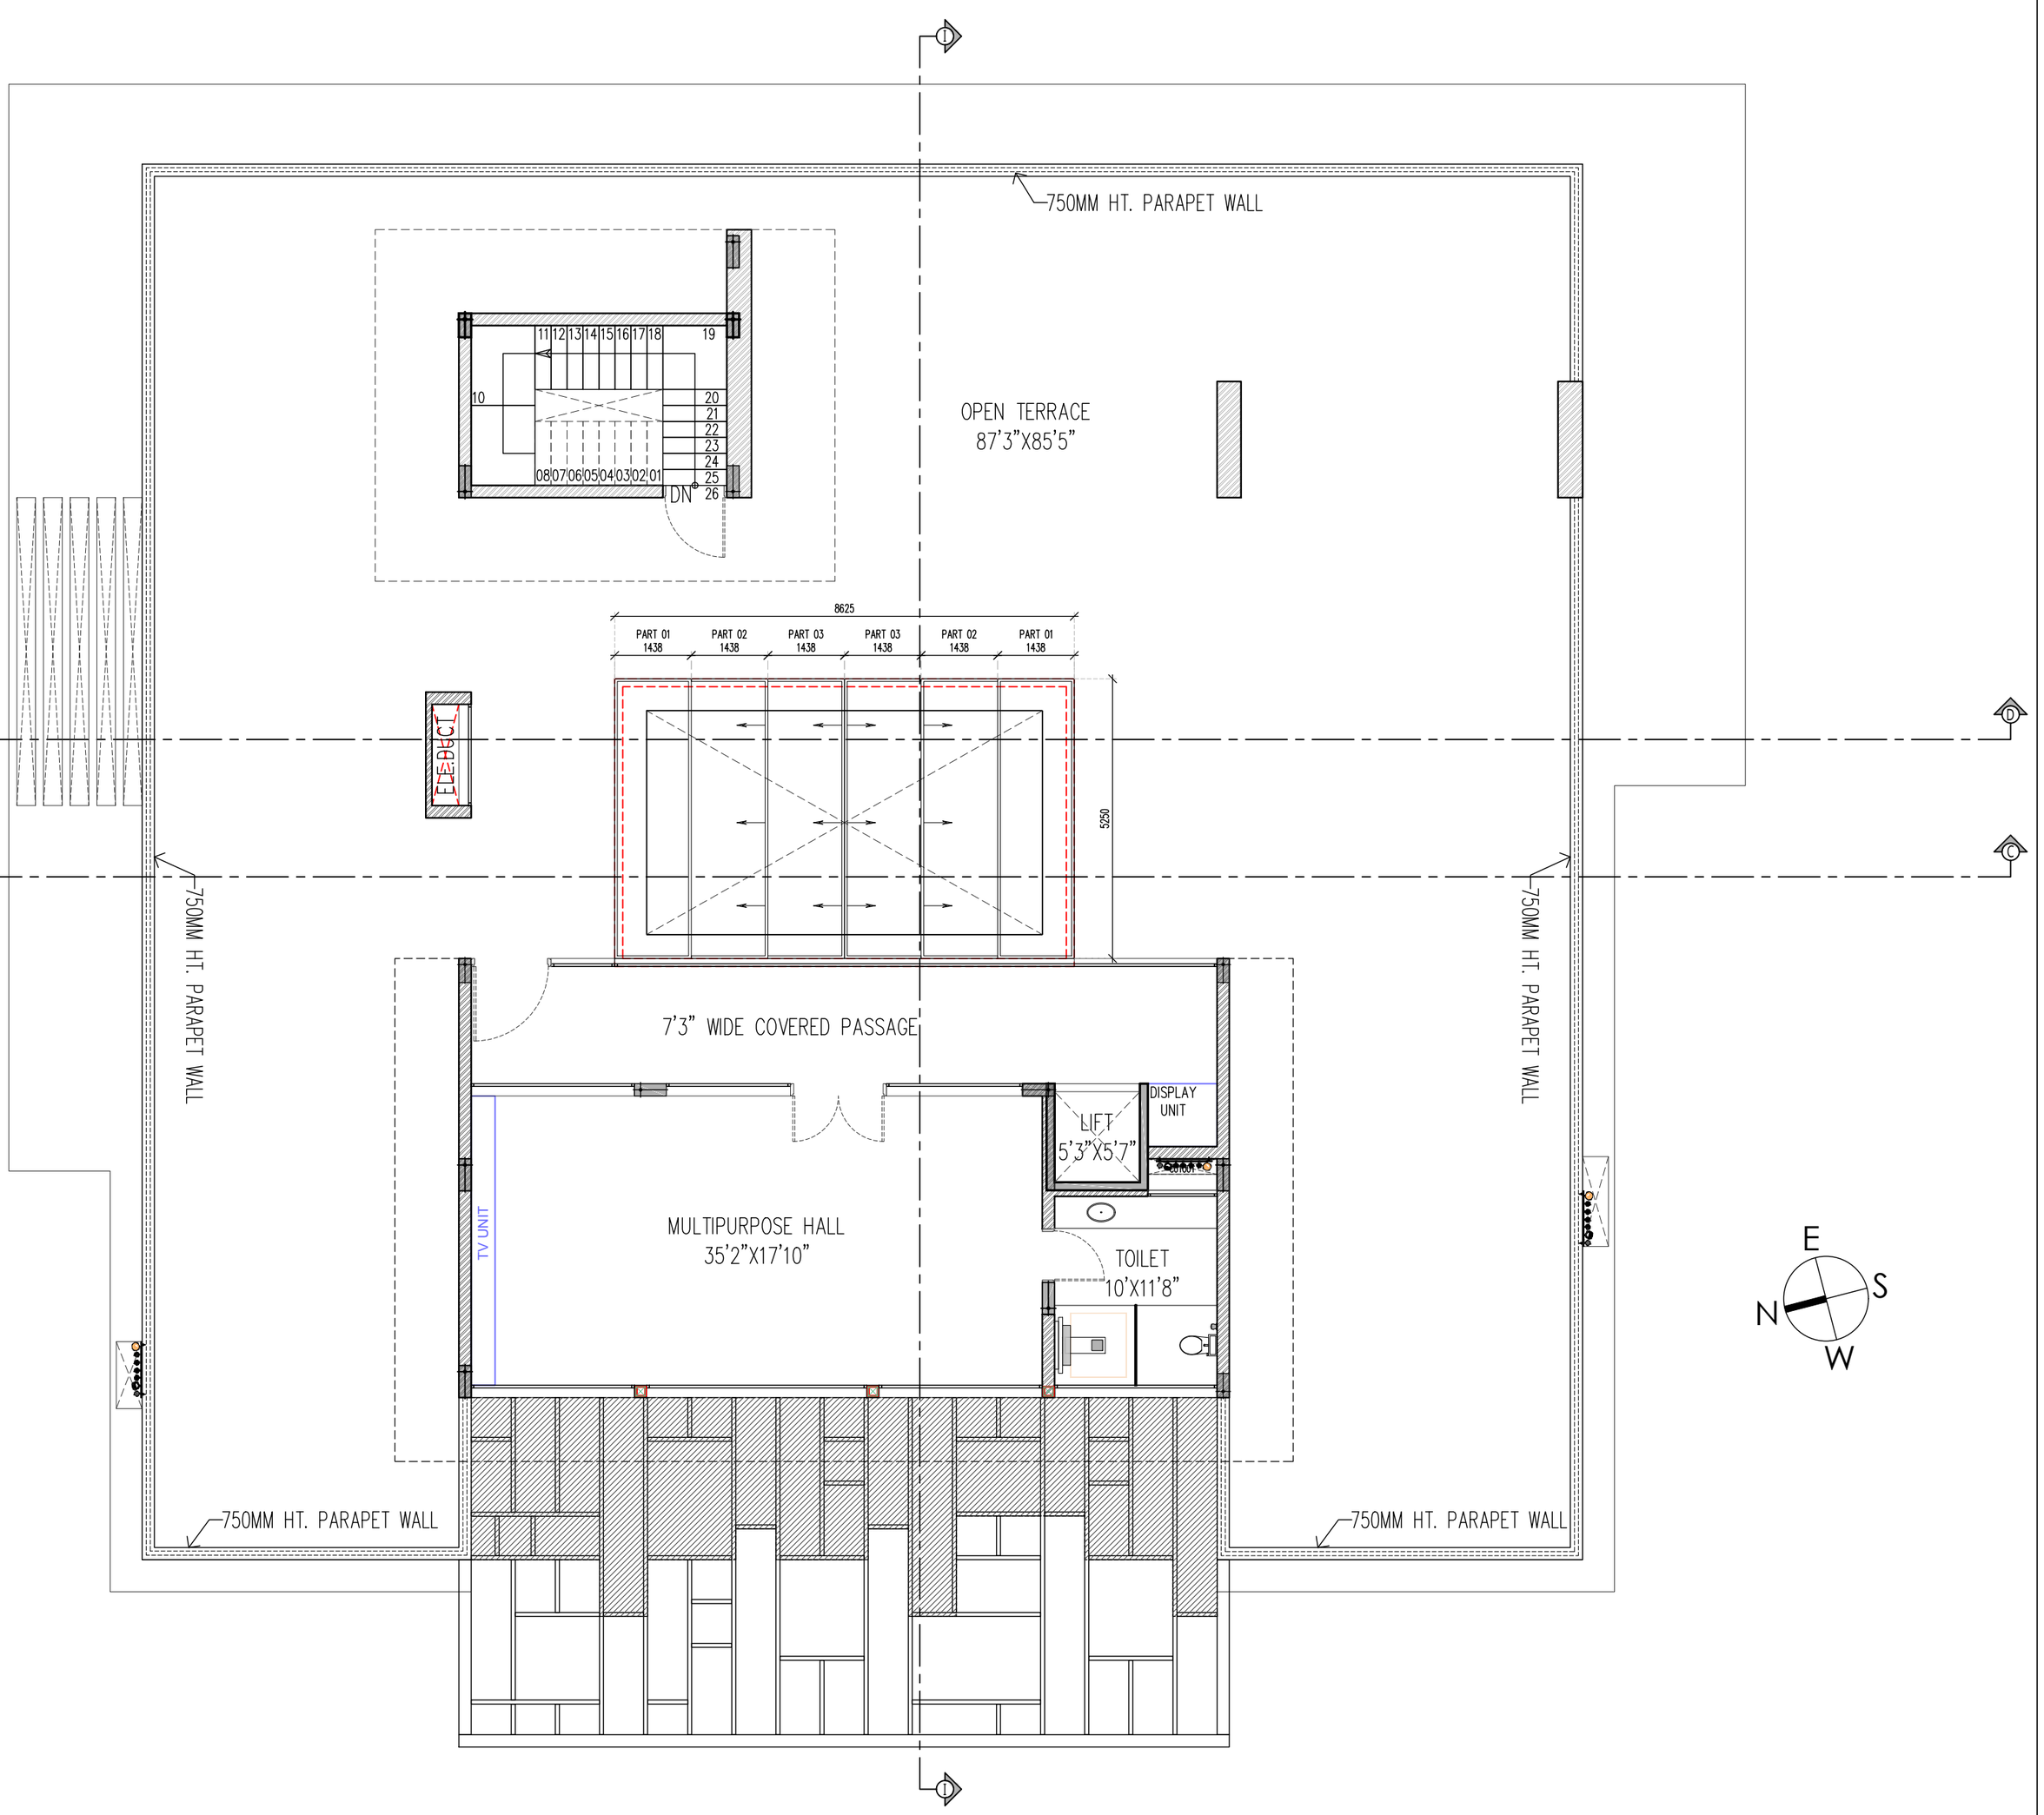

morphallaxis
architecture + design

architect : abhishek panchal
website : www.morphallaxis.in

email : morphallaxis@outlook.com
phone no : +91 84 6040 6000

NOTES/LEGENDS

- All dimensions are in Millimeters and to be read and not measured.
- All dimensions are considered without plaster thickness.
- 25 mm thick plaster on both sides of the brickwork is considered.
- Refer detail drawings wherever relevant.
- In case of any discrepancy between architectural drawings and other drawings, architectural drawings to be followed. The discrepancy to be brought to the notice of the architect before commencement of the work.
- This drawing and the design it covers is the property of **morphallaxis, Ahmedabad, India.** It is merely loaned on the borrower's express agreement that it will not be reproduced, copied, loaned, exhibited nor used except in a limited way and private use as permitted by any written consent given by the lender to the borrower.

KEY PLAN

REVISION OF DRAWING

R.NO	DATE	REMARKS
--	--/--/--	--
--	--/--/--	--
--	--/--/--	--
--	--/--/--	--
--	--/--/--	--
--	--/--/--	--
--	--/--/--	--

HARD COPY

CLIENT	SITE	TOTAL
--	--	--
--	--	--
--	--	--
--	--	--
--	--	--
--	--	--
01	01	02

PROJ. NAME : R 3 B U N G A L O W S
C L I E N T : MAHESHBHAI BUNGALOW

DRG. NAME : S E C O N D F L O O R P L A N
DRG. TYPE : W O R K I N G D R A W I N G

DRAWING FOR : STUDY PURPOSE
MODIFIED BY : D . B . R a v a l **CHECKED BY :** AR.ABHISHEK

PROJ. NO : MB/018

DRG NO : AR_WD_FP_03

REV NO : R1

SCALE - 1 : 1 0 0

24/09/2021