

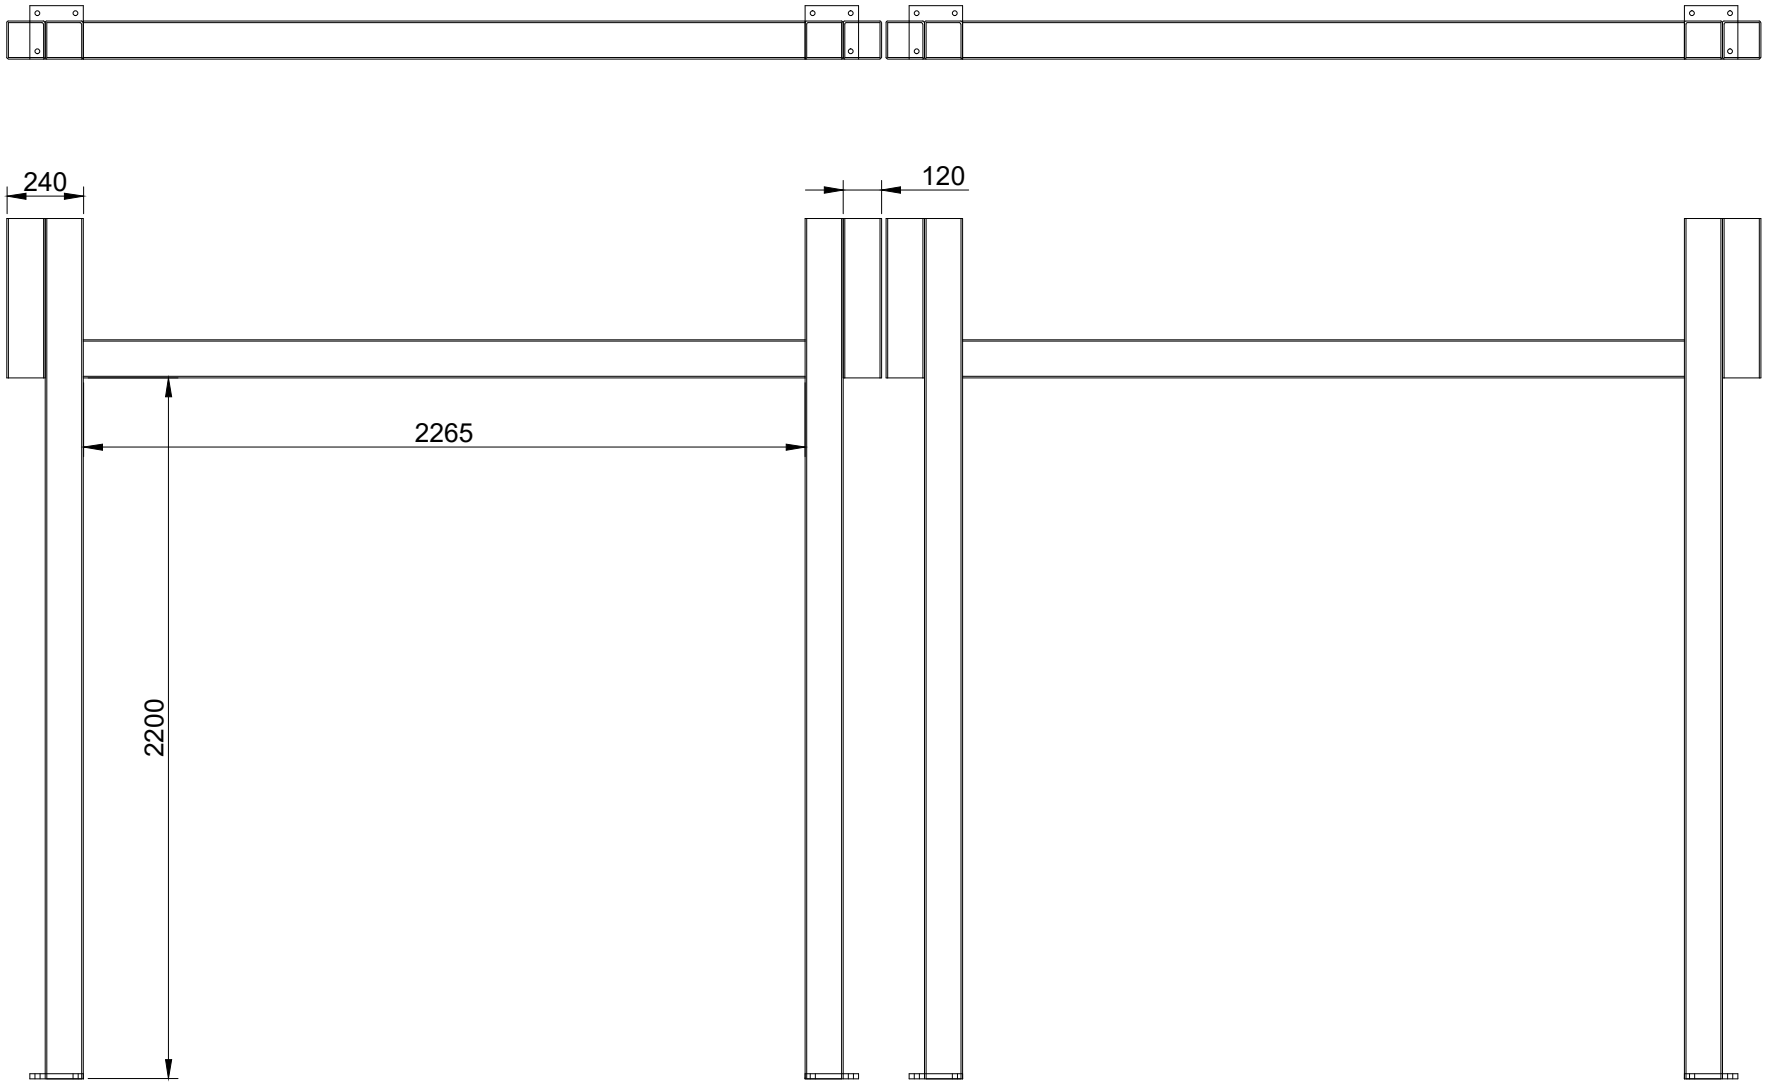


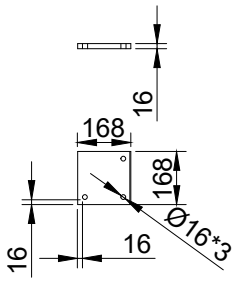

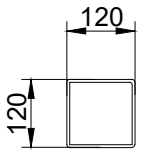

Note:-

1.All dimension are in 'mm'

2.All civil work is in client scope

3.Given GA drawing is only for the client unerstanding purpose

4.If strucuture required, will be in our scope(Box 121*120*5)

Rev No.	Revision	Date	Revised By
01	structure changed from chanel 125*65 to box 120*120*5	01-11-2023	Revised By

This drawing & design is the property of NIHVA TECHNOLOGIES. Not to be sold or copied to any other concern.

TITLE:-MACHINE PROTECTION DOOR STRUCTURE

NIHVA TECHNOLOGIES PVT. LTD.

NIHVA TECHNOLOGIES PVT. LTD. PUNE
Email:- info@nihva.com
Website:- www.nihva.com

	NAME	DATE	SIGN
DRAWN	NIRMALA	01/11/2023	
CHECK	A.K.	01/11/2023	
APPRD.	V.T.	01/11/2023	

If any queries contact : design@nihva.com

ALL DIMENSION ARE IN mm

CLIENT - HIROTEC

LOCATION -

PRODUCT - Machine Protection Door

DWG NO:-NIHVA/23-24/CLT/084

SCALE: NTS

SCALE:-- NTS