
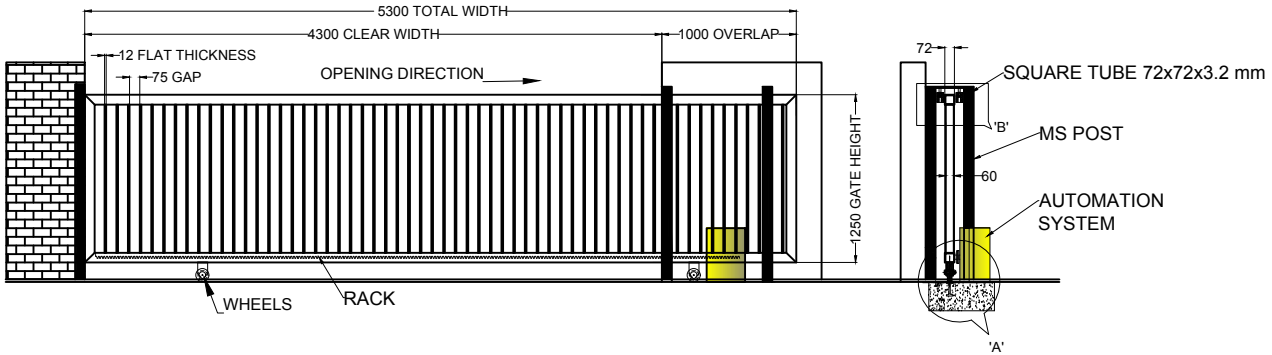
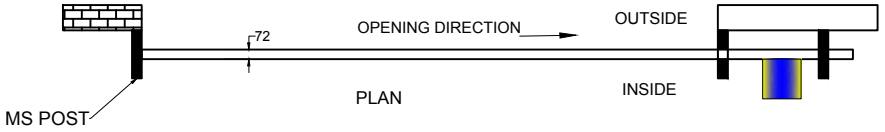
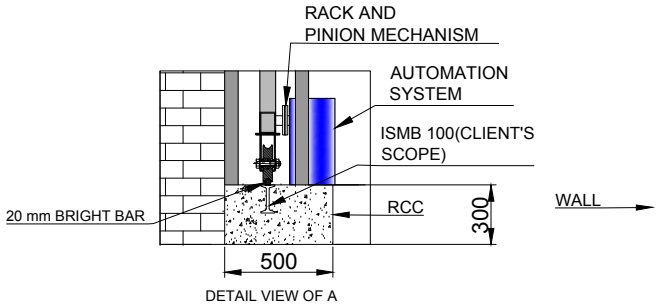



DETAIL VIEW OF A

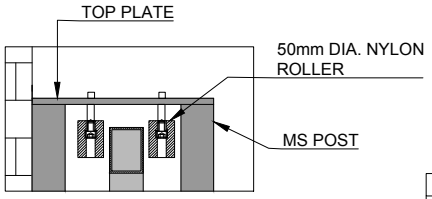


DETAIL VIEW OF B

QTY : 1 NOS

NOTE-
1. ALL REQUIRED CIVIL WORK WILL BE IN CLIENTS SCOPE.
2. TWO COATS OF PRIMER AND TWO COATS OF SYNTHETIC ENAMEL PAINT OF APPROVE SHADE.
3. SAFETY ACCESSORIES : FLASHING LIGHT, SAFETY PHOTOCELL.
4. GATE LEAF WILL BE IN TWO PARTS FOR TRANSPORTATION & WILL BE WELD TOGETHER ON SITE.

TOLERANCE- ±10mm

This drawing & design is the property of NIHVA TECHNOLOGIES. Not to be sold or copied to any other concern.

| TITLE | AUTOMATIC SLIDING GATE | | | NIHVA TECHNOLOGIES PVT. LTD. PUNE<br>Tel : 020 66304033<br>Email:- info@nihva.com<br>Website:- www.nihva.com | |
|---|---|---|---|---|---|
| | NAME | SIGN | DATE | | |
| DRAWN | S.M.S. | | 25.02.2020 | CLIENT - DYNAMIC LOGISTICS | |
| CHECK | P.A. | | 25.02.2020 | PROJECT - ELLESLEY | |
| APPRD. | | | | SITE LOCATION - PUNE | |
| If any queries contact : design@nihva.com | | | | DWG. NO. : NIHVA/19-20/0218 | REV- R00 |
| ALL DIMENSION ARE IN mm | | | | SCALE: NTS | WT: SHEET: |