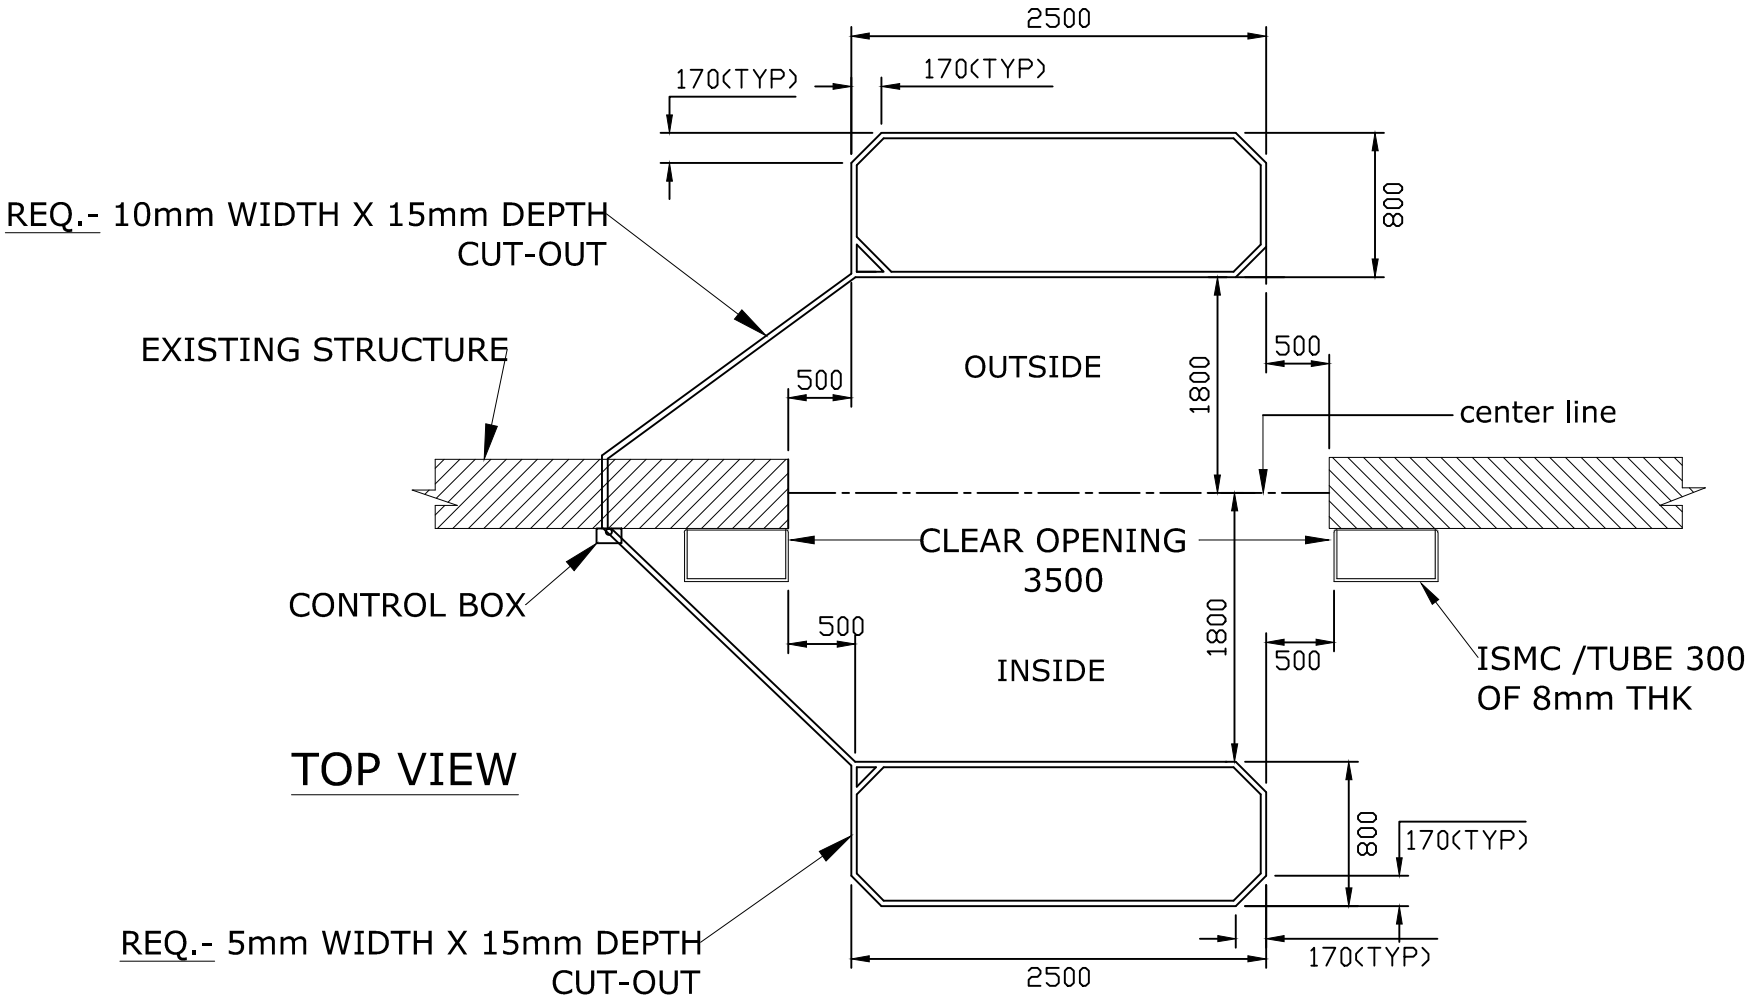


CLEAR WIDTH (CW)	CLEAR HEIGHT (CH)	QUANTITY
3500	3500	6
3500	4500	6

This drawing & designing is the property of NIHVA TECHNOLOGIES. Not be sold or copy to any other concern.

TITLE

FLOOR CUT-OUT FOR LOOP DETECTOR FOR HIGH SPEED DOOR (RR3000)

CLIENT APPROVAL

ALL DIMENSION ARE IN mm

	SIGN	DATE
DRAWN	OMKAR	13/06/16
CHECK	ANIL	13/06/16
ENG		
APPRD.		
MFG		
Ref. No.		

NIHVA TECHNOLOGIES PVT. LTD.

NIHVA TECHNOLOGY PVT. LTD. PUNE
Tel : 020 66304033
Email:- info@nihva.com
Website:- www.nihva.com

CLIENT - KNIGHT FRANK/MBIL

PROJECT- MBIL

SITE -

DWG. NO. - NIHVA/15-16/246

SCALE: 01 | WT: | SHEET: 01

If any queries contact : projects@nihva.com