





DETAIL D
SCALE 1 : 15

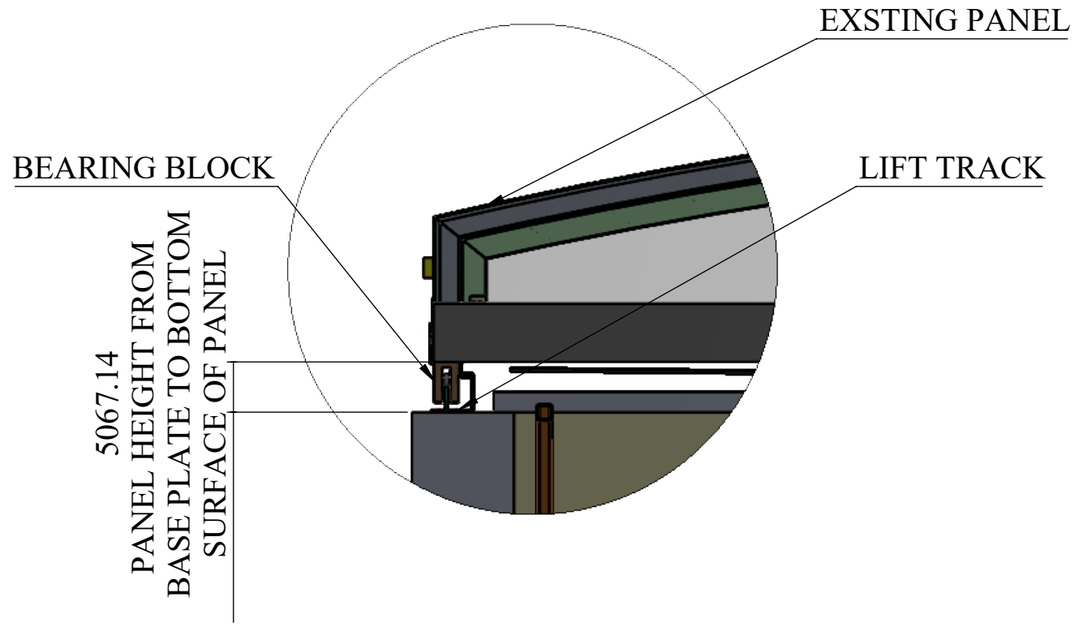



DETAIL C
SCALE 1 : 15

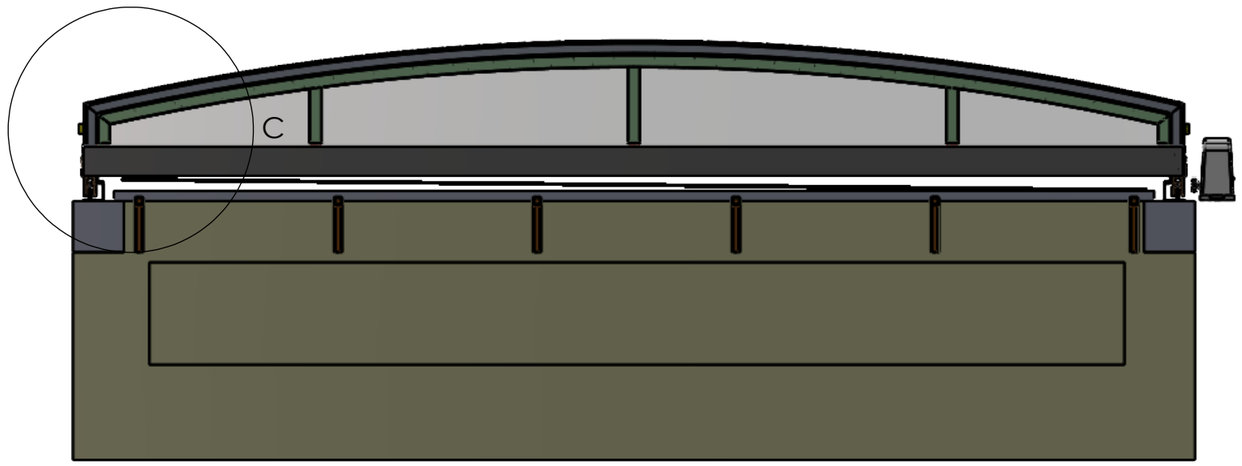

TITLE - ROOF AUTOMATION				NIHVA TECHNOLOGIES PVT.LTD.PUNE	
DWG NO - NTPL-163-PM-001-00-00-00				Website - www.nihva.com	
	NAME	SIGNATURE	DATE	PROJECT NO - NTPL-163-PM	
DRAWN	V.B.		25-06-2025	PRODUCT - RETRACTABLE ROOF	REVISION -
CHK'D	S.W.		25-06-2025	SITE LOCATION - WAKAD	WEIGHT -
APPV'D	V.T.		25-06-2025	MATRIAL -	QTY - 1
if any queries contact - supportautomation@nihva.com				PROJECTION METHOD:	SCALE :
ALL DIMENSION ARE IN mm			A3		SHEET 1 OF 9

ITEM NO.	PART NUMBER	DESCRIPTION	QTY.
1	GUIDE RAILS-T75-1B	STD (5 M LENGTH)	2

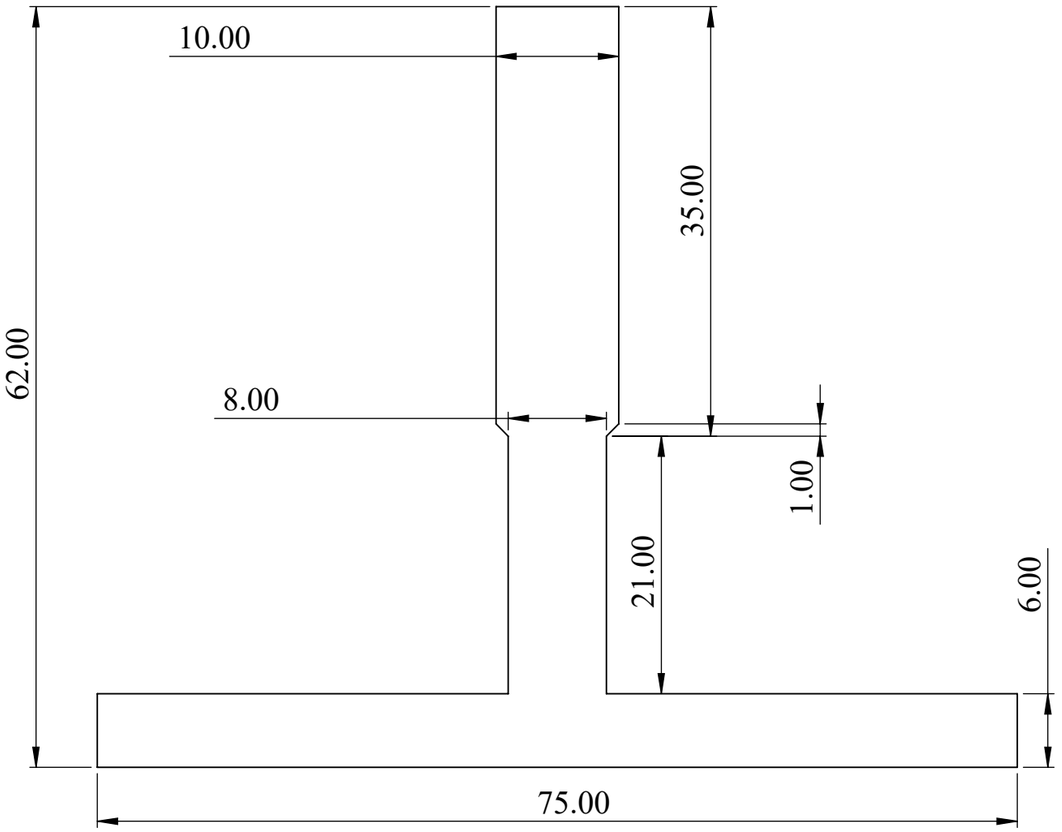


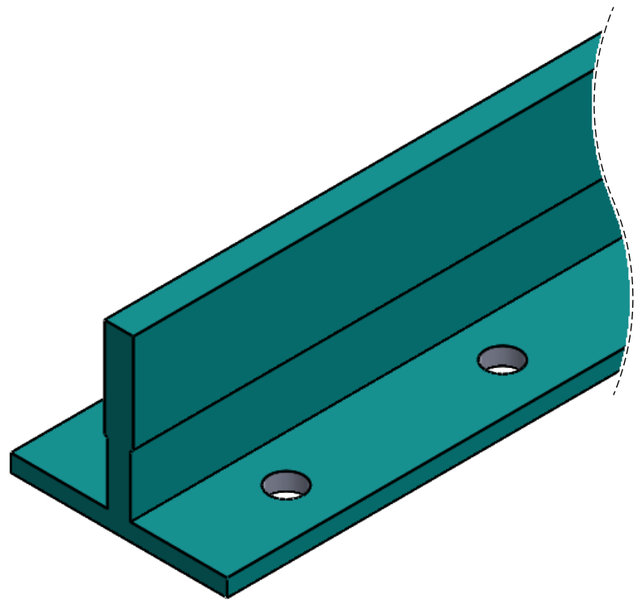


NOTE
GUIDE RAIL T-75 1B STD
TOTAL LENGTH- 9800MM (TRACK LENGTH)
QTY- 2 NOS

TITLE - ROOF AUTOMATION				NIHVA TECHNOLOGIES PVT.LTD.PUNE	
DWG NO - NTPL-163-PM-001-00-00-00				Website - www.nihva.com	
	NAME	SIGNATURE	DATE	PROJECT NO - NTPL-163-PM	
DRAWN	V.B.		25-06-2025	PRODUCT - RETRACTABLE ROOF	REVISION -
CHK'D	S.W.		25-06-2025	SITE LOCATION -WAKAD	WEIGHT -
APPV'D	V.T.		25-06-2025	MATRIAL -	QTY - 1
if any queries contact - supportautomation@nihva.com				PROJECTION METHOD:	SCALE :
ALL DIMENSION ARE IN mm			A3		SHEET 2 OF 9

ITEM NO.	PART NUMBER	DESCRIPTION	QTY.
1	GUIDE RAILS-T75-1B	CUT PART - 4800MM	2

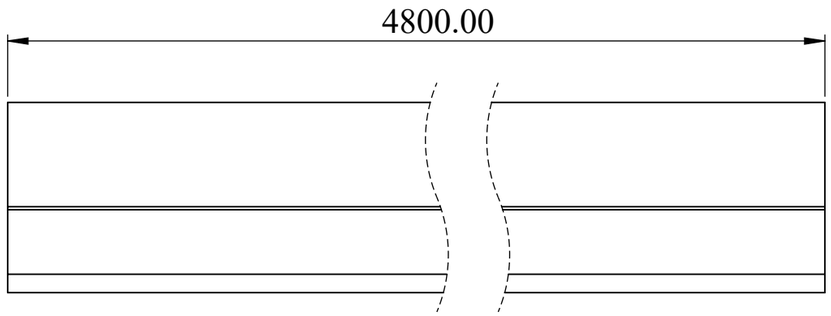


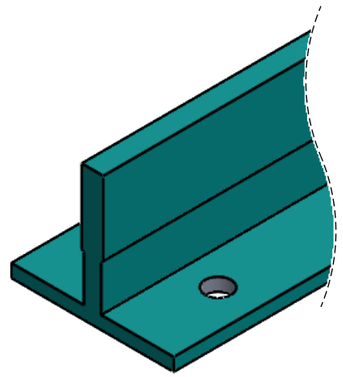



NOTE
GUIDE RAIL T-75 1B STD
CUT PART LENGTH- 4800MM (TRACK LENGTH)
QTY- 2 NOS

TITLE - ROOF AUTOMATION				NIHVA TECHNOLOGIES PVT.LTD.PUNE Website - www.nihva.com	
DWG NO - NTPL-163-PM-001-00-00-00					
	NAME	SIGNATURE	DATE	PROJECT NO - NTPL-163-PM	
DRAWN	V.B.		25-06-2025	PRODUCT - RETRACTABLE ROOF	REVISION -
CHK'D	S.W.		25-06-2025	SITE LOCATION -WAKAD	WEIGHT -
APPV'D	V.T.		25-06-2025	MATRIAL -	QTY - 1
if any queries contact - supportautomation@nihva.com				PROJECTION METHOD:	SCALE :
ALL DIMENSION ARE IN mm			A3		SHEET 3 OF 9

ITEM NO.	PART NUMBER	DESCRIPTION	QTY.
1	ROLLER BRG HSG	100X80X105 MM (VMC PART)	4
2	SKF_NATR 12	BRG(STD)	8
3	SHOULDER BOLT NATR 12		8
4	SKF_NATR 8	BRG(STD)	8
5	ISO 7379 - 8 x 30 --- N		8

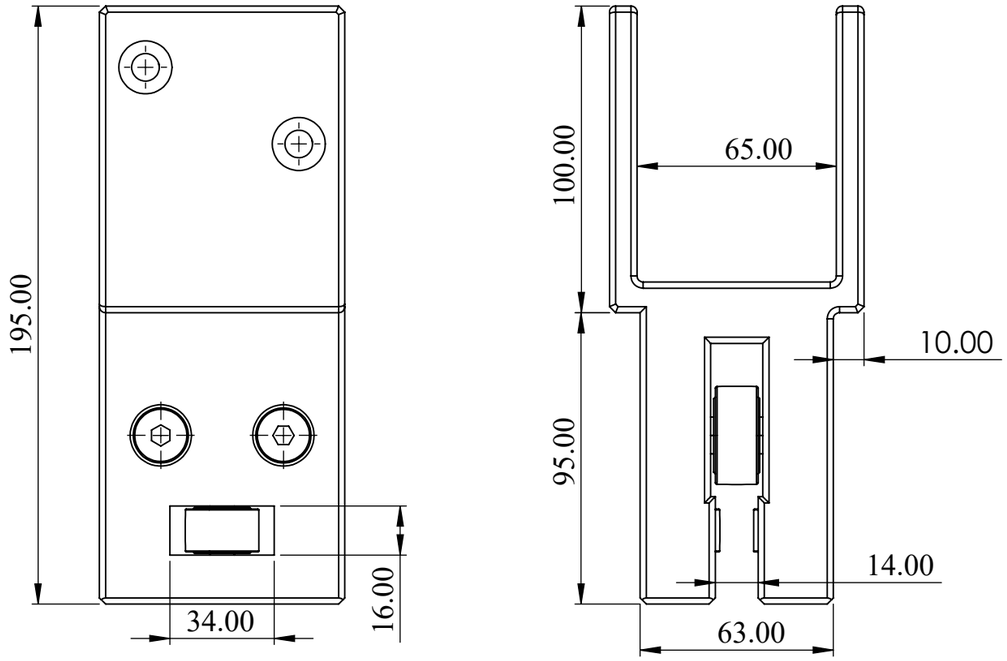

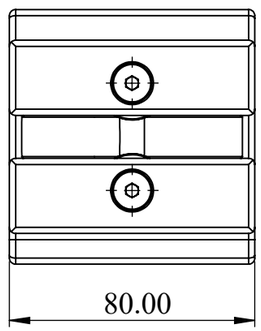


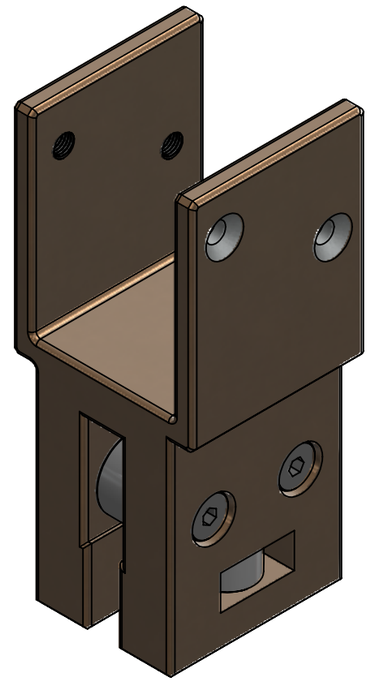



NOTE
BEARING BLOCK ASM
USE THIS BEARING BLOCK ASM
FOR ALL PANEL
VMC CUTTING


TITLE - ROOF AUTOMATIOM				NIHVA TECHNOLOGIES PVT.LTD.PUNE
DWG NO - NTPL-163-PM-001-00-00-00				Website - www.nihva.com
	NAME	SIGNATURE	DATE	PROJECT NO - NTPL-163-PM
DRAWN	V.B.		25-06-2025	PRODUCT - RETRACTABLE ROOF
CHK'D	S.W.		25-06-2025	SITE LOCATION - WAKAD
APPV'D	V.T.		25-06-2025	
if any queries contact - supportautomation@nihva.com				REVISION - / QTY - 1
ALL DIMENSION ARE IN mm		A3		SCALE / SHEET 4 OF 9

ITEM NO.	PART NUMBER	DESCRIPTION	QTY.
1	ROLLER BRG HSG	100X80X105 MM (VMC PART)	4

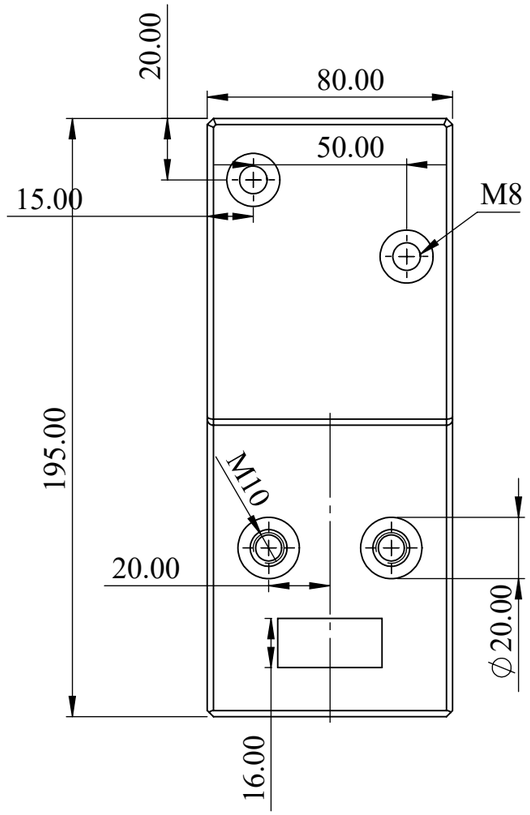

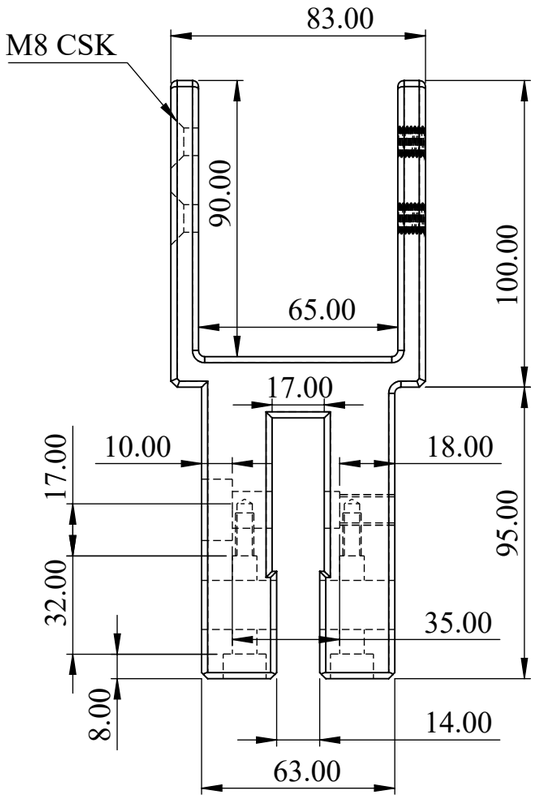


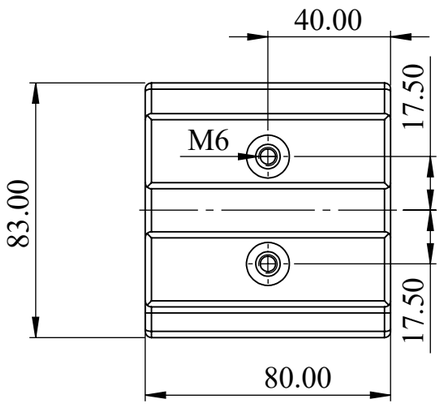


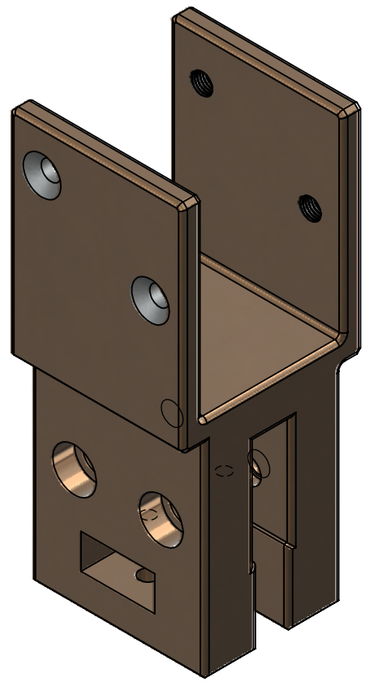


NOTE
BEARING BLOCK
USE THIS BEARING BLOCK
FOR ALL PANEL
VMC CUTTING
MATERIAL - ALUMINIUM
THICKNESS - 9 MM
QTY -4 NOS


TITLE - ROOF AUTOMATIOM				NIHVA TECHNOLOGIES PVT.LTD.PUNE
DWG NO - NTPL-163-PM-001-00-00-00				Website - www.nihva.com
	NAME	SIGNATURE	DATE	PROJECT NO - NTPL-163-PM
DRAWN	V.B.		25-06-2025	PRODUCT - RETRACTABLE ROOF
CHK'D	S.W.		25-06-2025	SITE LOCATION -WAKAD
APPV'D	V.T.		25-06-2025	
if any queries contact - supportautomation@nihva.com				REVISION - / QTY - 1
ALL DIMENSION ARE IN mm		A3		SCALE / SHEET 5 OF 9

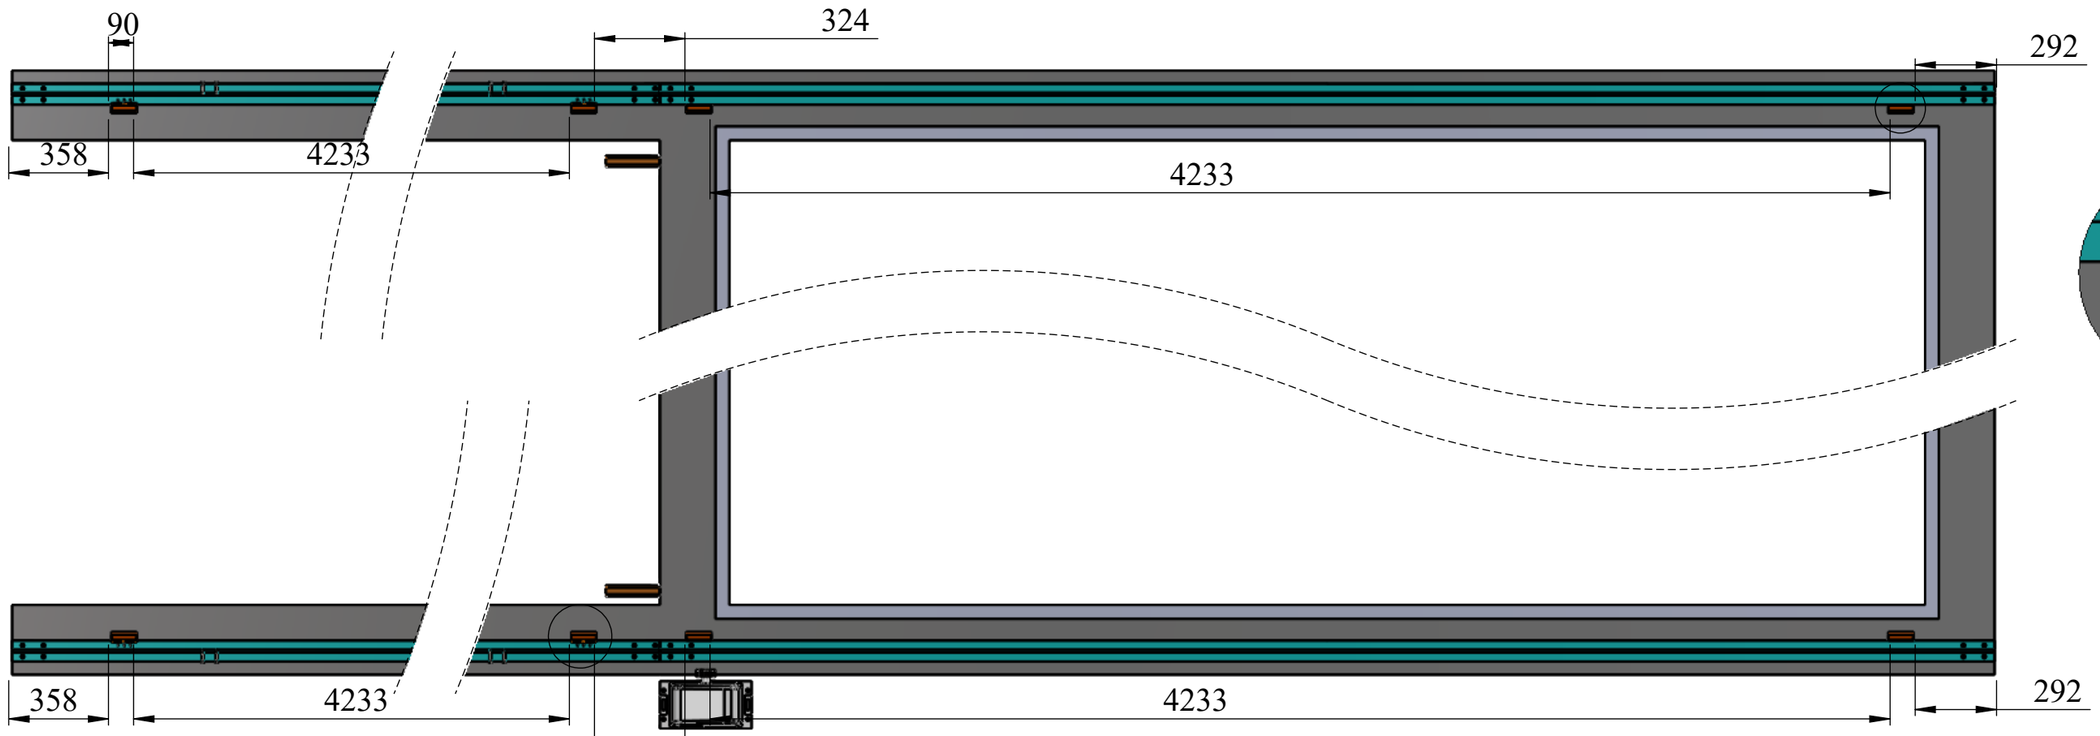

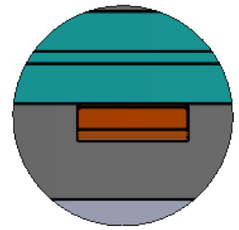


DETAIL E
SCALE 1 : 5

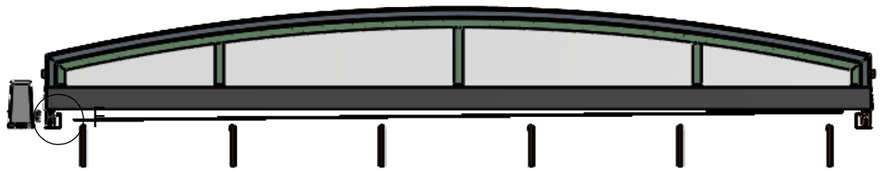

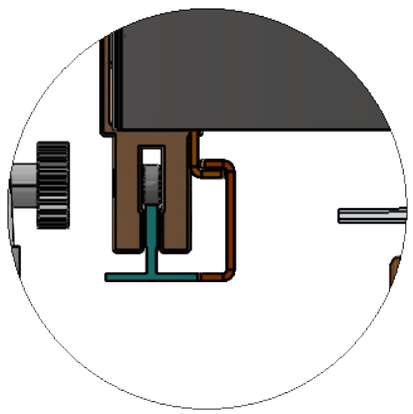


DETAIL F
SCALE 1 : 5

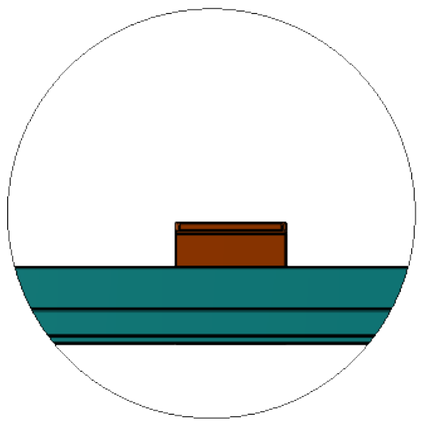

DETAIL G
SCALE 1 : 5

H

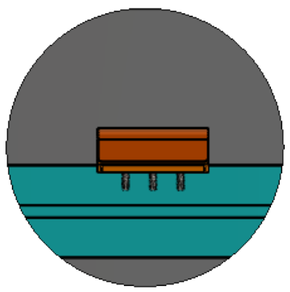



DETAIL H
SCALE 1 : 5

NOTE-
1) LOCKING PLATE ASM
LOCKING PLATE POSITION
2) LOCKING PLATE MOUNT ON IN SIDE OF THE PANEL

TITLE - ROOF AUTOMATION				NIHVA Technologies Pvt. Ltd.	NIHVA TECHNOLOGIES PVT.LTD.PUNE Website - www.nihva.com
DWG NO - NTPL-163-PM-001-00-00-00					
	NAME	SIGNATURE	DATE	PROJECT NO - NTPL-000-PM	
DRAWN	V.W		25-06-2025	PRODUCT - RETRACTABLE ROOF	REVISION -
CHK'D	S.W.		25-06-2025	SITE LOCATION -WAKAD	WEIGHT -
APPV'D	V.T.		25-06-2025	MATRIAL -	QTY - 1
if any queries contact - supportautomation@nihva.com				PROJECTION METHOD:	SCALE :
ALL DIMENSION ARE IN mm			A3		SHEET 6 OF 9

ITEM NO.	PART NUMBER	DESCRIPTION	QTY.
1	LOCKING PLATE PLATE 1	90 X37.5X 6MM THK	8

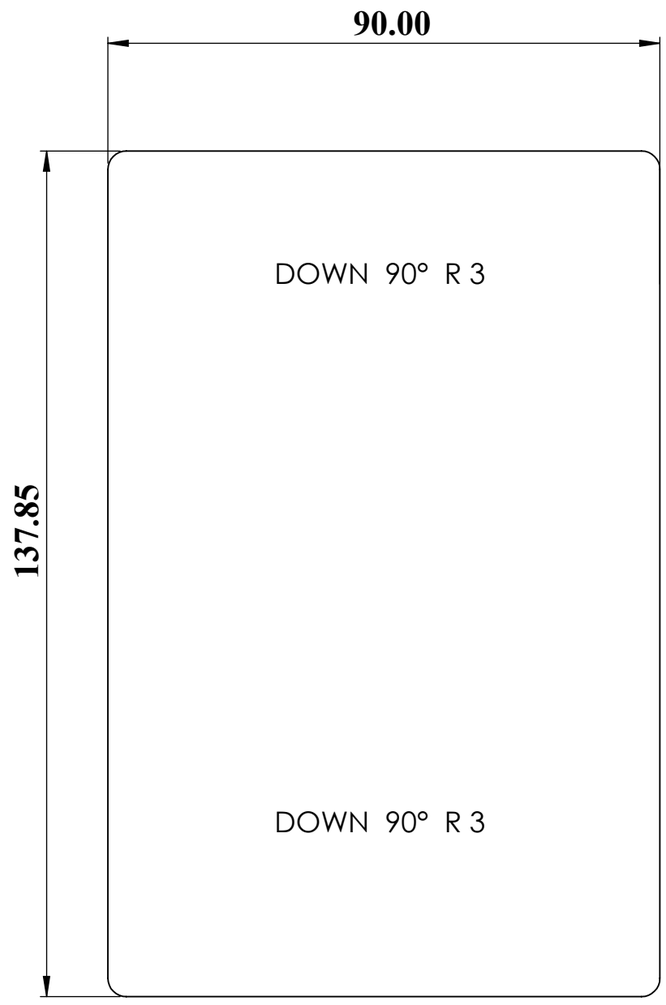


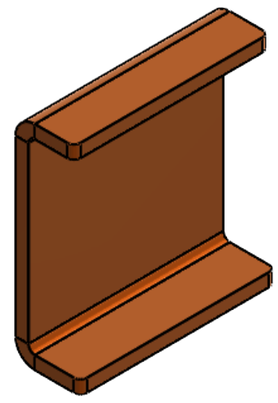


NOTE:-
LOCKING PLATE 1
SIZE- 90X37.5X6 MM THK
MATERIAL- MS
THK- 6MM
QTY- 8 NOS

TITLE - ROOF AUTOMATION				NIHVA TECHNOLOGIES PVT.LTD.PUNE	
DWG NO - NTPL-163-PM-001-00-00-00				Website - www.nihva.com	
	NAME	SIGNATURE	DATE	PROJECT NO - NTPL-163-PM	
DRAWN	V.B.		25-06-2025	PRODUCT - RETRACTABLE ROOF	REVISION -
CHK'D	S.W.		25-06-2025	SITE LOCATION -WAKAD	WEIGHT -
APPV'D	V.T.		25-06-2025	MATRIAL -	QTY - 1
if any queries contact - supportautomation@nihva.com				PROJECTION METHOD:	SCALE :
ALL DIMENSION ARE IN mm			A3		SHEET 7 OF 9

ITEM NO.	PART NUMBER	DESCRIPTION	QTY.
1	LOCKING PLATE 2	113.42 X 90 X 6 MM THK	8

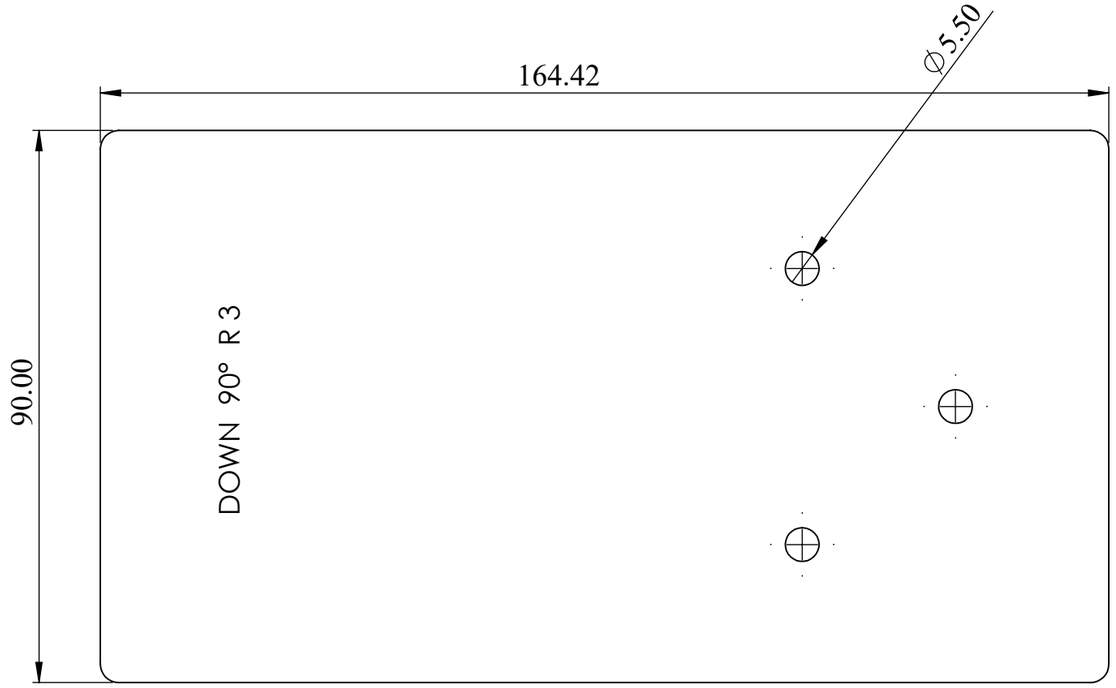

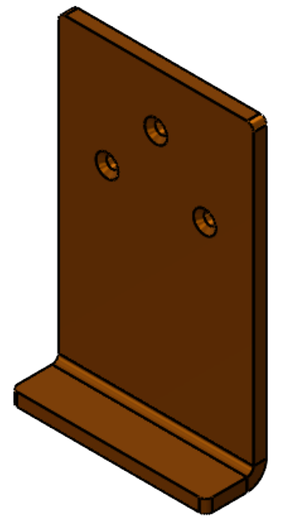



NOTE:-
LOCKING PLATE 2
SIZE- 90X164.5X6 MM THK
MATERIAL- MS
THK- 6MM
QTY- 8 NOS

TITLE - ROOF AUTOMATION				NIHVA TECHNOLOGIES PVT.LTD.PUNE	
DWG NO - NTPL-000-PM-001-00-00-00				Website - www.nihva.com	
	NAME	SIGNATURE	DATE	PROJECT NO - NTPL-000-PM	
DRAWN	V.B.		25-06-2025	PRODUCT - RETRACTABLE ROOF	REVISION -
CHK'D	S.W.		25-06-2025	SITE LOCATION - WAKAD	WEIGHT -
APPV'D	V.T.		25-06-2025	MATRIAL -	QTY - 1
if any queries contact - supportautomation@nihva.com				PROJECTION METHOD:	SCALE :
ALL DIMENSION ARE IN mm			A3		SHEET 8 OF 9

ITEM NO.	PART NUMBER	DESCRIPTION	QTY.
1	M5_Countersunk_20		24

M5 COUNTERSUNK X 20 BOLT

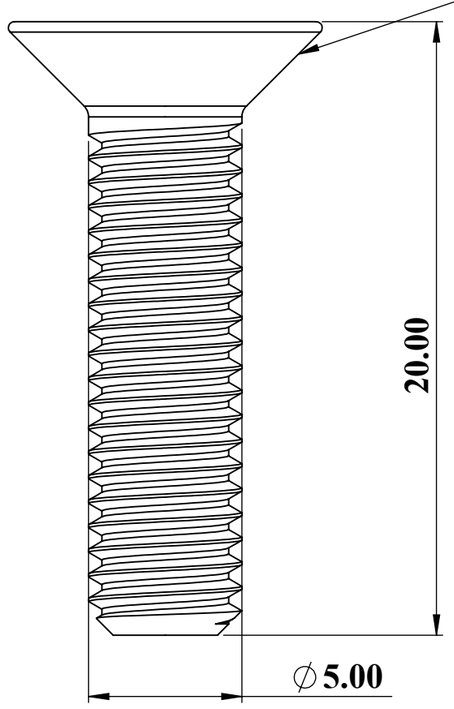

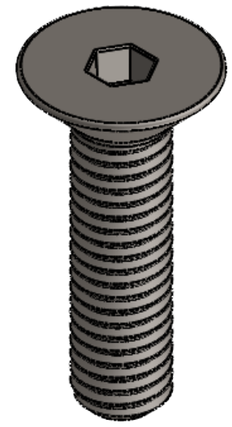

NOTE:-
THIS M5 CSK BOLT FOR LOCKING PLATE FIX TO PANEL .
MATERIAL:- SS
QTY- 24 NOS

TITLE - ROOF AUTOMATION				NIHVA TECHNOLOGIES PVT.LTD.PUNE	
DWG NO - NTPL-163-PM-001-00-00-00				Website - www.nihva.com	
	NAME	SIGNATURE	DATE	PROJECT NO - NTPL-163-PM	
DRAWN	V.W		25-06-2025	PRODUCT - RETRACTABLE ROOF	REVISION -
CHK'D	S.W.		25-06-2025	SITE LOCATION - WAKAD	WEIGHT -
APPV'D	V.T.		25-06-2025	MATRIAL -	QTY - 1
if any queries contact - supportautomation@nihva.com				PROJECTION METHOD:	SCALE :
ALL DIMENSION ARE IN mm			A3		SHEET 9 OF 9