
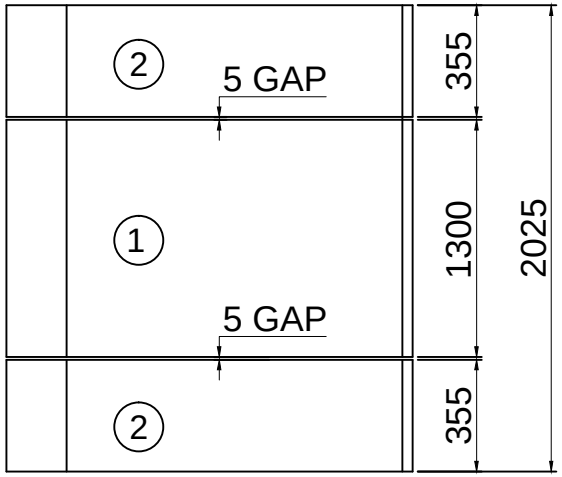


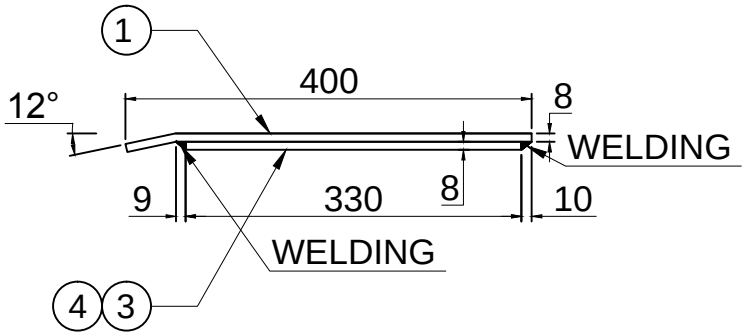

1. CHEQ. SHEET 400 X 8 THK X 1300L = 1 NO
2. CHEQ. SHEET 400 X 8 THK X 355L = 2 NOS
3. CHEQ. SHEET 330 X 8 THK X 1280L = 1 NO
4. CHEQ. SHEET 330 X 8 THK X 345L = 2 NO

REV NO	DRAWN	DATE	DESCRIPTION
R 01	PRADEEP	15.09.18	LIP PLATE DESIGN CHANGE

This drawing & design is the property of NIHVA TECHNOLOGIES. Not to be sold or copied to any other concern.

TITLE

LIP PLATE DRG

	NAME	SIGN	DATE
DRAWN	PRADEEP		05.09.2018
CHECK	PRADEEP		05.09.2018
APPRD.	PRADEEP		05.09.2018

NIHVA TECHNOLOGIES PVT. LTD.

NIHVA TECHNOLOGIES PVT. LTD. PUNE
Tel : 020 66304033
Email:- info@nihva.com
Website:- www.nihva.com

If any queries contact : design@nihva.com

ALL DIMENSION ARE IN mm

CLIENT -

PROJECT - DLSD1010

SITE LOCATION -

DWG. NO. : NIHVA/18-19/MFG/DLSD1010/007/R01

SCALE: NTS | WT: | REV- 01