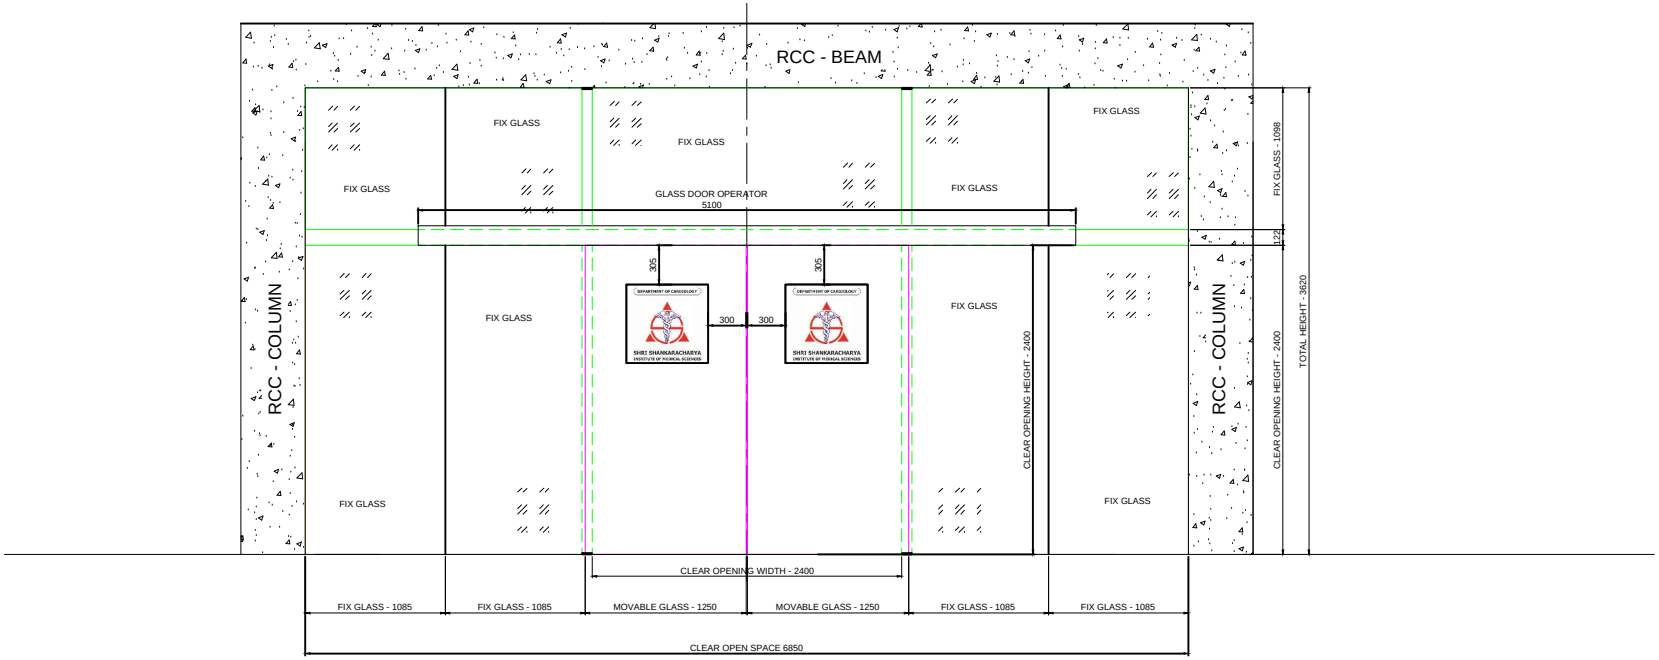

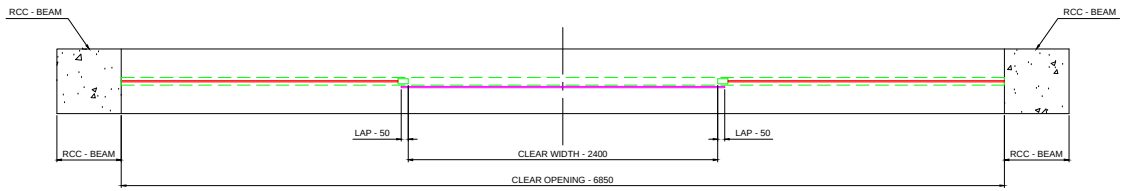

REV NO	DATE	DRAWN	REMARK
R01	04.07.19	P.V.A	1. LOGO ADDED.

This drawing & design is the property of NIHVA TECHNOLOGIES. Not to be sold or copied to any other concern.

TITLE

AUTOMATIC GLASS DOOR

	NAME	SIGN	DATE
DRAWN	P.V.A		16.05.2019
CHECK	V.M.T		16.05.2019
APPRD.			

If any queries contact : design@nihva.com

ALL DIMENSION ARE IN mm

NIHVA TECHNOLOGIES PVT. LTD.
NIHVA TECHNOLOGIES PVT. LTD. PUNE
Tel : 020 66304033
Email:- info@nihva.com
Website:- www.nihva.com

CLIENT - M/S. SHANKARACHARYA HOSPITAL.

PROJECT - M/S. SHANKARACHARYA HOSPITAL.

SITE LOCATION - CHHATTISGARH

DWG. NO. : NIHVA/19-20/0021/R01 | REV- R01

SCALE: NTS | WT: | SHEET:

SR.NO	TOTAL WIDTH	TOTAL HEIGHT	CLEAR OPENING WIDTH	CLEAR OPENING HEIGHT	QTY
01	6850	3620	2400	2400	1 NO