
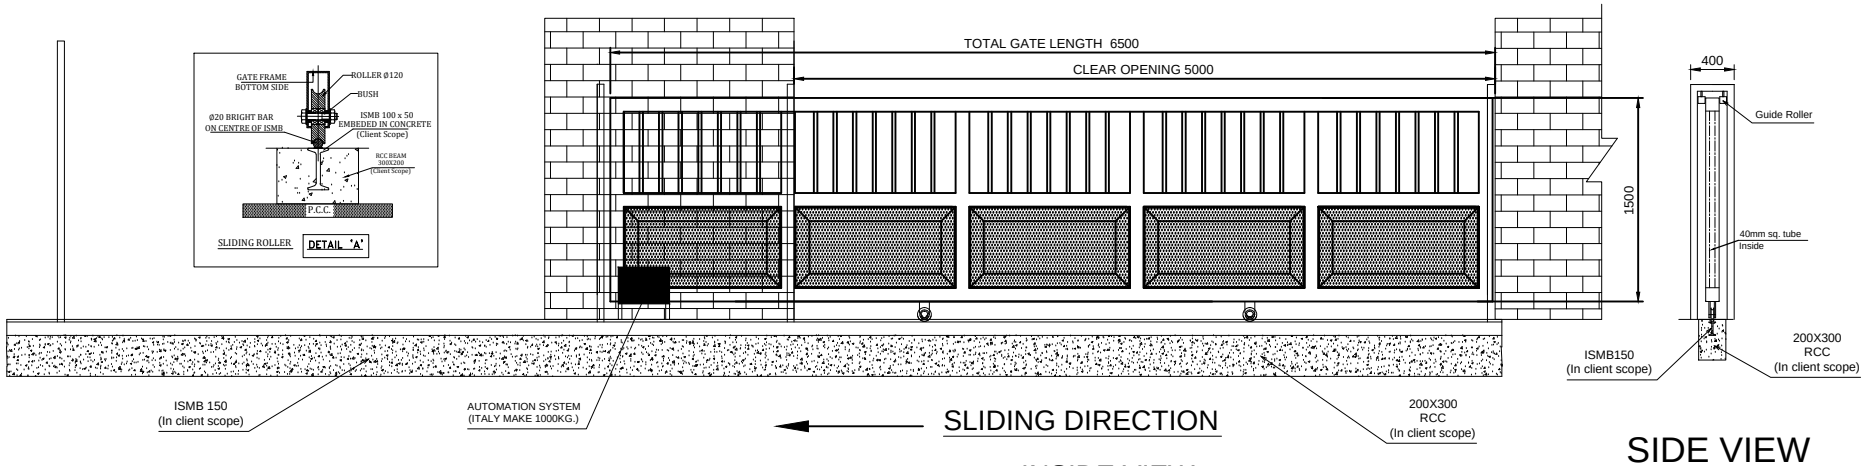



SLIDING DIRECTION

INSIDE VIEW


SIDE VIEW

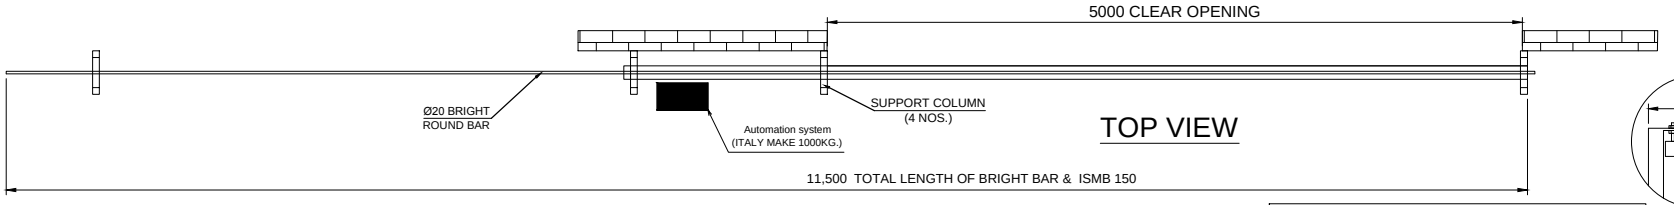

TOP VIEW

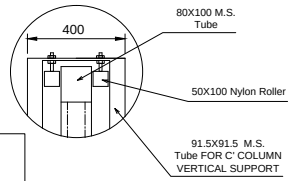

Clear Opening size	- 5000X1500mm
Total length of gate	- 6500X1500mm
No. Of Column	- 4 nos.
Factory paint finish	- Red oxide primer coat
NOTE :-	*ALL REQ. CIVIL WORK WILL BE IN CLIENT SCOPE.

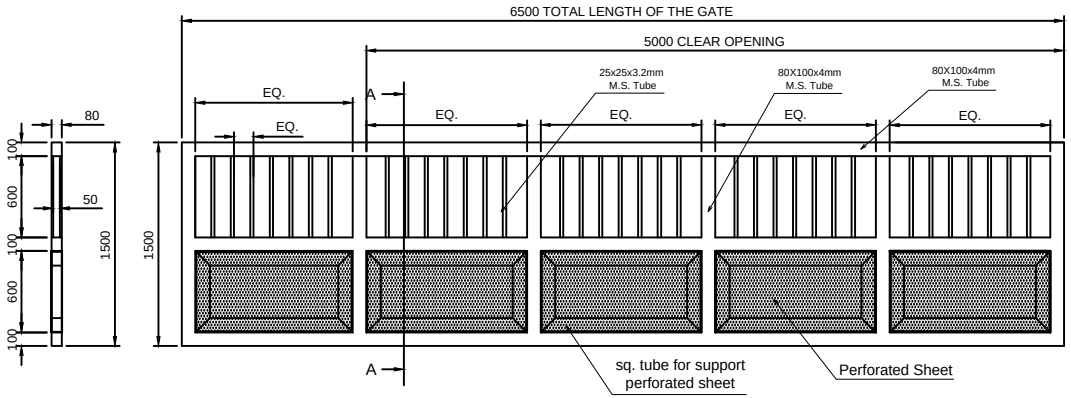

This drawing & designing is the property of NIHVA TECHNOLOGIES. Not be sold or copy to any other concern.

TITLE	MOTORIZED SLIDING GATE	
	SIGN	DATE
DRAWN	ABHIJIT	16/10/15
CHECK	ANIL	16/10/15
REV.	02	
APPROVAL		
If any queries contact : projects@nihva.com		
ALL DIMENSION ARE IN mm		

NIHVA TECHNOLOGIES PVT. LTD.
NIHVA TECHNOLOGY PVT. LTD. PUNE
Tel : 020 66304033
Email:- info@nihva.com
Website:- www.nihva.com

CLIENT - REWARD CONSTRUCTION		
PROJECT - GIVAUDAN		
SITE - RANJANGAON MIDC		
DWG. NO. : NIHVA/15-16/104		
SCALE: 01	WT:	SHEET: 01 OF 01