


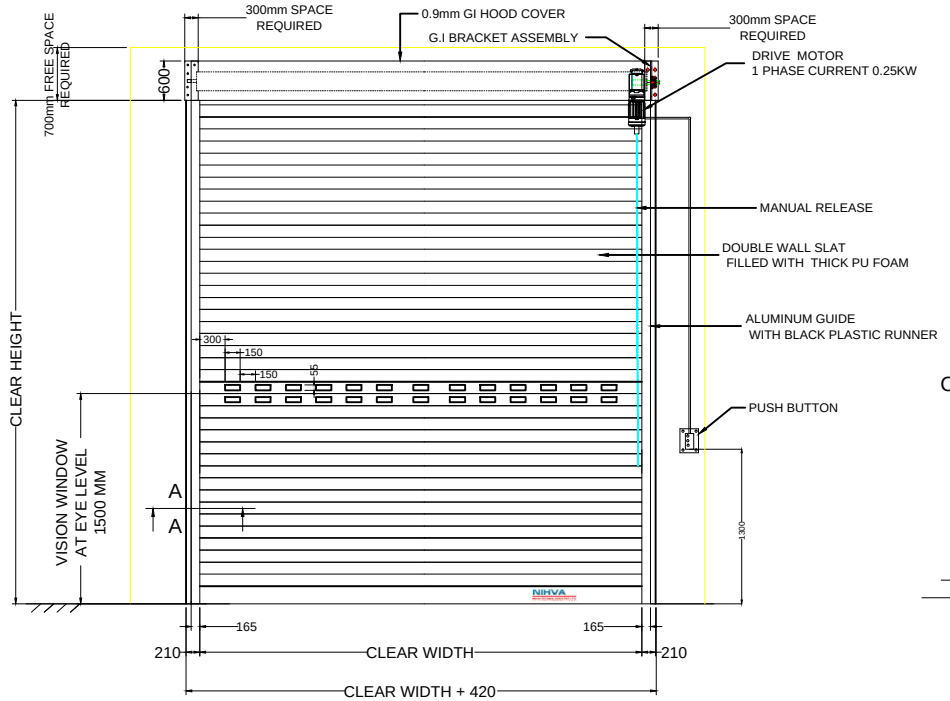


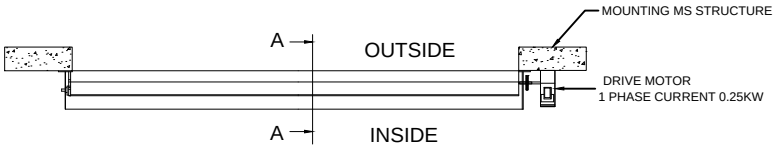

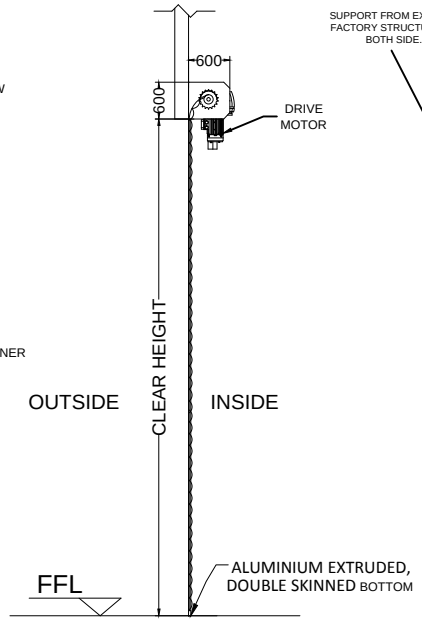


Section A-A

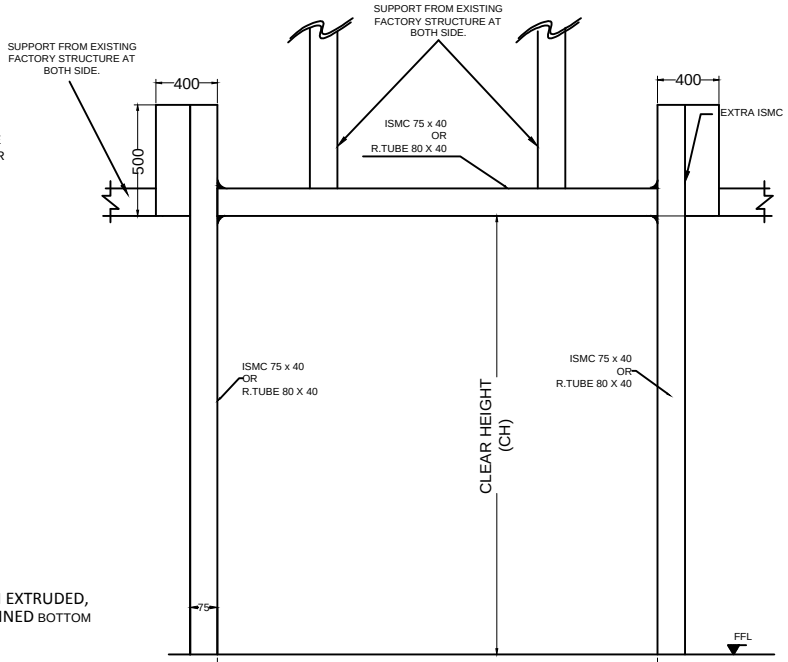

STRUCTURE

CLIENT SCOPE


1) 16A 3 PIN INDUSTRIAL TYPE FEMALE SOCKET 230V, 50HZ,
WITH EARTH AROUND 1/2 METER FROM CONTROLLER/OPERATOR.
2) ALL CIVIL WORK WILL BE CLIENT'S SCOPE.
3) TECHNICAL MS STRUCTURE REQUIRED FOR SHUTTER IS IN CLIENT'S SCOPE.

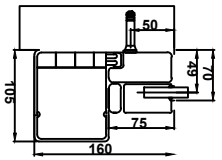

SECTION DETAIL

MAIN SLATS
DOUBLE WALL ROLLING SHUTTER



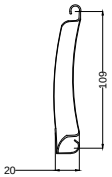

STANDARD COLOR OF SLATS & SHUTTER -RAL9002 (GRAY WHITE)

NOTE : DOOR TO BE FIXED FROM INSIDE ONLY

This drawing & design is the property of NIHVA TECHNOLOGIES. Not to be sold or copied to any other concern.

TITLE	DOUBLE WALL ROLLING SHUTTER	NIHVA TECHNOLOGIES PVT. LTD. PUNE	
		NIHVA TECHNOLOGIES PVT. LTD.	Tel : 020 66304033 Email:- info@nihva.com Website:- www.nihva.com
	NAME / SIGN / DATE		
DRAWN	S.S. / 6.10.2020	CLIENT - M A ENGINEERING	
CHECK	P.A / 6.10.2020	PROJECT - JOHN DEERE INDIA PVT LTD	
APPRD.		SITE LOCATION - PUNE	
If any queries contact : projectsupport@nihva.com		DWG. NO. : NIHVA/20-21/0058	REV- R00
ALL DIMENSION ARE IN mm		SCALE: NTS / WT: / SHEET:	