




MODEL : SKB-G65
THICKNESS 3mm
GALVANISED STEEL GUIDE RAIL

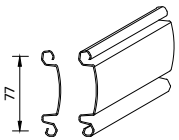

MODEL : SKB-A7
SHUTTER SLAT

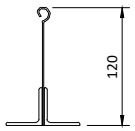


MODEL : SKB-T120
FIRE RATED BOTTOM BAR

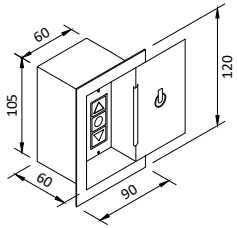


PUSH BUTTON

SHUTTER MODEL	SKB A7 MODEL - FIRE RATED
SHUTTER TYPE	SKB 2 HOURS FIRE RATED ROLLER SHUTTER (BS476 PART 22)
SHUTTER SLATS	SKB-A7 ZINC SOLID SLATS SINGLE SKIN 1.2mm THICKNESS
SLATS FINISHING	POWDER COATED TO SKB STD RAL COLOR
GUIDE RAIL	SKB G65 GALVANIZED GUIDE RAIL
GUIDE RAIL FINISHING	POWDER COATED TO SKB STD RAL COLOR
BOTTOM BAR	SKB T-120 GUIDE RAIL
BOTTOM BAR FINISHING	POWDER COATED TO SKB STD RAL COLOR
BOX DESIGN	MILD STEEL SECTION FRAME DESIGN
OPERATION	SKB 500 MOTORISED WITH MANUAL CHAIN OVERRIDE
MOTOR POWER SOURCE	230VOLTS, 1 PHASE 50HZ.
FIRE MODE	ERA- EMERGENCY RELEASE SYSTEM READY TO RECEIVED 24VDC FIRE SIGNAL FROM FIRE CONTROL ROOM AND SHUTTER SHALL CLOSE DOWN BY GRAVITY FORCE WITHOUT DELAY (AUTO RESET)
	TFL-THERMAL FUSSIBLE LINK WILL AUTO CLOSE BY GRAVITY WHEN ROOM TEMPERATURE RISES UP TO 71 C^{o}
	FIRE SIGNAL OF 24VDC 400mA ARE REQUIRED
ADDITIONAL ITEM	


SHUTTER NO.	LOCATION	CLEAR WIDTH (mm)	CLEAR HEIGHT (mm)	QTTY.	MOTOR LOCATION
FRS-01	.	4000 mm	4000 mm	1	RIGHT

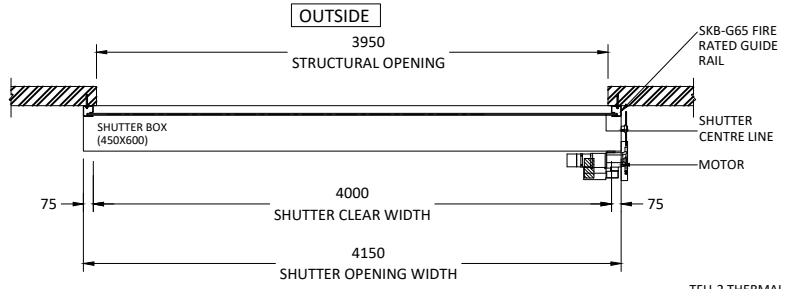


PLAN VIEW

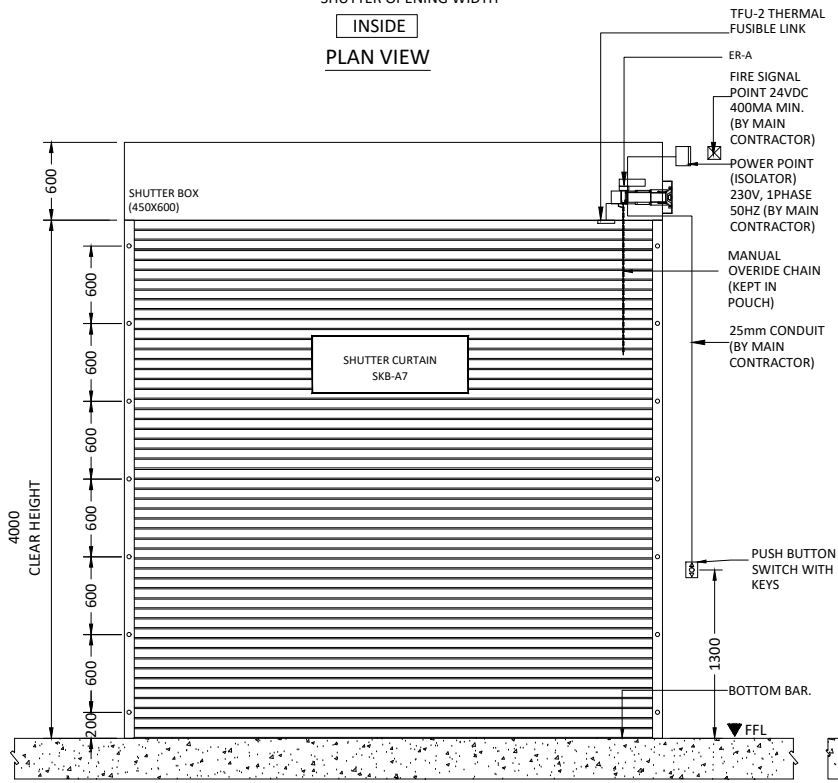

ELEVATION VIEW

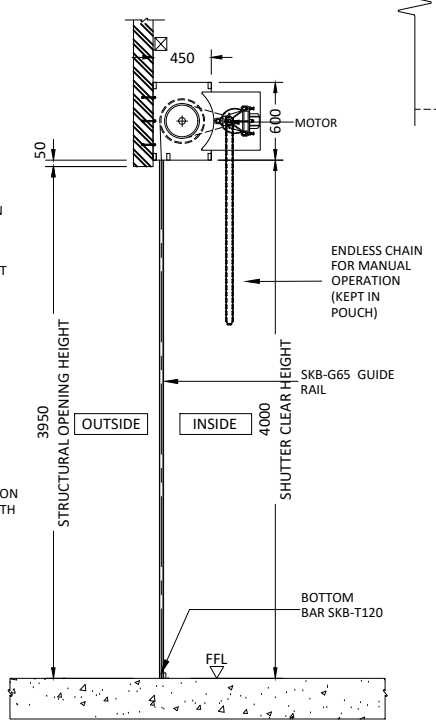

SECTION VIEW

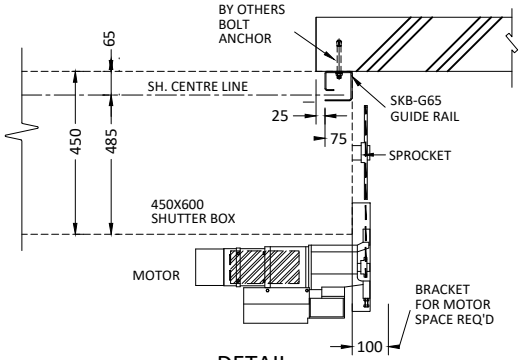

DETAIL

SHOP DRAWING

NO.	DATE	AMENDMENTS
02	24.1.24	Clear width & height changes

DEVELOPER / LANDOWNER:

ARCHITECTURAL:

CONSULTANT :

MAIN CONTRACTOR :

INSTALLER :

MANUFACTURER:

SKB STORAGE INDUSTRIES SDN.BHD
Lot 22 Jalan Teknologi, Taman Sains
Selangor,Kota Damansara
47810 Petaling Jaya,Selangor Darul Ehsan
Tel:(60) 3 6157 2277 Fax:(60) 3 6157 2211

PROJECT TITLE:

NIHVA TECHNOLOGIES PVT LTD
PROJECT : SUPPLY ONLY

DRAWING TITLE:

SKB 2 HRS FIRE RATED ROLLER SHUTTER - BS 476 PART 22

DRAWN: A.D	CHECKED : LYN	DRAWING NO:	REV:
SCALE: NTS	DATE: 24-1-2024	NIHV-FRS-24-JAN-A7-BS-001 -V01.DWG	V02