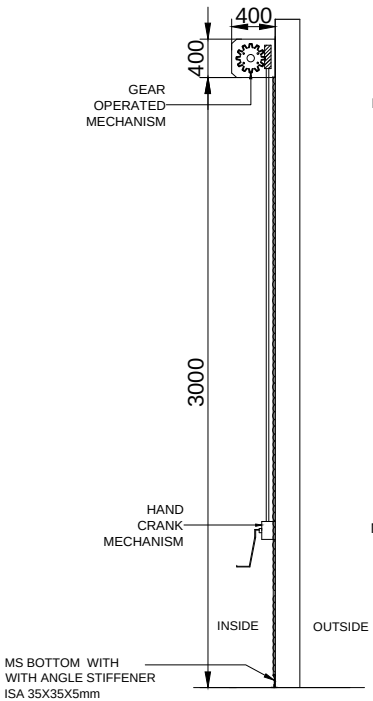
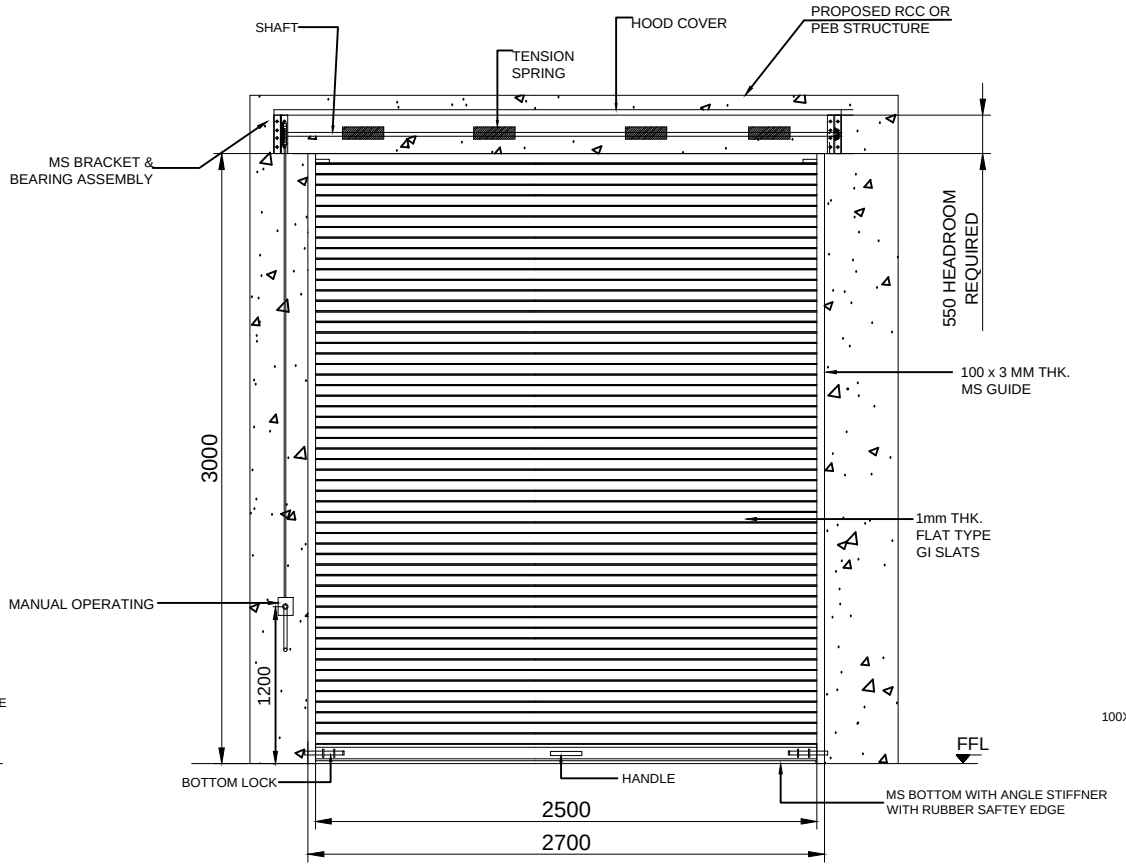
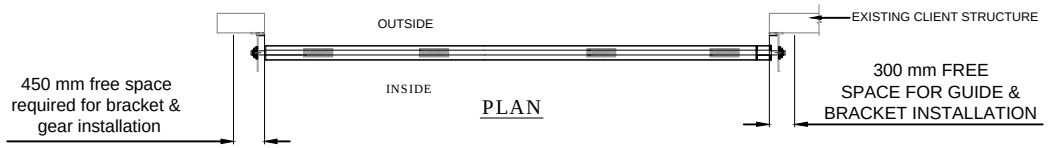


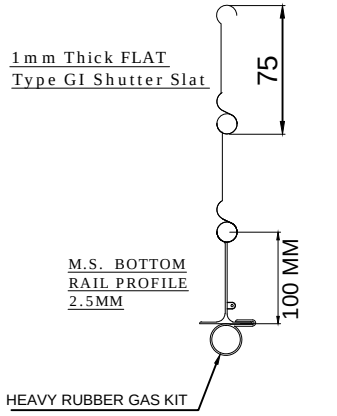

SIDE VIEW



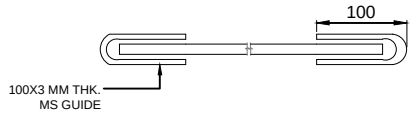

INSIDE ELEVATION




PLAN




M.S. BOTTOM RAIL PROFILE 2.5MM




| SR.NO. | RAL COLOR |
|---|---|
| 01 | RAL 9002 (WHITE GREY) |

| SR.NO. | SIZE | QUANTITY |
|---|---|---|
| 01 | 2500(W)X3000(H) | 30 |

| S.NO | FEATURE | EQUIPMENT DETAILS |
|---|---|---|
| 01 | SLATS MODEL | GALVANISE STEEL(GI) SLATS 1mm THK. |
| 02 | GUIDE RAIL | 100 X 3mm THK MILD STEEL(MS). |
| 03 | BOTTOM RAIL | 2.5mm THK MILD STEEL (M.S.). |
| 04 | HOOD COVER | 0.9mm THK GALVANISE STEEL (GI). |
| 05 | RAL COLOR | RAL 9002 |

NOTE-
1. ALL CIVIL WORK WILL BE CLIENT'S SCOPE.

TOLERANCE - ±10mm

This drawing & design is the property of NIHVA TECHNOLOGIES. Not to be sold or copied to any other concern.

TITLE
GEAR OPERATED ROLLING SHUTTER

NIHVA TECHNOLOGIES PVT. LTD.

NIHVA TECHNOLOGIES PVT. LTD. PUNE
Tel : 020 66304033
Email:- info@nihva.com
Website:- www.nihva.com

| | NAME | SIGN | DATE |
|---|---|---|---|
| DRAWN | PRADEEP | | 14-07-2018 |
| CHECK | SURAJ | | 14-07-2018 |
| APPRD. | R.D | | 14-07-2018 |

CLIENT -
PROJECT-
SITE LOCATION -
If any queries contact : design@nihva.com
DWG. NO. : NIHVA/18-19/VDR/162
REV- 01
ALL DIMENSION ARE IN mm
SCALE: NTS
WT:
SHEET: 01 OF 01