


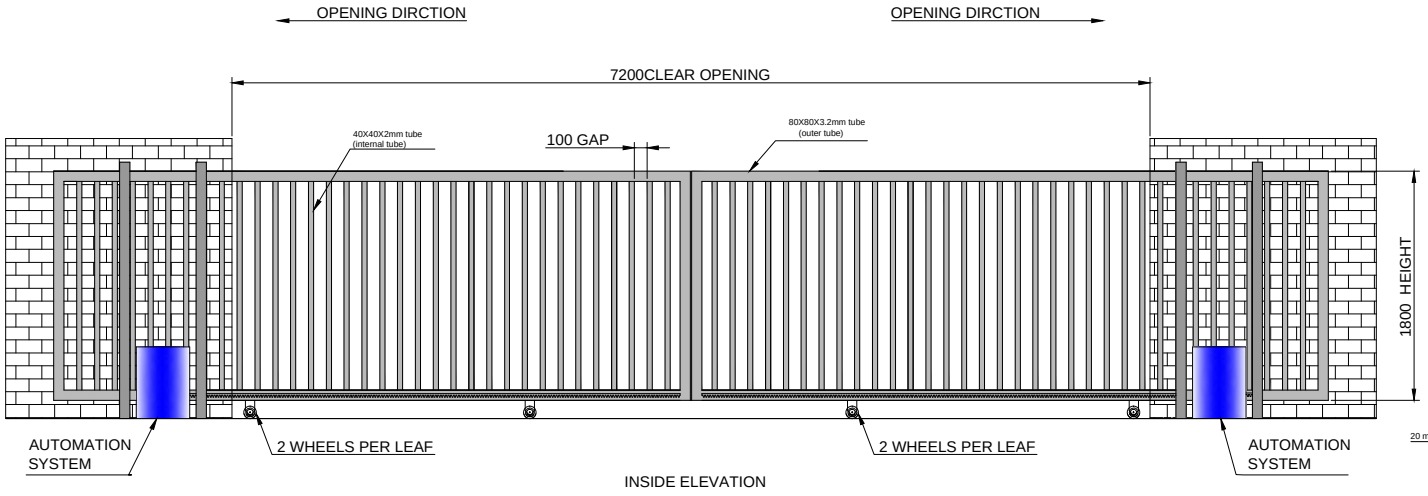


INSIDE ELEVATION

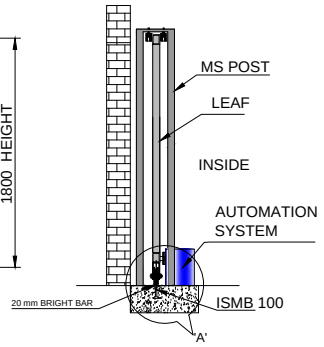

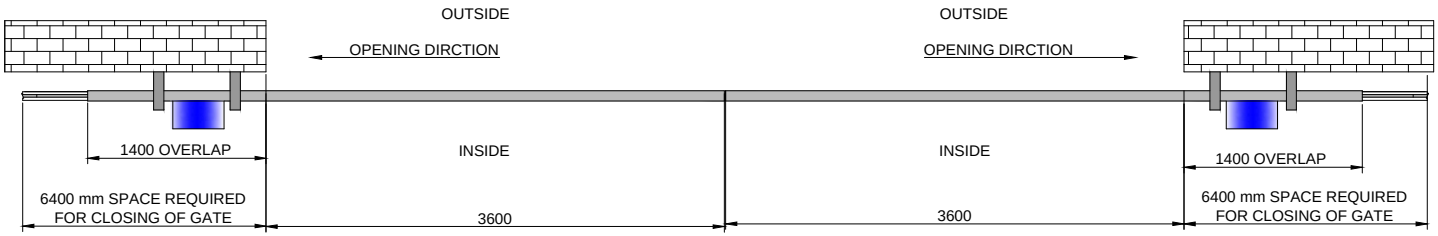

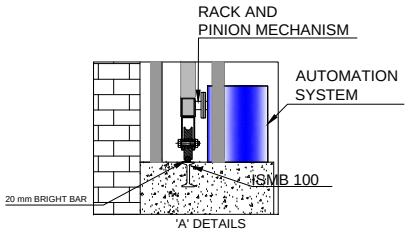

'A' DETAILS

DIMENSION :

CLEAR WIDTH	CLEAR HEIGHT	QUANTITY
7200mm	1800mm	1 NOS

MATERIAL:

THICKNESS :

NIHVA TECHNOLOGIES PVT. LTD.

NIHVA TECHNOLOGIES PVT. LTD. PUNE
Email:- info@nihva.com
Website:- www.nihva.com

TITLE:

AUTOMATIC SLIDING GATE

CLIENT'S APPROVAL :

CLIENT - TATA PROJECT

PROJECT - ALSTOM

SITE LOCATION -HYDRABAD

DWG. NO. : NIHVA/16-17/179

SCALE: NTS	WT:	SHEET:1 OF 1
DRAWN BY: SURAJ		DATE: 11-03-2017
CHECK BY : OMKAR		DATE: 11-03-2017
APPROVED BY : R.K		DATE: 11-03-2017

If any queries contact : projects@nihva.com

NOTE: ALL DIMENSIONS ARE IN mm

THIS DRAWING & DESIGN IS THE PROPERTY OF NIHVA TECHNOLOGIES. NOT TO BE SOLD OR COPIED TO ANY OTHER CONCERN.