

SCISSOR LIFT SIZE	WIDTH (W)	LENGTH (L)	HEIGHT (H)	LIP (C) LENGTH
	2000	2000	800	300


PIT DIMENSION	WIDTH (W 1)	LENGTH (L 1)	DEPTH (D)	ALL DIMENSIONS ARE IN mm
	2150	2150	805	

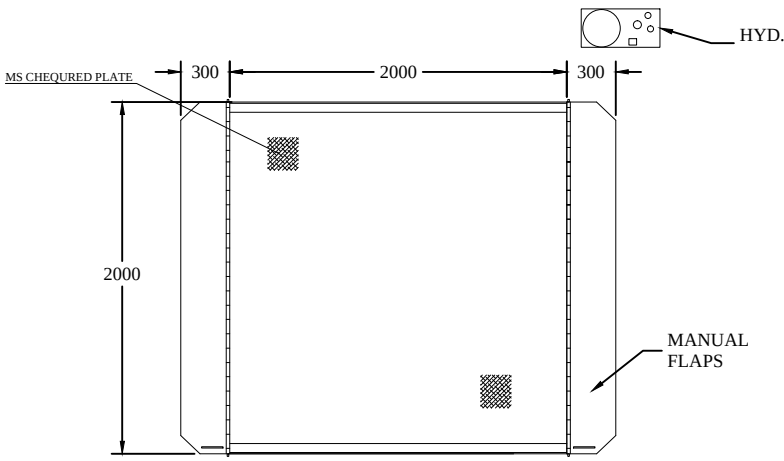

PLAN

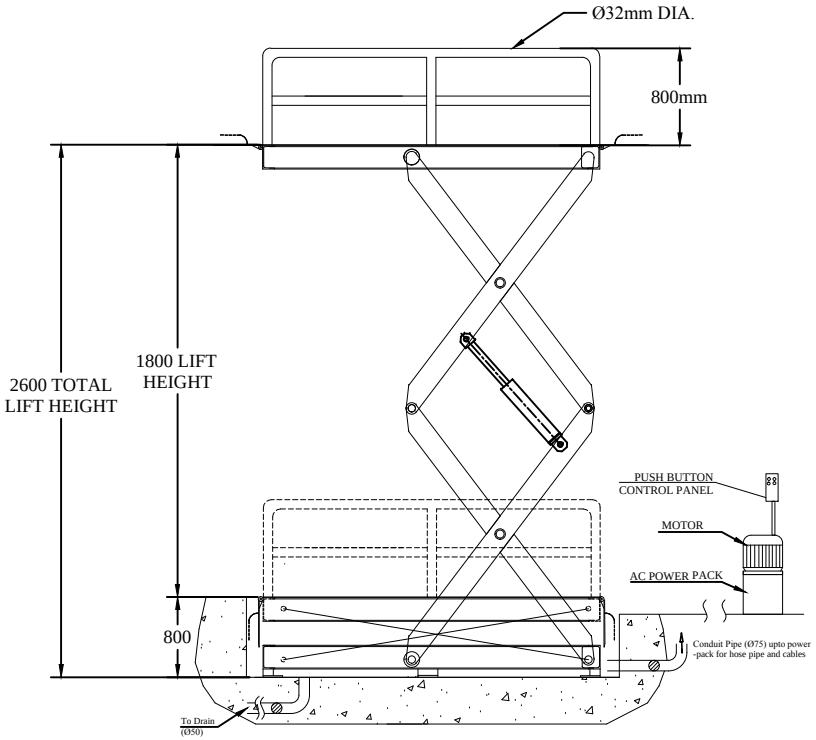

ELEVATION

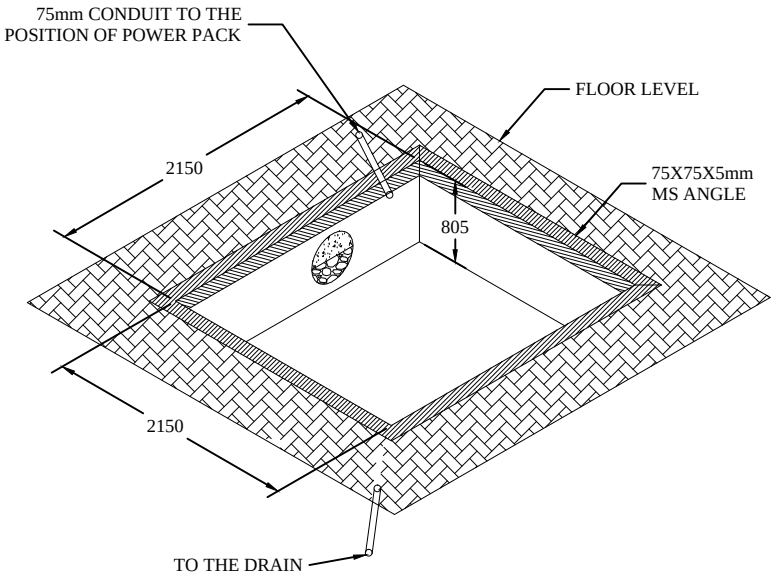

PIT DRAWING

COLOR- PU PAINT SCHEME WITH STANDARD COLOR.

SCISSOR LIFT- 2000 KG CAPACITY

TOLERANCE -±10mm

This drawing & designing is the property of NIHVA TECHNOLOGIES. Not be sold or copy to any other concern.

TITLE	SCISSOR LIFT			NIHVA TECHNOLOGY PVT. LTD. PUNE
	NAME	SIGN	DATE	NIHVA TECHNOLOGIES PVT. LTD. Tel : 020 66304033 Email:- info@nihva.com Website:- www.nihva.com
DRAWN	SURAJ		01/11/17	CLIENT -
CHECK	OMKAR		01/11/17	PROJECT -
APPD.	SHEKHAR		01/11/17	SITE -
MFG.				DWG. NO. : NIHVA/17-18/VDR/0163 REV. : 0
If any queries contact : projects@nihva.com				SCALE: NTS WT: SHEET: 01 OF 01
ALL DIMENSION ARE IN mm				