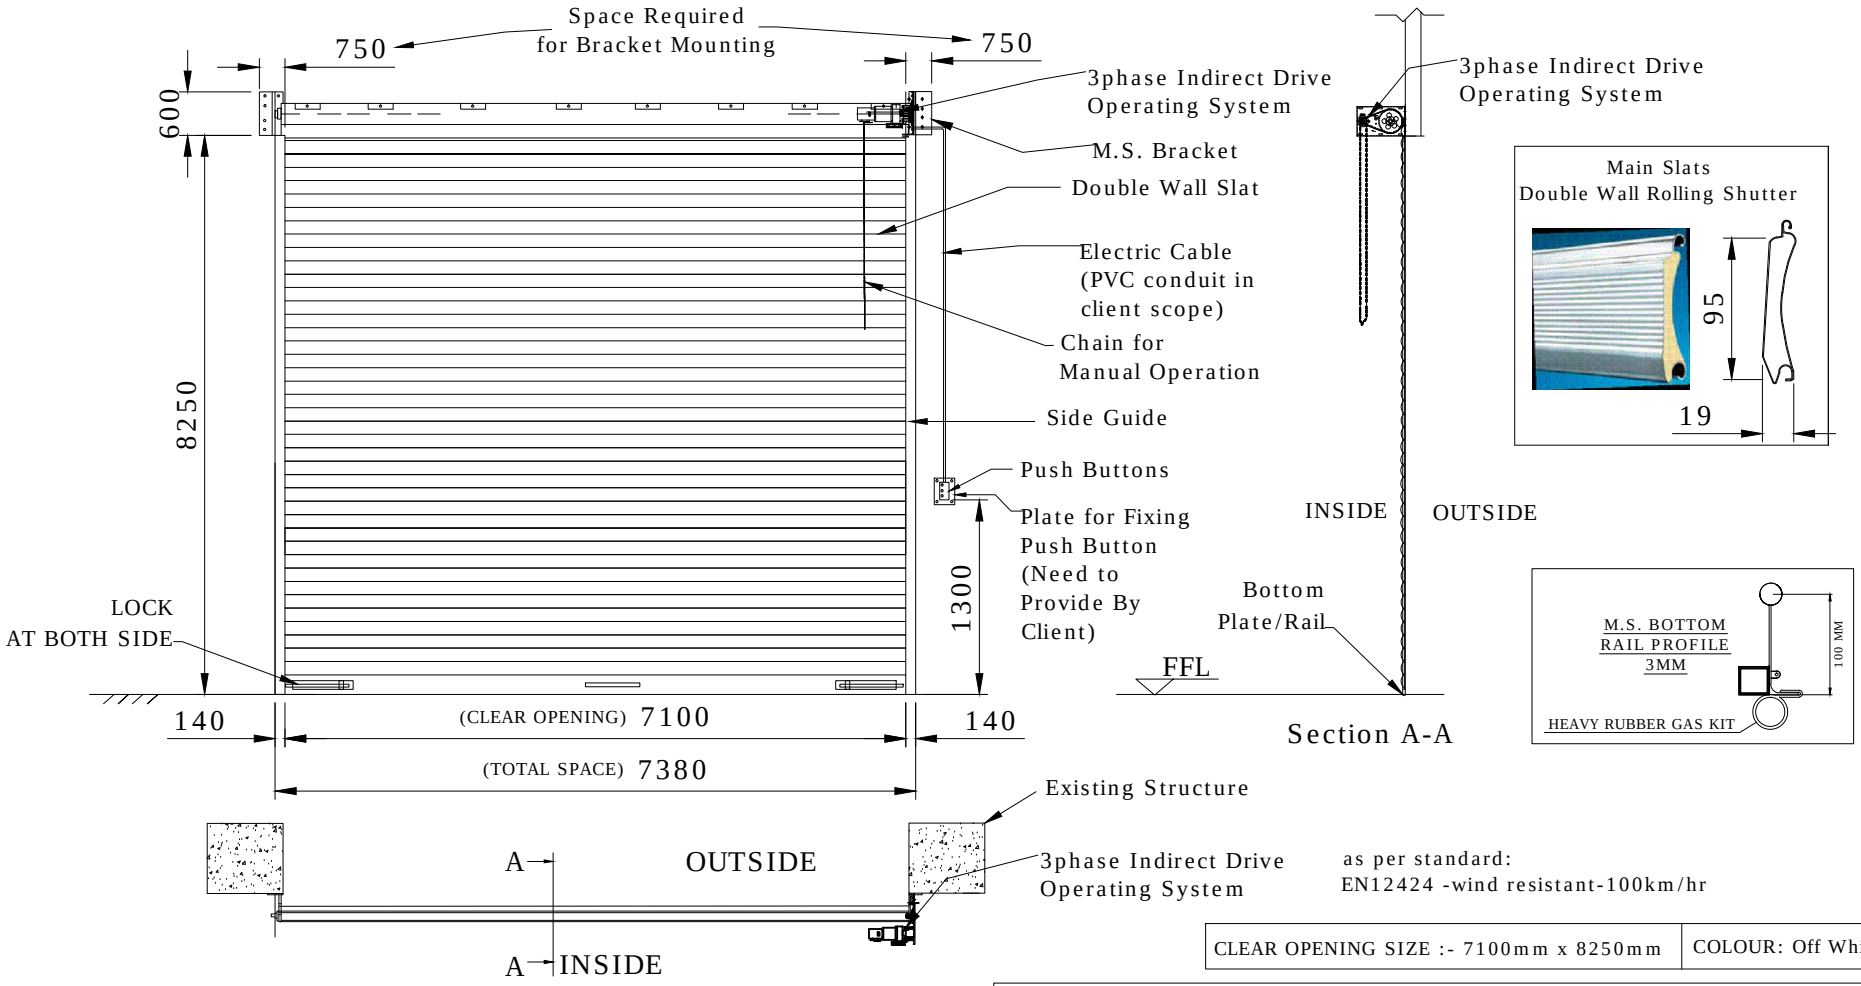


as per standard:
EN12424 -wind resistant-100km/hr

CLEAR OPENING SIZE :- 7100mm x 8250mm	COLOUR: Off White

NOTE: push button fixing will be decided as per site ready condition.

Sr. No.	Details	Specification
1)	Slats Profile	95mm x 19mm with PU filled inside/ Length-7320
2)	Guide Channel	140mm x 50mmx3mm/ Length-8277
3)	Shaft	125mm OD with heavy duty flanges and hardwarex3.2mm / Length-7300
4)	Bottom Rail	120mm with extra 50x50 sq. tube support Locking arrangement provides
5)	Brackets	750mmx600mmx6mm thickness

TITLE:

DOUBLE WALL
ROLLING SHUTTER

CLIENT APPROVAL

This drawing & designing is the property of NIHVA TECHNOLOGIES. Not be sold or copy to any other concern.

ALL DIMENSION ARE IN mm

	SIGN	DATE
DRAWN	ABHIJIT	28/10/15
CHECK	ANIL	28/10/15
REV.	02	
APPRD.		
MFG		
Ref. No.		

NIHVA TECHNOLOGY
PVT. LTD. PUNE
Tel : 020 66304033
Email:- info@nihva.com
Website:- www.nihva.com

CLIENT - PHENIX

PROJECT - ENNORE

SITE - CHENNAI

DWG. NO. -NIHVA/15-16/161

SCALE: 01 | WT: | SHEET: 01 OF 01

If any queries contact : projects@nihva.com