


A1 DO NOT SCALE DRAWING. CHECK ALL DIMENSIONS ON SITE.
ALL RIGHTS RESERVED.
INTEGRATED DESIGN ASSOCIATES INDIA PVT. LTD.

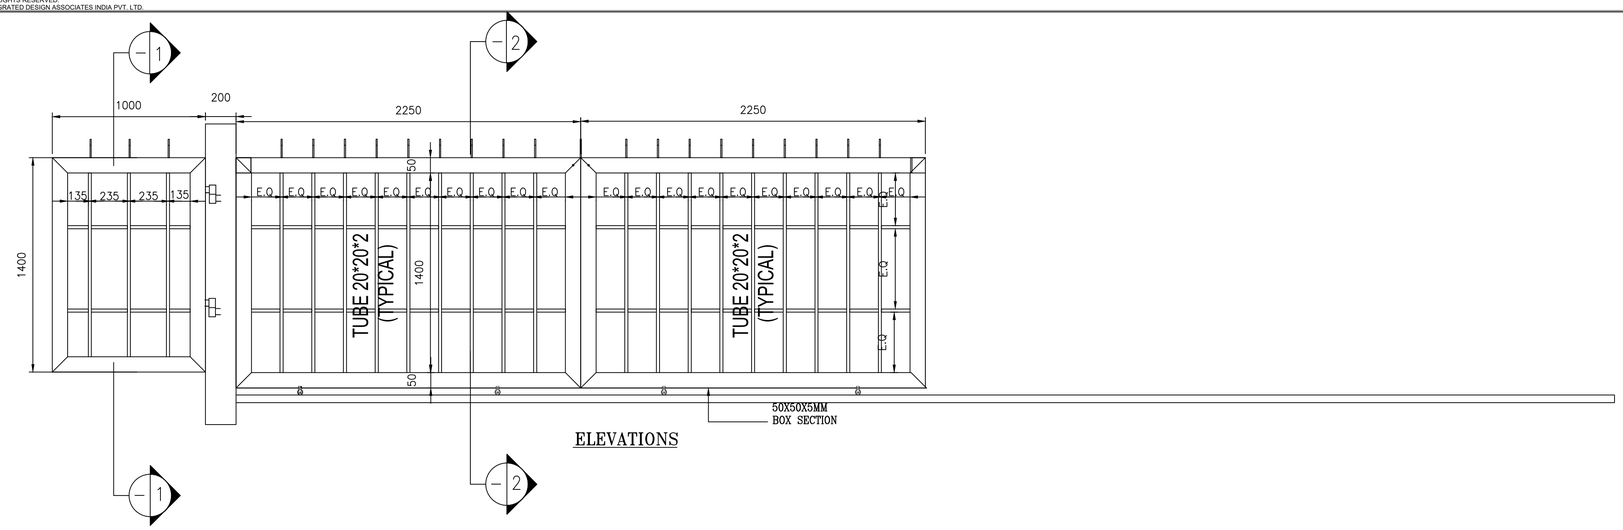


ELEVATIONS

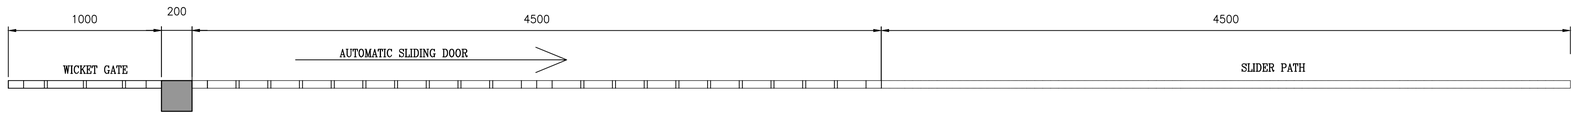


PLAN

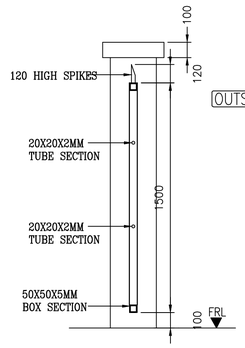

SECTION 1-1

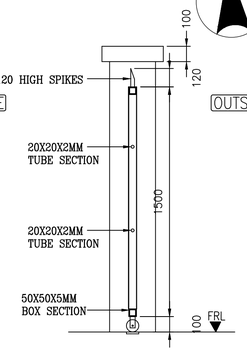


SECTION 2-2

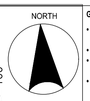

GENERAL NOTES:


- Architectural Drawing shows equipment space holders only, for equipment layout please refer to individual service drawing.
- Refer Structural Drawings for Plinth Setting out
- For Boom Barrier, Mechanical Bollards and Security gates, kindly refer to seperate drawings (By Others)
- For door/window/louver details and schedules, refer to detail drawing.

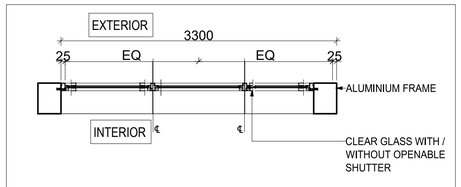


PARTIAL GLASS PARTITIONS PLAN

3300X1200

ALUMINIUM FRAME & GLAZED WINDOW

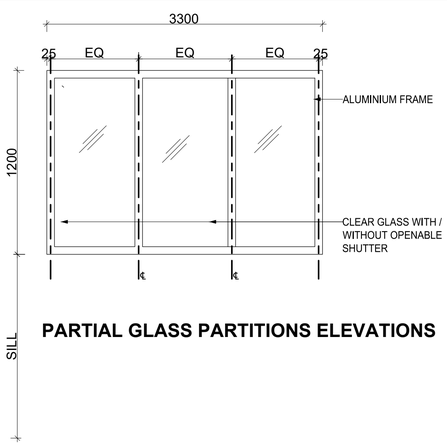

PARTIAL GLASS PARTITIONS ELEVATIONS

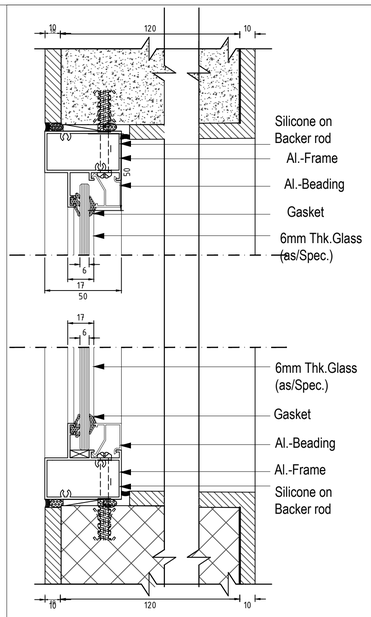


PARTIAL GLASS PARTITION
CROSS SECTIONS

REV	DATE	DESCRIPTION

DSGN			
DRWN			
CHKD			
APPD			
	NAME	SIGN	DATE

KEY PLAN:

SCALE 1:75000

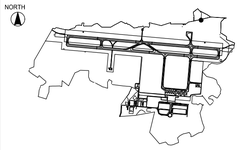

PROJECT:

GREENFIELD INTERNATIONAL AIRPORT AT MOPA, GOA

CLIENT:

GMR GOA INTERNATIONAL AIRPORT LIMITED

EPC CONTRACTOR:

MEGAWIDE CONSTRUCTION DMCC

ARCHITECTURAL CONSULTANT:

INTEGRATED DESIGN ASSOCIATES INDIA PVT. LTD.
c/o Anil Mehta & Associates,
5th Floor, Midas Chambers, Off New Link Road
Andheri West, Mumbai - 400053
Maharashtra, India

STRUCTURAL CONSULTANT:

SY^2 + ASSOCIATES, Inc.
9801 Kamagong Street
Makati Philippines.

MEP CONSULTANT:

ESKAYEM
CONSULTANTS PVT LTD.
301, 3RD FLOOR, SWASTIK CHAMBERS,
C.S.T. ROAD, CHEMBUR, MUMBAI-400071
TEL 022-25262645/46/47

PACKAGE:

SECURITY GATE HOUSE

TITLE:

GATE HOUSE TYPICAL SLIDING & WICKET GATE & PARTIAL GLASS PARTITION DETAILS

DRAWING NO.:

GGIAL-MW-GH1-AR-10-SK-346

FILE REF.:

DATE : 03.06.2022

RELEASED FOR:	SCALE:	SIZE:	REV:
GFC		A1	R0

0 0.5 1.0 1.5 2.0 2.5

SCALE - 1 : 50

USER: INTEGRATED DESIGN ASSOCIATES LTD.