

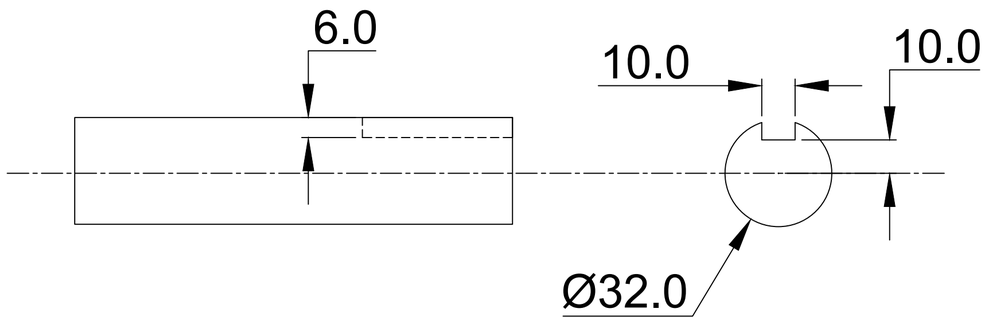



SHAFT DIA. 32 MM

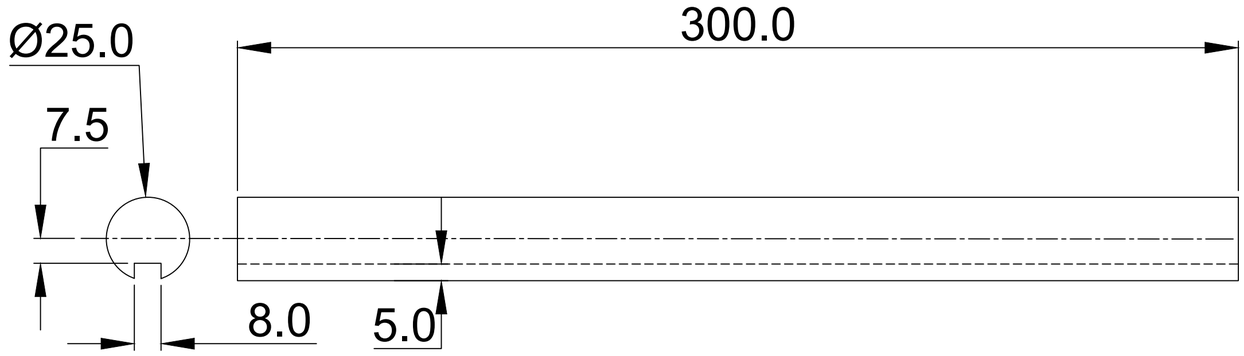


SHAFT DIA. 25 MM

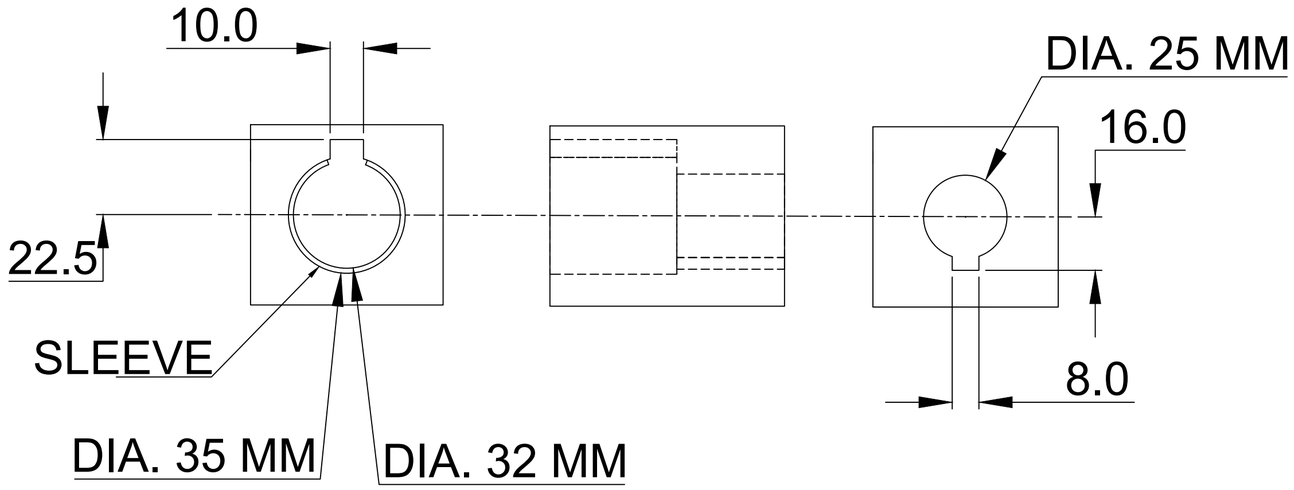


# COUPLING DIA. 32 MM & 25 MM

KEY SIZES-

1. W 8 MM X H 8 MM
2. W 10 MM X H 12 MM

DOOR QTY : 02 NOS

This drawing & design is the property of NIHVA TECHNOLOGIES. Not to be sold or copied to any other concern.

| TITLE | KEY-WAY DWG FOR COUPLING AND SHAFTS | | | NIHVA TECHNOLOGIES PVT. LTD. |
|---|---|---|---|---|
| | NAME | SIGN | DATE | |
| DRAWN | MAHESH S. | | 24.08.2022 | CLIENT - |
| CHECK | MAHESH S. | | 24.08.2022 | PROJECT - |
| APPRD. | AMIT K. | | 24.08.2022 | SITE LOCATION - |
| If any queries contact : sales@nihva.com | | | | DWG. NO. : NIHVA/22-23/VDR/0067 / REV- 0 |
| ALL DIMENSION ARE IN mm | | | | SCALE: NTS / WT: / SHEET: 01 OF 01 |

NIHVA TECHNOLOGIES PVT. LTD. PUNE
Tel : 020 66304033
Email:- info@nihva.com
Website:- www.nihva.com