




Detail B

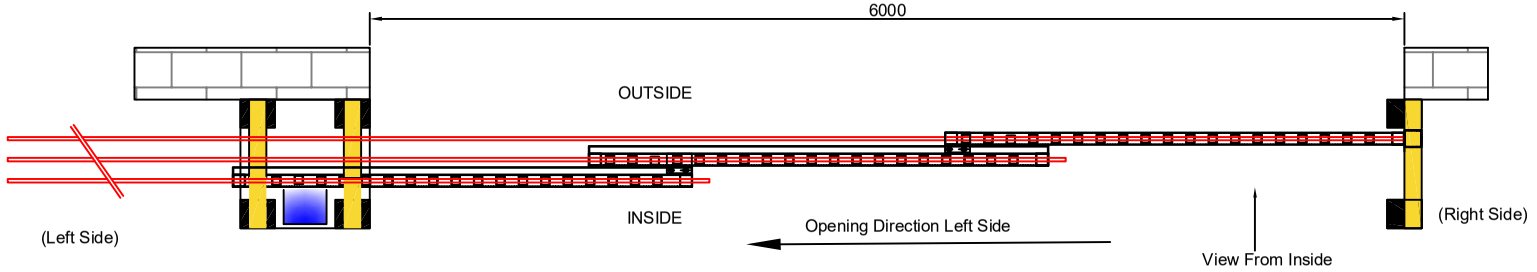

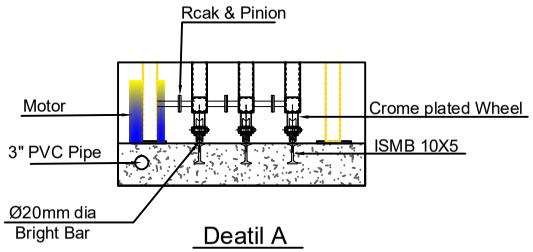

Deatil A

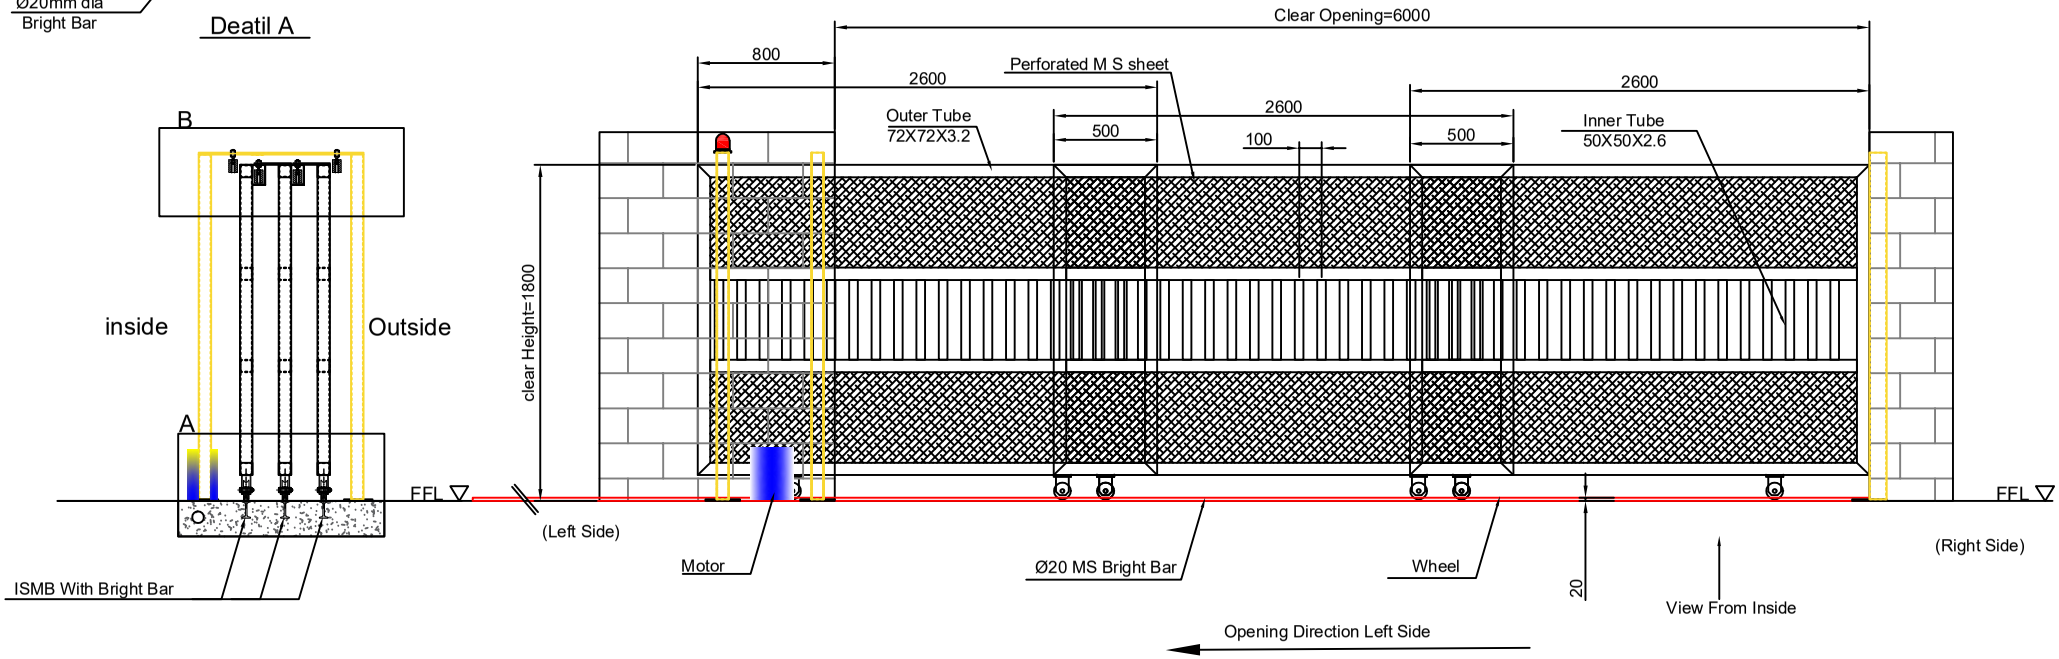

Note:–

1. Given above Tel.Sliding Gate drawing(GA) only for the client understanding purpose.
2. Required all Civil work will be in client scope
3. ALL Dimensions are in mm
4. Required Parking space will be 2760mm

This drawing & design is the property of NIHVA TECHNOLOGIES. Not to be sold or copied to any other concern.

TITLE:- MS Motorised Tel.Sliding Gate

NIHVA TECHNOLOGIES PVT. LTD.
NIHVA TECHNOLOGIES PVT. LTD. PUNE
Tel : 020 66304033
Email:- info@nihva.com
Website:- www.nihva.com

	NAME	DATE	SIGN
DRAWN	SUJATA	24/02/2022	
CHECK	G.PATIL	24/02/2022	
APPRD.	P.J	24/02/2022	

If any queries contact : design@nihva.com

ALL DIMENSION ARE IN mm

CLIENT - INDUS ENGINEES

LOCATION -TALOJA

PRODUCT - TEL.SLIDING GATE QTY:-

DWG NO:-NIHVA/21-22/CLT/0326 REV- 3

SCALE: NTS SCALE:-- 1:1 SHEET: 01 OF 01

Rev No.	Revision	Date	Revised By