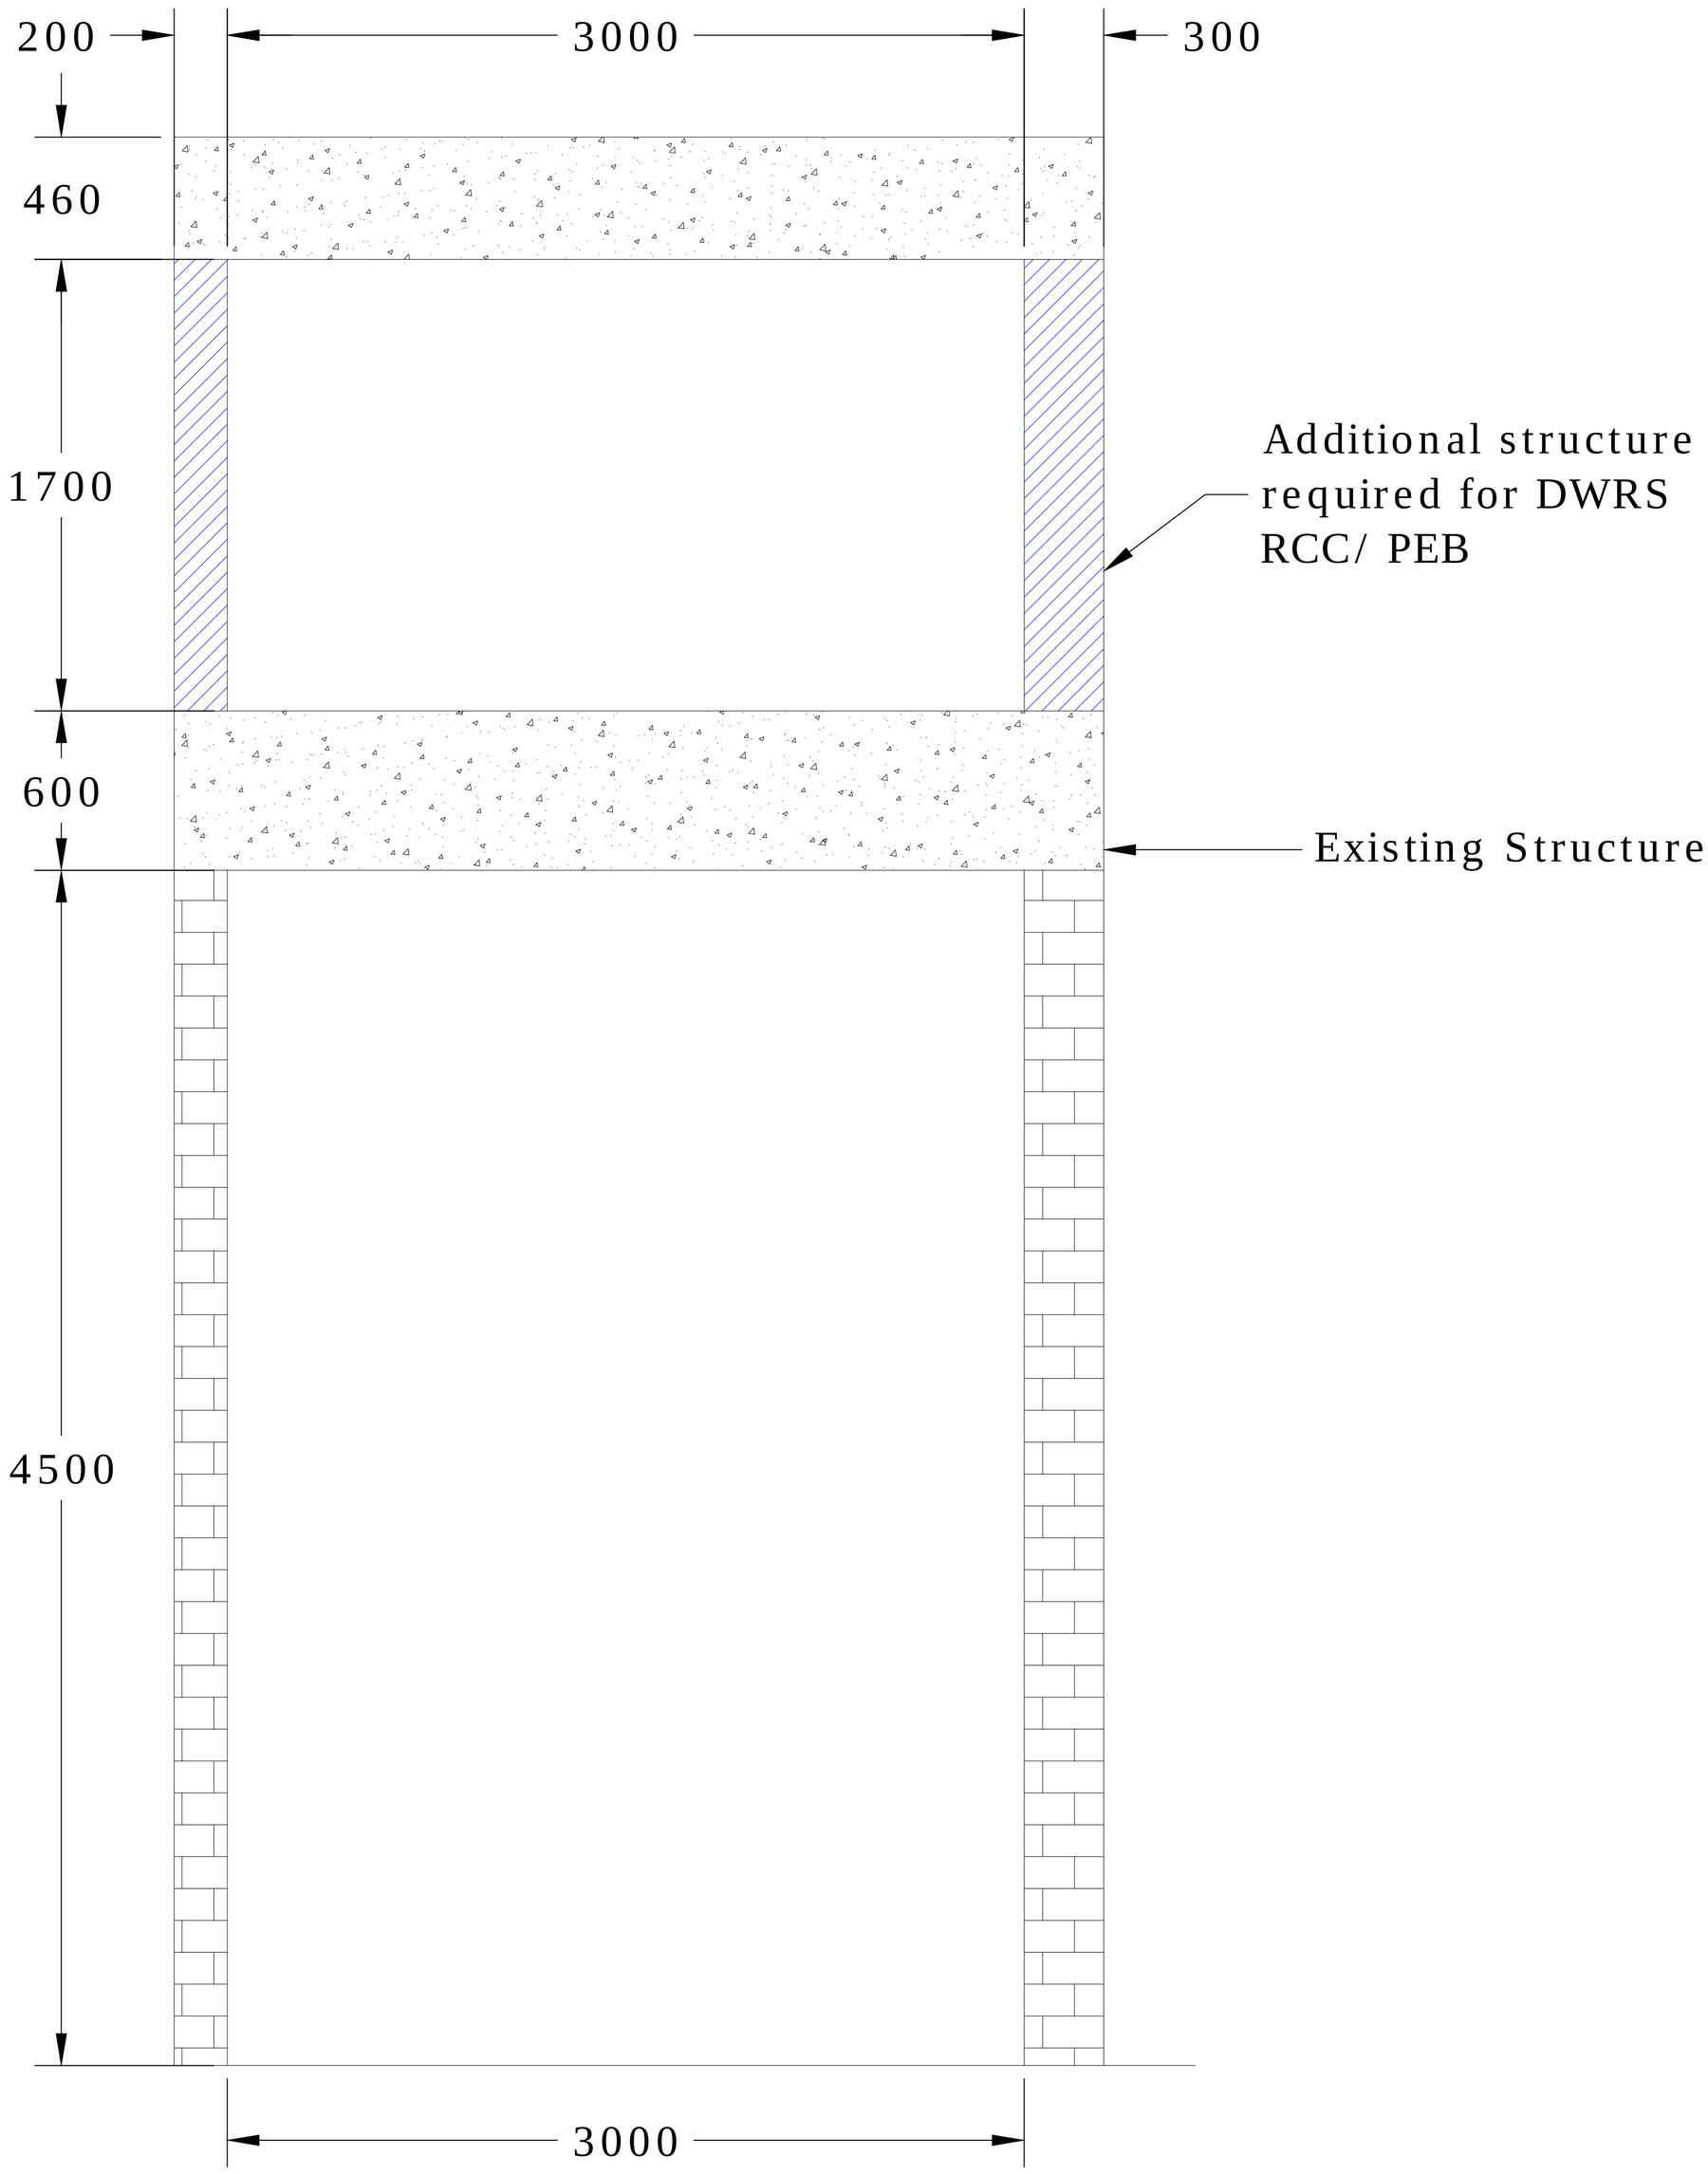



Inside Elevation

Additional Structure required at site for DWRS

Note- 1.Motor mounting will be at right side.
2.Need to construct additional structure,RCC,Wall as per drawing.

SHUTTER LOCATION- SHUTTER 3 STARTS FROM NORTH SIDE.

This drawing & design is the property of NIHVA TECHNOLOGIES. Not to be sold or copied to any other concern.

TITLE

STRUCTURE FOR DWRS 3

CLIENT APPROVAL

ALL DIMENSION ARE IN mm

| | SIGN | DATE |
|---|---|---|
| DRAWN | OMKAR | 30/05/17 |
| CHECK | SAGAR P. | 30/05/17 |
| REV. | | |
| APPRD. | R.K. | 30/05/17 |
| MFG | | |
| Ref. No. | | |

NIHVA TECHNOLOGIES PVT. LTD.

NIHVA TECHNOLOGIES PVT. LTD. PUNE
Tel : 020 66304033
Email:- info@nihva.com
Website:- www.nihva.com

CLIENT - LUPIN

PROJECT - LUPIN

SITE - NAGPUR

DWG. NO. - NIHVA/17-18/0031/R01/3

SCALE: NTS | WT: | SHEET: 01 OF 01

If any queries contact : projects@nihva.com