
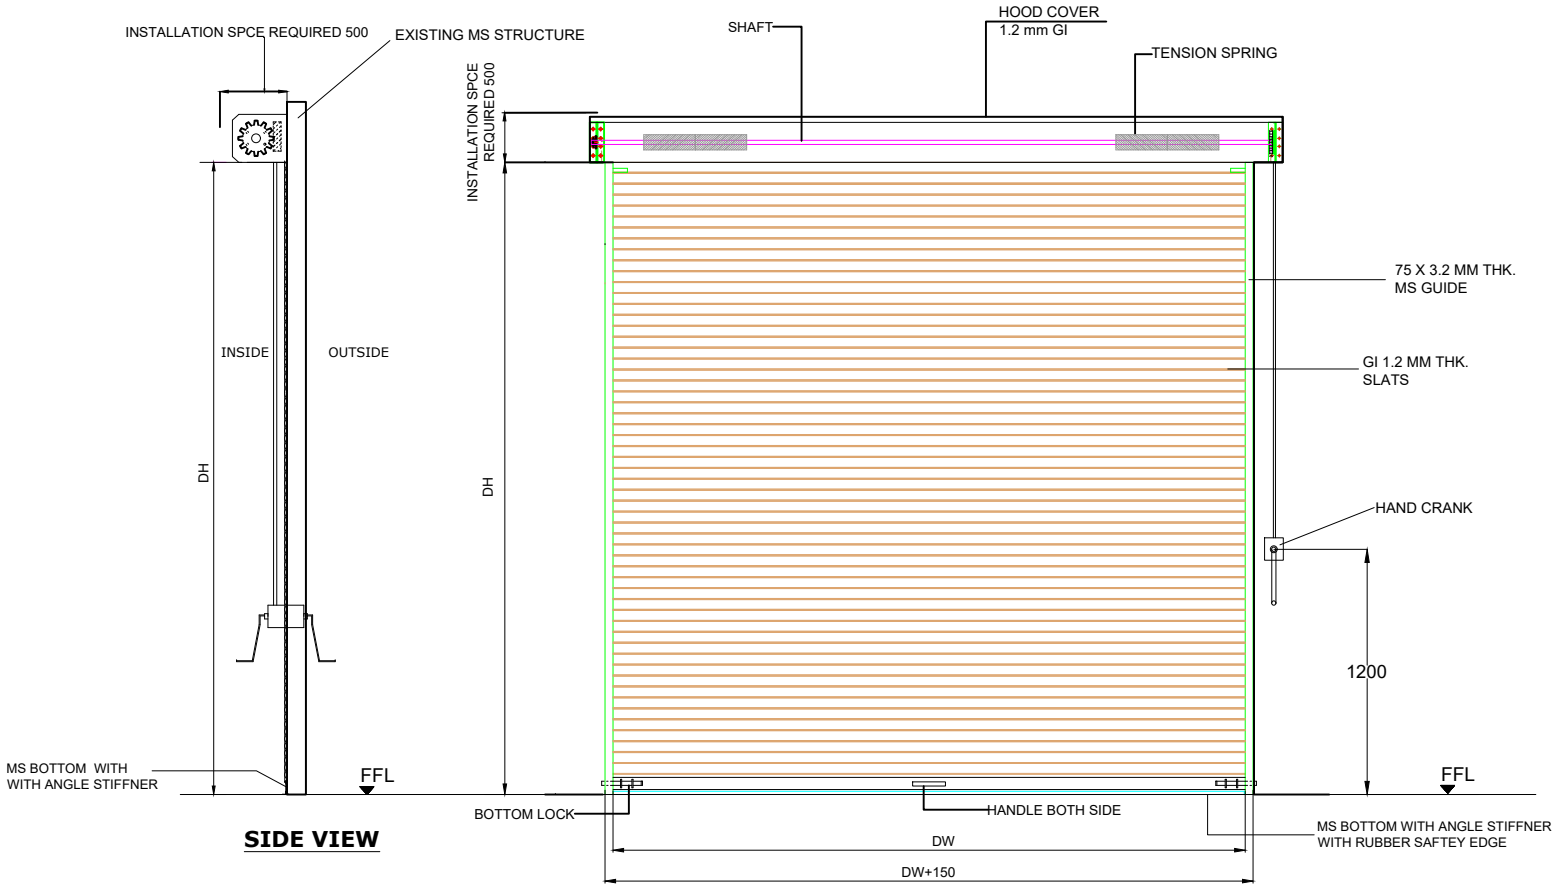


SIDE VIEW

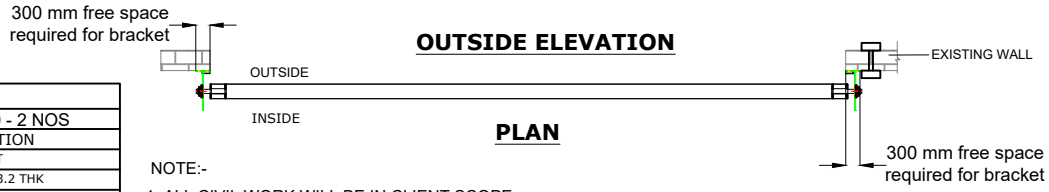


OUTSIDE ELEVATION


PLAN

Curve Type MS Shutter SLATS

M.S. BOTTOM RAIL PROFILE 2MM

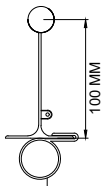

HEAVY RUBBER GAS KIT

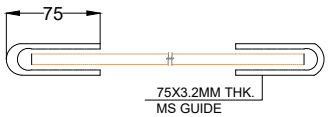

TOLERANCE - ±10mm

TECHNICAL SPECIFICATIONS		
SHUTTER SIZE - DW 4000 x DH 3000 - 2 NOS		
SR NO	DESCRIPTION	SPECIFICATION
1.	SOLID SLAT & QTY	1.2 mm THK GI. SLAT
2.	M.S.GUIDE TYPE & SIZE	U GUIDE OF 75X35X3.2 THK
3.	HOOD COVER 1.2 mm GI	1/SHUTTER
4.	BOTTOM	MS BOTTOM 2 mm THK WITH ANGLE STIFFNER WITH RUBBER SAFTEY EDGE
5.	HAND CRANK	CONSIDERED
6.	HAND CRANK	RH SIDE
7.	SHUTTER MTG LOCATION	INSIDE
8.	SHUTTER MOUNTING BASE	RCC WALL (IN CLIENT SCOPE)
9.	APPROVED RAL SHADE	AS CLIENT APPROVED RAL 9001 : Cream

NOTE:-

1. ALL CIVIL WORK WILL BE IN CLIENT SCOPE.
2. SURFACE FINISH: POWDER COATING OF APPROVED RAL 9001 : Cream.
3. MOUNTING: MS STRUCTURE
4. GALVANIZATION SHALL BE MIN 230g/Sqm
5. ROLLING SHUTTER SHALL WITHSTAND A BASIC WIND SPEED OF 50 m/s

REV.NO	REVISION	DATE	REVISED BY

CLEAR WIDTH (DW)	CLEAR HEIGHT (DH)	QTY
4000	3000	2 NOS

This drawing & designing is the property of NIHVA TECHNOLOGIES. Not to be sold or copied to any other concern.

TITLE :-
GEAR OPERATED ROLLING SHUTTER

NIHVA
NIHVA TECHNOLOGIES PVT. LTD.

	NAME	DATE
DRAWN	NIRMALA	20/07/2023
CHECK		
APPROVAL		

CLIENT - RKM Premier Constructions Pvt Ltd
PROJECT - Rolling shutter
SITE -Kanpur
DWG. NO. : NIHVA/23-24/CLT/0142 REV-00

If any queries contact : design1@nihva.com

SCALE: NTS | WT: | SHEET: 01 OF 01

ALL DIMENSION ARE IN mm