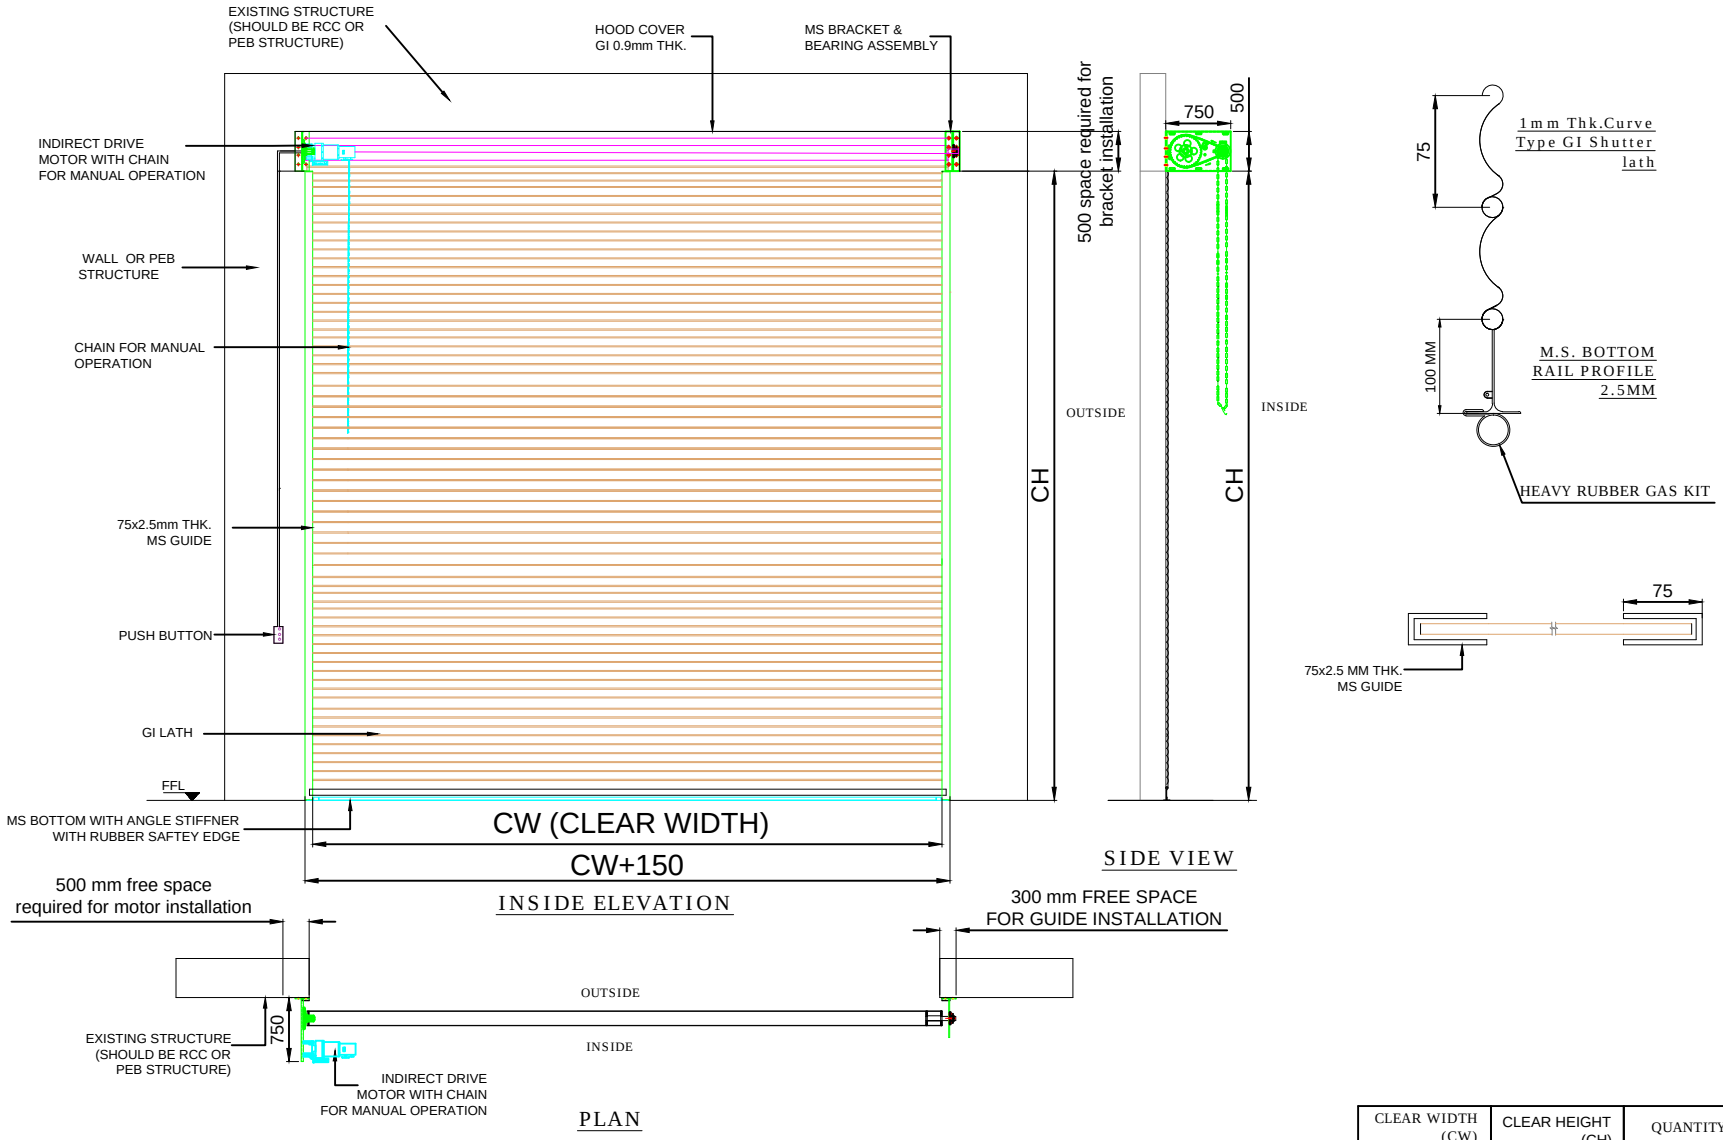


NOTE- PLEASE PROVIDE RAL COLOR SHADE FOR FINAL FINISH.

CLEAR WIDTH (CW)	CLEAR HEIGHT (CH)	QUANTITY
3100	3600	1

DIMENSION :

CLEAR WIDTH	CLEAR HEIGHT	QUANTITY
3100 mm	3600 mm	01 NOS.

NOTE:
1.REQUIRED STRUCTURE FOR SHUTTER SHALL BE IN CLIENT SCOPE.
2.ONE COAT OF RED OXIDE PRIMER WILL BE GIVEN TO NON GI COMPONENT OF SHUTTER
3.FOR FINAL FINISH CLIENT SHOULD MENTION RAL COLOR SHADE.
4. SINGLE PHASE SUPPLY SHOULD BE PROVIDED.

NIHVA TECHNOLOGIES PVT. LTD.
NIHVA TECHNOLOGIES PVT. LTD. PUNE
Email:- info@nihva.com
Website:- www.nihva.com

TITLE:

MOTORIZED ROLLING SHUTTER

CLIENT'S APPROVAL :

CLIENT - ITC

PROJECT -

SITE LOCATION - GUNTUR,A.P.

DWG. NO. : NIHVA/17-18/0003/R01

SCALE: NTS	WT:	SHEET:1 OF 1

DRAWN BY: OMKAR	DATE: 18-04-2017
CHECK : SAGAR P	DATE: 18-04-2017
APPROVED BY- R.K.	DATE: 18-04-2017

If any queries contact : projects@nihva.com

NOTE: ALL DIMENSIONS ARE IN mm

THIS DRAWING & DESIGN IS THE PROPERTY OF NIHVA TECHNOLOGIES. NOT TO BE SOLD OR COPY TO ANY OTHER CONCERN.