


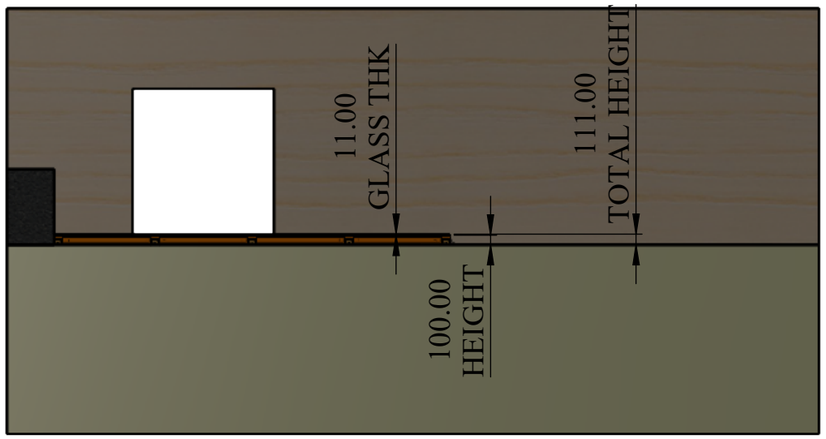


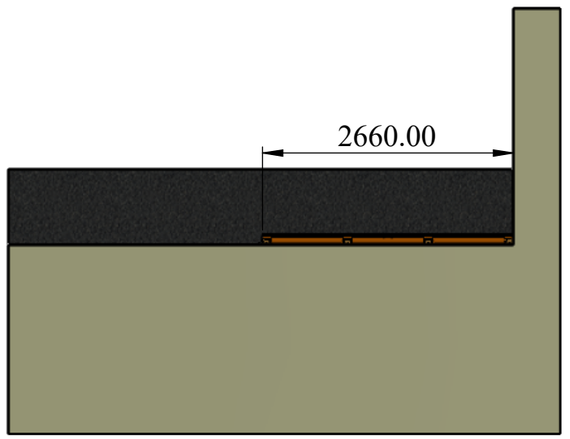


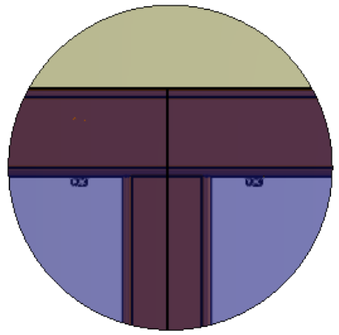

DETAIL B
SCALE 1 : 7


ANCHOR BOLTING TO
WALL FOR PANEL FITTING
TO THE WALL

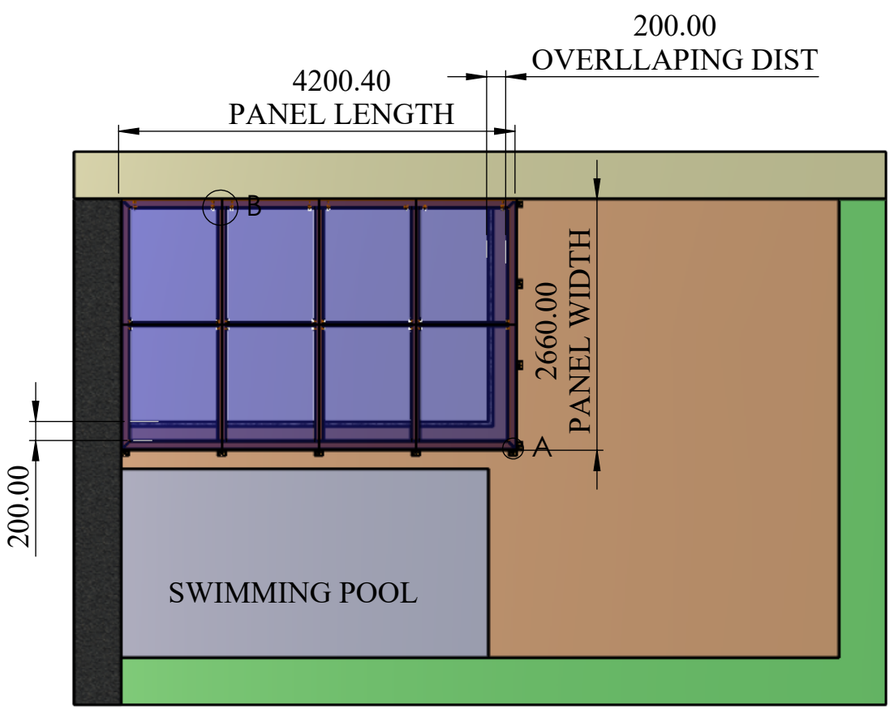

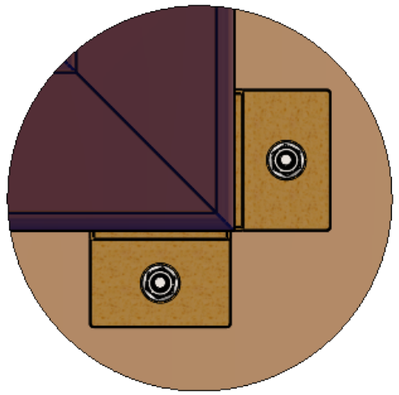


DETAIL A
SCALE 2 : 7


PALTE ARE WELD OUTSIDE
FOR PANEL FITTING CIVIL

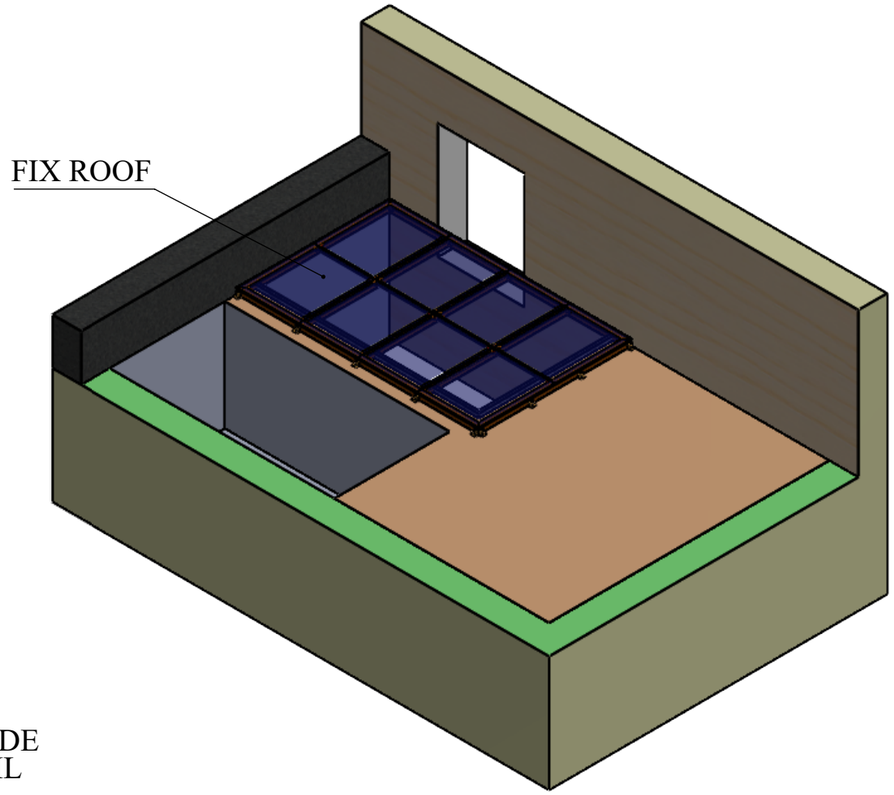


FIX ROOF GA DRAWING


TITLE - ROOF AUTOMATION				NIHVA TECHNOLOGIES PVT.LTD.PUNE Website - www.nihva.com
DWG NO - NTPL-000-PM-001-00-00-00				
	NAME	SIGNATURE	DATE	PROJECT NO - NTPL-000-PM
DRAWN	V.W		10-06-2025	PRODUCT - RETRACTABLE ROOF
CHK'D	S.W.		10-06-2025	SITE LOCATION - LUCKNOW
APPV'D	V.T.		10-06-2025	
if any queries contact - supportautomation@nihva.com				REVISION - 01 / QTY - 1
ALL DIMENSION ARE IN mm		A3		SCALE / SHEET 1 OF 2

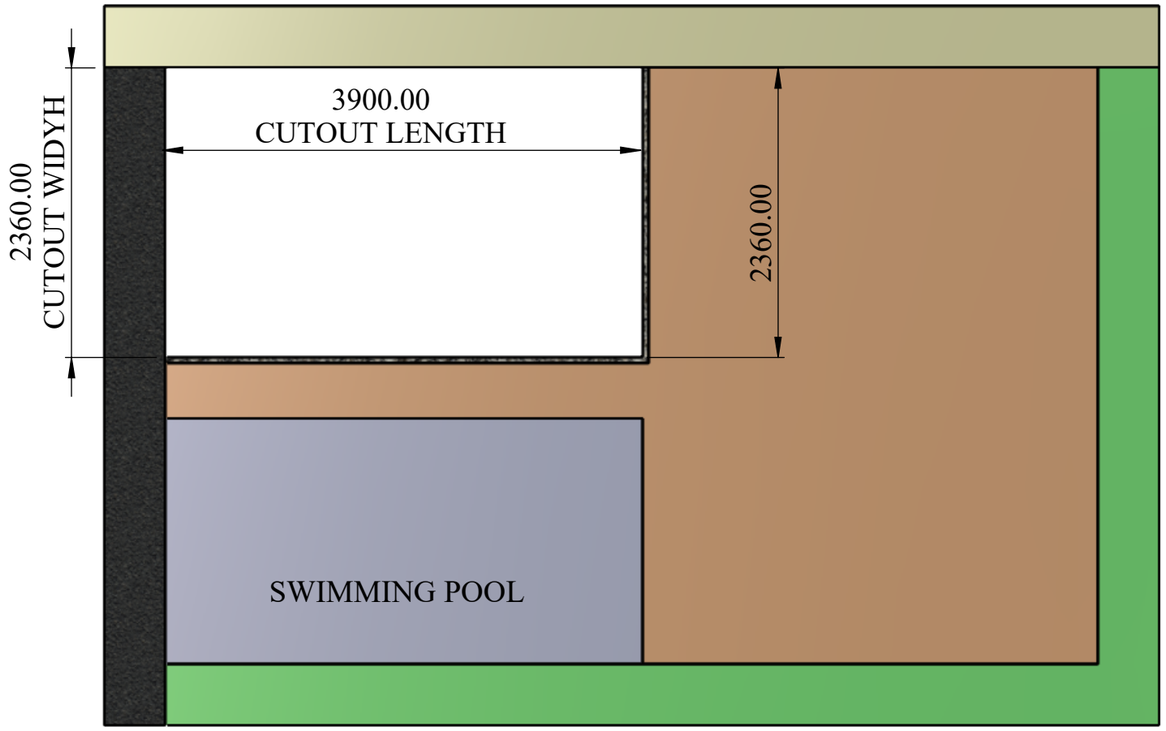

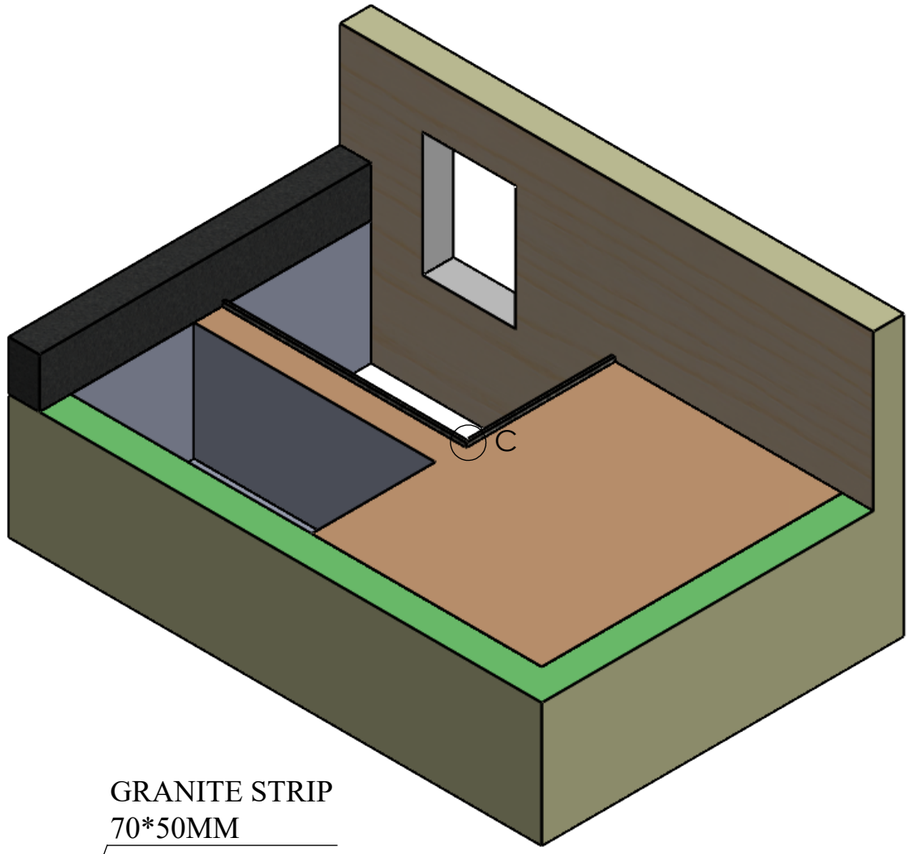

GRANITE STRIP
70*50MM

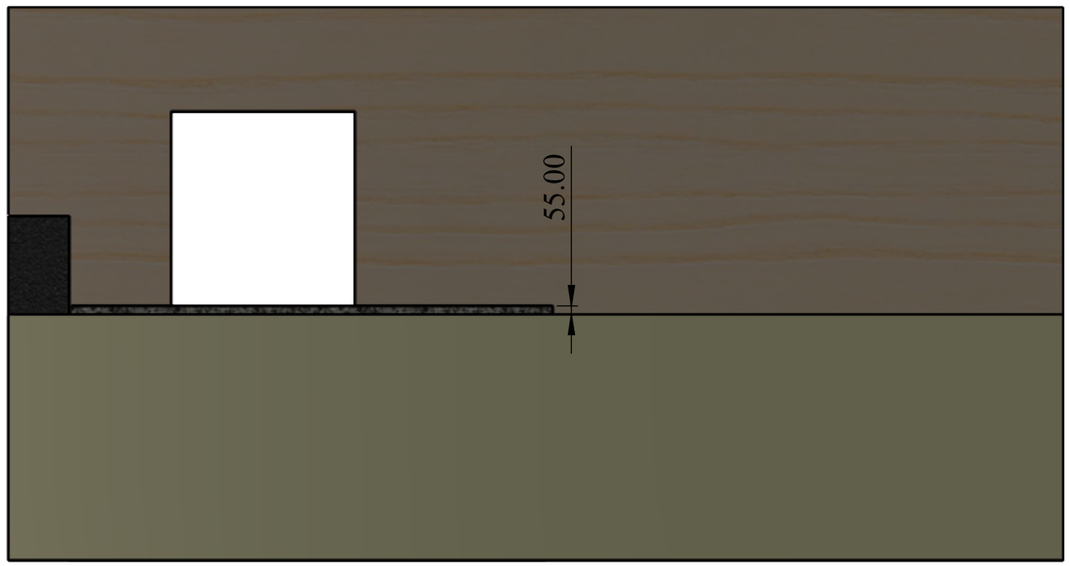

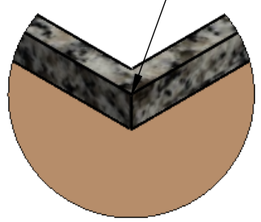

DETAIL C
SCALE 1 : 10

CIVIL DRAWING

NOTE :
TO AVOID WATER INSIDE THE ROOF
ADD GRANITE STRIP 70*50MM INSIDE,
AS PER SHOWN IN ABOVE SKECH

TITLE - ROOF AUTOMATION				NIHVA TECHNOLOGIES PVT.LTD.PUNE
DWG NO - NTPL-000-PM-001-00-00-00				Website - www.nihva.com
	NAME	SIGNATURE	DATE	PROJECT NO - NTPL-000-PM
DRAWN	V.W		10-06-2025	PRODUCT - RETRACTABLE ROOF
CHK'D	S.W.		10-06-2025	SITE LOCATION - LUCKNOW
APPV'D	V.T.		10-06-2025	
if any queries contact - supportautomation@nihva.com				REVISION - 01 / QTY - 1
ALL DIMENSION ARE IN mm		A3		SCALE / SHEET 2 OF 2