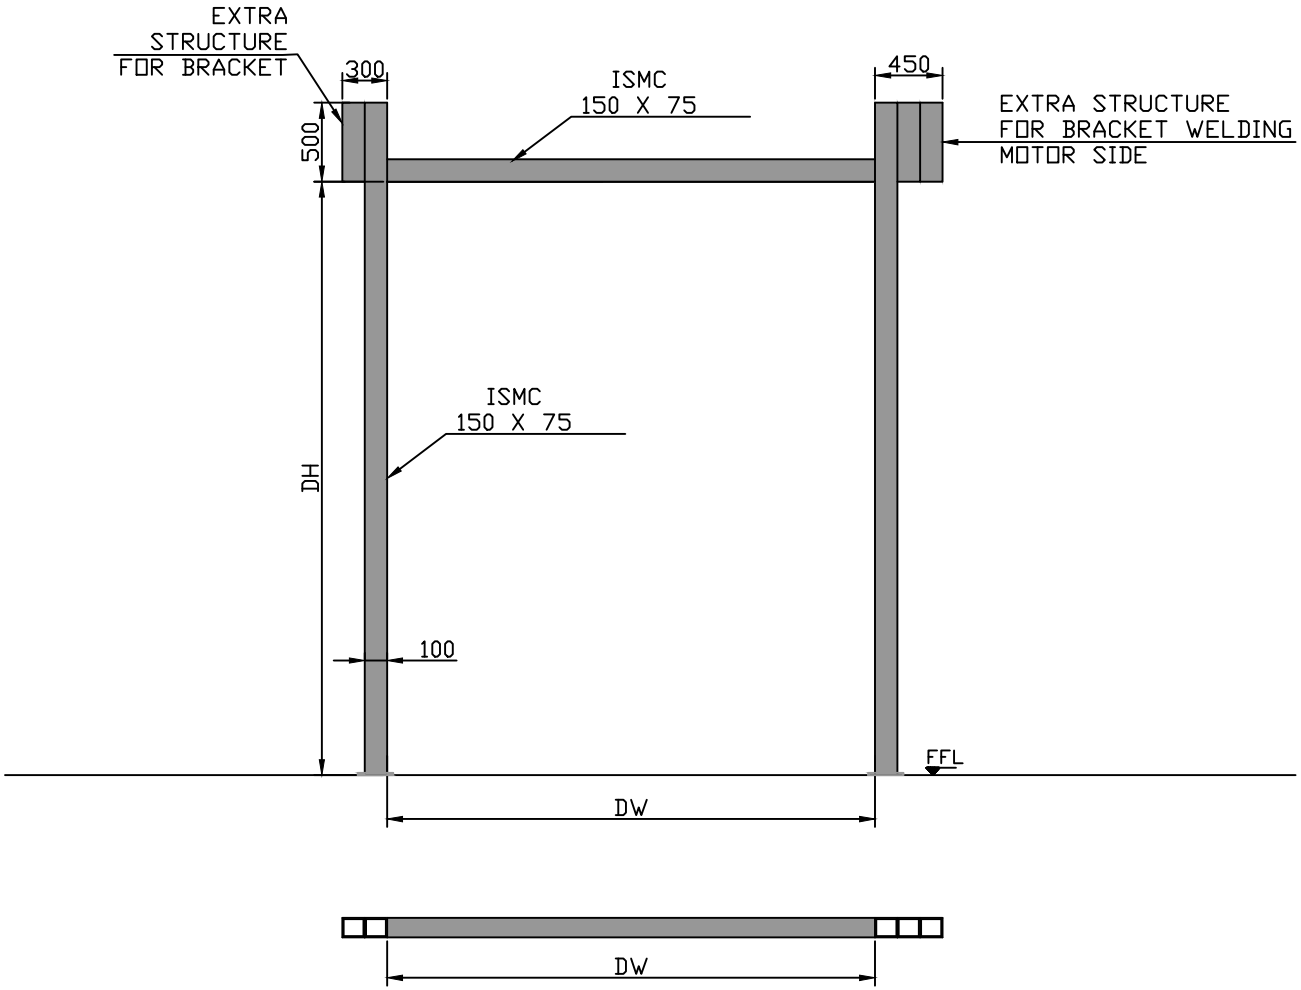


SR NO	DW	DH	LOCATION	QUANTITY
			DOOR DIMENSION	
2	3500	4000	Buffer Zone Shop Floor Side RS12	1 No
1	3200	3000	Pin Joint Loading Shop Floor Side Door(RS02 & RS03)	2 Nos

NOTE-
1. STRUCTURE REQUIRED FOR SHUTTER IS IN NIHVA SCOPE.
2. PAINT FINISH: EPOXY PAINTED OF APPROVED
   COLOR RAL CODE - RAL 7036 (PLATINIUM GREY)

This drawing & design is the property of NIHVA TECHNOLOGIES. Not to be sold or copied to any other concern.

TITLE - RR300 PLUS ALU HSD STRUCTURE

NIHVA TECHNOLOGIES PVT. LTD.
NIHVA TECHNOLOGIES PVT. PUNE
Tel : 020 66304033
Email:- info@nihva.com
Website:- www.nihva.com

	NAME	SIGN	DATE
DRAWN	P.V.A		25.06.19
CHECK	V.M.T		25.06.19
APPROVED			

CLIENT - LM WIND POWER BLADES
PROJECT -
SITE LOCATION - DABASPETH, BANGLORE.

Tolerance ±3 mm (for all dimensions)
Dimensions in [ ] ==> clearance for installation

If any queries contact:sales@nihva.com
ALL DIMENSION ARE IN mm

DWG. NO. -NIHVA/19-20/0054 REV- 0
SCALE: NTS WT: SHEET: