Prinzipzeichnung RapidProtect RP300
General drawing Rapid Protect RP300

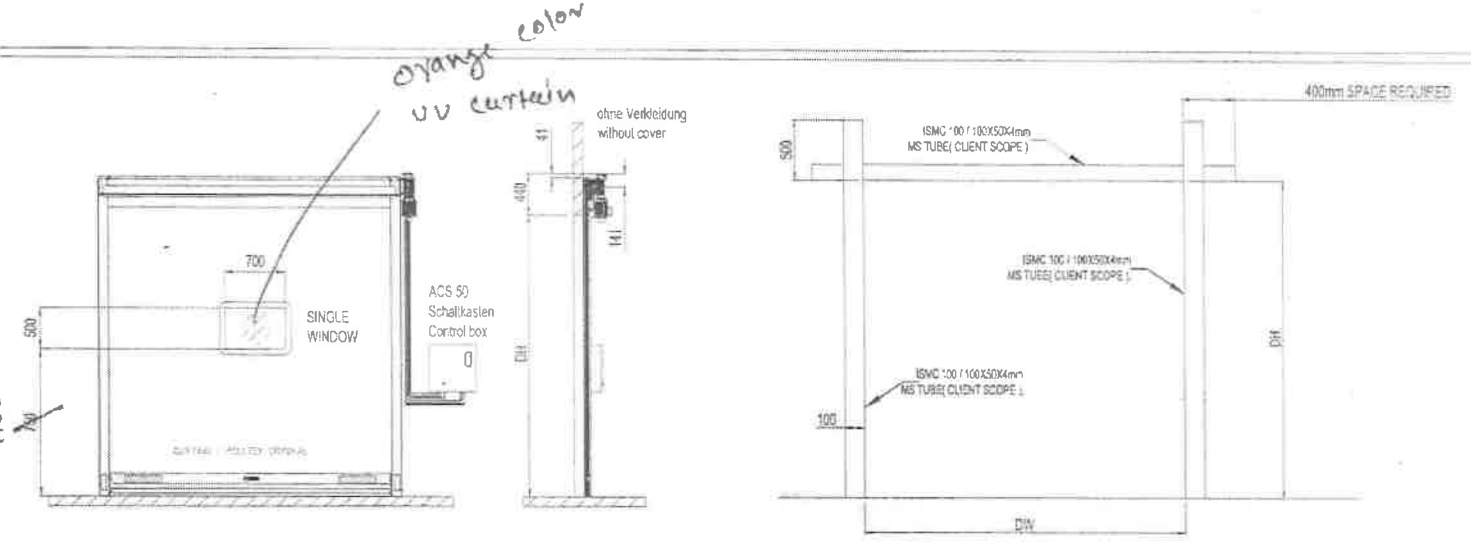

MS STRUCTURE

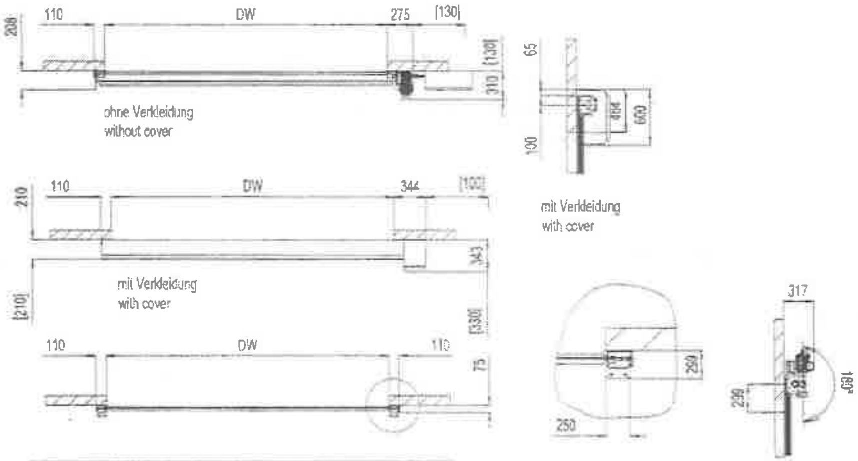

🟨	RAL 1003	
🟧	RAL 2004	
🟥	RAL 3000	
🟦	RAL 5002	
🟩	RAL 6005	
⬜	RAL 7035	
⬛	RAL 9005	
	RAL 9010	

ok →
Orange
vikas raut
23/10/18

DOOR SIZE		
DW	DH	QUANTITY
1500	~~2000~~ 2500	8

Toleranz ±3 mm (gültig für alle Maßangaben)
Tolerance ±3 mm (for all dimensions)

Maßangaben in [ ] ==> Montagefreiraum
Dimensions in [ ] ==> clearance for installation

NOTE-
1. COLOR : RAL 5002 (BLUE).
2. CURTAIN : ROLLTEX ORIGINAL.
3. REQUIRED STRUCTURE FOR HSD WILL BE IN CLIENT'S SCOPE.

REV.NO.	DESCRIPTION	DRAWN	DATE	SIGN
R0	1.WINDOW SIZE CHANGED 2.[illegible] RAL COLOUR	SURAJ	22-10-2018	

This drawing & designing is the property of NIHVA TECHNOLOGIES. [illegible]

TITLE	HIGH SPEED DOOR RP 300 & STRUCTURE			**NIHVA** NIHVA TECHNOLOGIES PVT. LTD. Website - www.nihva.com NIHVA TECHNOLOGIES PVT. LTD. PUNE Tel : 020 66304032 Email - info@nihva.com
	NAME	SIGN	DATE	
DRAWN	P.A		21.10.2018	CLIENT - FINEARC SYSTEMS LTD
CHECK	R.D		21.10.2018	PROJECT -
REV.	V.T		21.10.2018	SITE - PUNE
If any queries contact : design@nihva.com				DWG. NO. : NIHVA/18-19/D155/R01 REV:- 01
ALL DIMENSIONS ARE IN mm				SCALE: NTS SHEET: 01 OF 01