


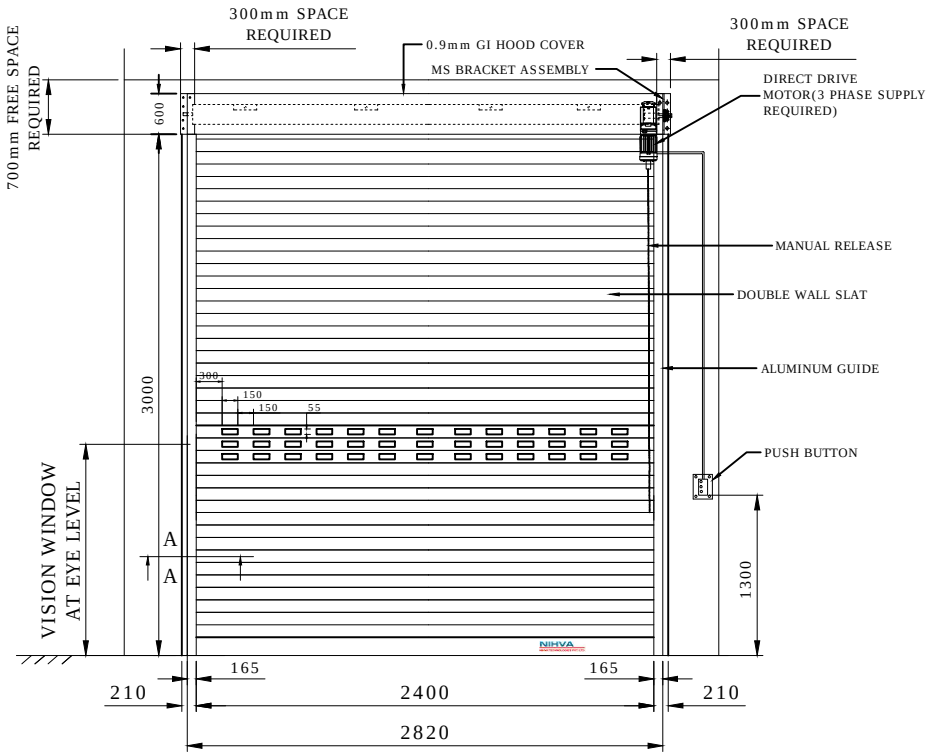


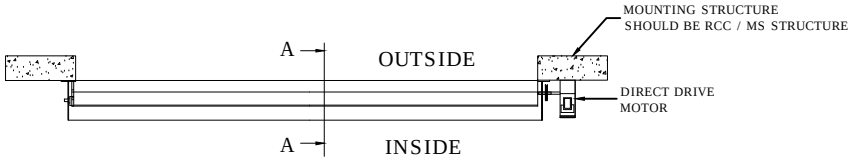

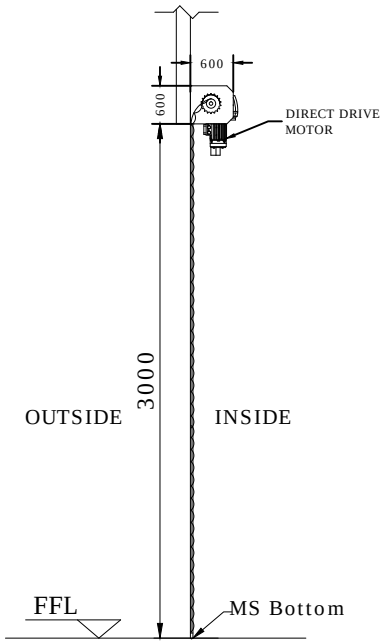

Section A-A


NOTE : ALL DOORS TO BE FIXED FROM INSIDE ONLY

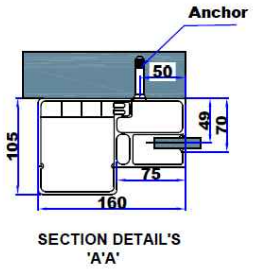

SECTION DETAIL'S 'A'A'

STANDARD COLOR OF SLATS & SHUTTER -RAL9002 (GRAY WHITE)

Main Slats
Double Wall Rolling Shutter

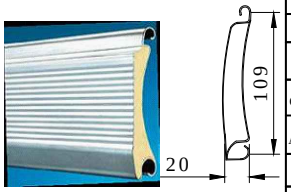

DIMENSION :

CLEAR WIDTH	CLEAR HEIGHT	QUANTITY
2400 mm	3000 mm	71 NOS

MATERIAL :

THICKNESS :

CLIENT SCOPE :-

1. STEEL STRUCTURE PROCUREMENT, FIXING & STRENGTH IS CLIENT RESPONSIBILITY.
2. 3 PHASE SUPPLY SHOULD BE PROVIDED.
3. 16A, 5 PIN INDUSTRIAL TYPE FEMALE SOCKET - 230V, 50Hz, WUTH EARTH AROUND 1/2 MTR FROM CONTROLLER/OPERATOR.
4. SOLID STATE INLINE (UPS/STABILIER) 2KVA CAPACITY REQUIRED.

NOTES :-

1. OPERATOR IS ALWAYS ON RIGHT SIDE.
2. CONTROLLER IS ALWAYS ON OPERATOR SIDE.

NIHVA TECHNOLOGIES PVT. LTD. PUNE
Email:- info@nihva.com
Website:- www.nihva.com

TITLE:

DOUBLE WALL ROLLING SHUTTER

CLIENT'S APPROVAL :

CLIENT - RELIANCE

PROJECT -

SITE LOCATION - NILAKOTTAI, TAMILNADU.

DWG. NO. : NIHVA/18-19/0280 | REV- 00

SCALE: NTS | WT: | SHEET:1 OF 1

DRAWN BY: P.V.A | DATE: 28.02.2019

CHECKED BY: V.M.T | DATE: 28.02.2019

APPROVED BY : | DATE:

If any queries contact : sales@nihva.com

NOTE: ALL DIMENSIONS ARE IN mm

THIS DRAWING & DESIGN IS THE PROPERTY OF NIHVA TECHNOLOGIES. NOT TO BE SOLD OR COPIED TO ANY OTHER CONCERN.