

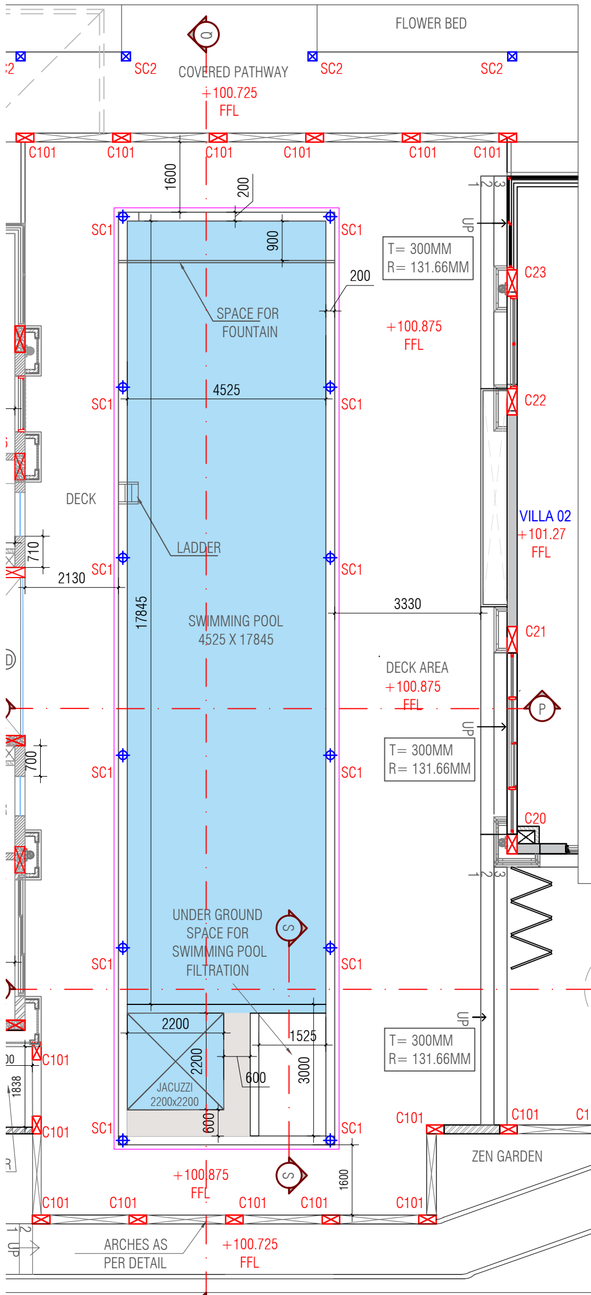



SWIMMING POOL AREA PLAN
SCALE 1:100

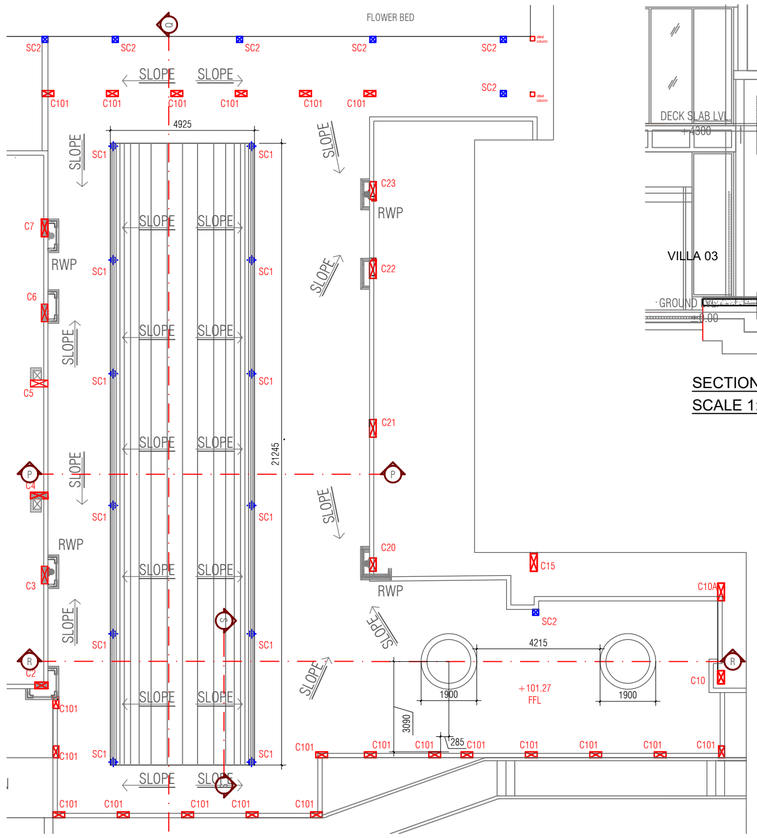


SWIMMING POOL AREA ROOF PLAN
SCALE 1:150

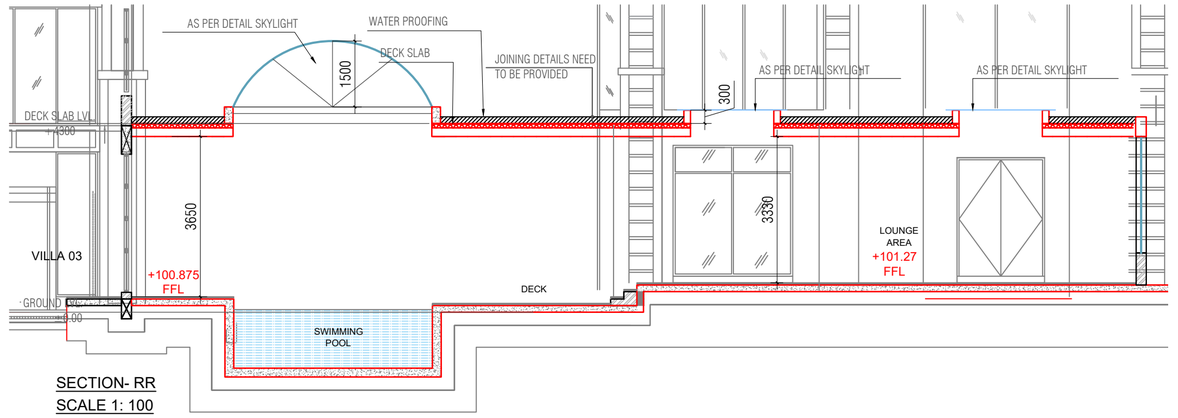

SECTION- RR
SCALE 1: 100

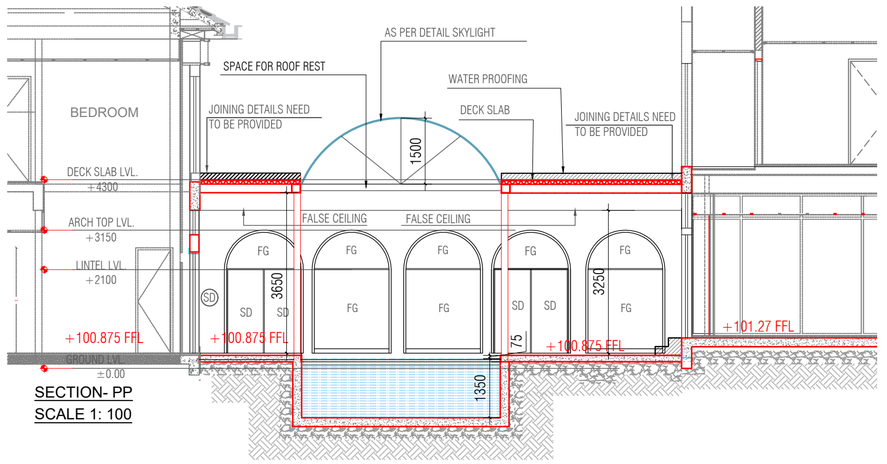

SECTION- PP
SCALE 1: 100

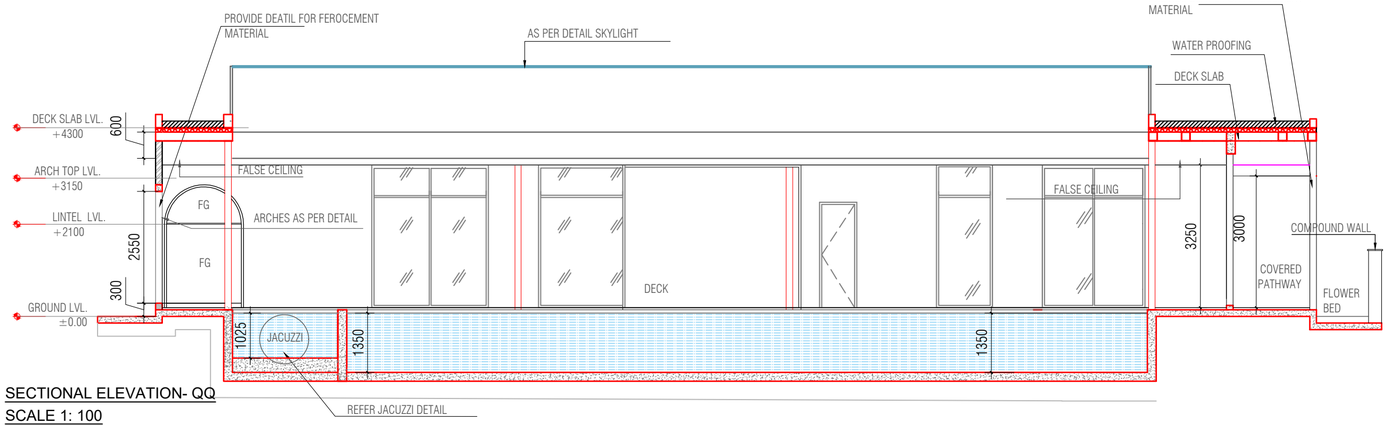

SECTIONAL ELEVATION- QQ
SCALE 1: 100

COPYRIGHT NOTE

THIS DRAWING IS SOLE PROPERTY OF DESIGN CONSULTANTS ARCHITECTS . THE COPYRIGHT OF THIS DRAWING SHALL REMAIN WITH US. THIS DRAWING MUST NOT WITHOUT OUR CONSENT BE SHOWN TO ANY PERSON OUTSIDE THE RECIPIENT, EMPLOYER OR BE COPIED OR ALTERED OR USED FOR THE PURPOSE OF CONSTRUCTION OR MANUFACTURING ANY ARTICLE SHOWN IN THIS DRAWING. THIS DRAWING ALONG WITH COPIES MADE BY THE RECIPIENT SHALL BE RETURNED ON DEMAND TO US.

NOTES

1. ALL DIMENSIONS ARE IN MM.
2. ONLY WRITTEN DIMENSIONS TO BE FOLLOWED.
3. DO NOT SCALE THE DRAWING.
4. IN CASE OF ANY AMBIGUITY OR DISCREPANCY, CONTACT THE ARCHITECTS.
5. REFER THIS DRAWING ALONG WITH THE STRUCTURAL ENGINEER'S DRAWINGS.
6. REFER STRUCTURAL ENGINEER'S DRAWINGS FOR REINFORCEMENT DETAILS.
7. CONSTRUCTION SHALL BE DONE ONLY AFTER THE APPROVAL FROM THE LOCAL AUTHORITY.

NORTH

ADVANCE COPY

ONLY AFTER GETTING THE APPROVAL FROM LOCAL AUTHORITY.
PLEASE NOTE: REFER SRTUCTURAL DRAWINGS FOR SKYLGHT AND SLAB DETAILS.

KEY PLAN

NO	REVISION	DATE
01	R0	31-01-2025

CLIENT	REVISION
MR.ROHIT PAWAR	R0
PROJECT	PROJECT NO
BUNGLOW EXTENSION	
SITE ADDRESS	
AMANORA, PUNE.	

SHEET TITLE:
SWIMMING POOL AREA DRAWINGS

SHEET NO	SCALE	DATE	DRAWN BY	CHECKED BY
AR-01-01, 03 AR-02-01,02	NTS	06.02.2025	MRUGENDRA	TRIPTI

ARCHITECTS SIGNATURE

ARCHITECT

Design Consultants Architects
SETU, UNIT NO.2, PLOT NO.69, BHARAT KUNJ, COLONY NO.2 ERANDAWANE, KOTHRUD,PUNE-38 ERANDAWANE, KOTHRUD,PUNE-38. TEL:020-25411470
FAX: 25422819 E-MAIL: do@dcapl.net