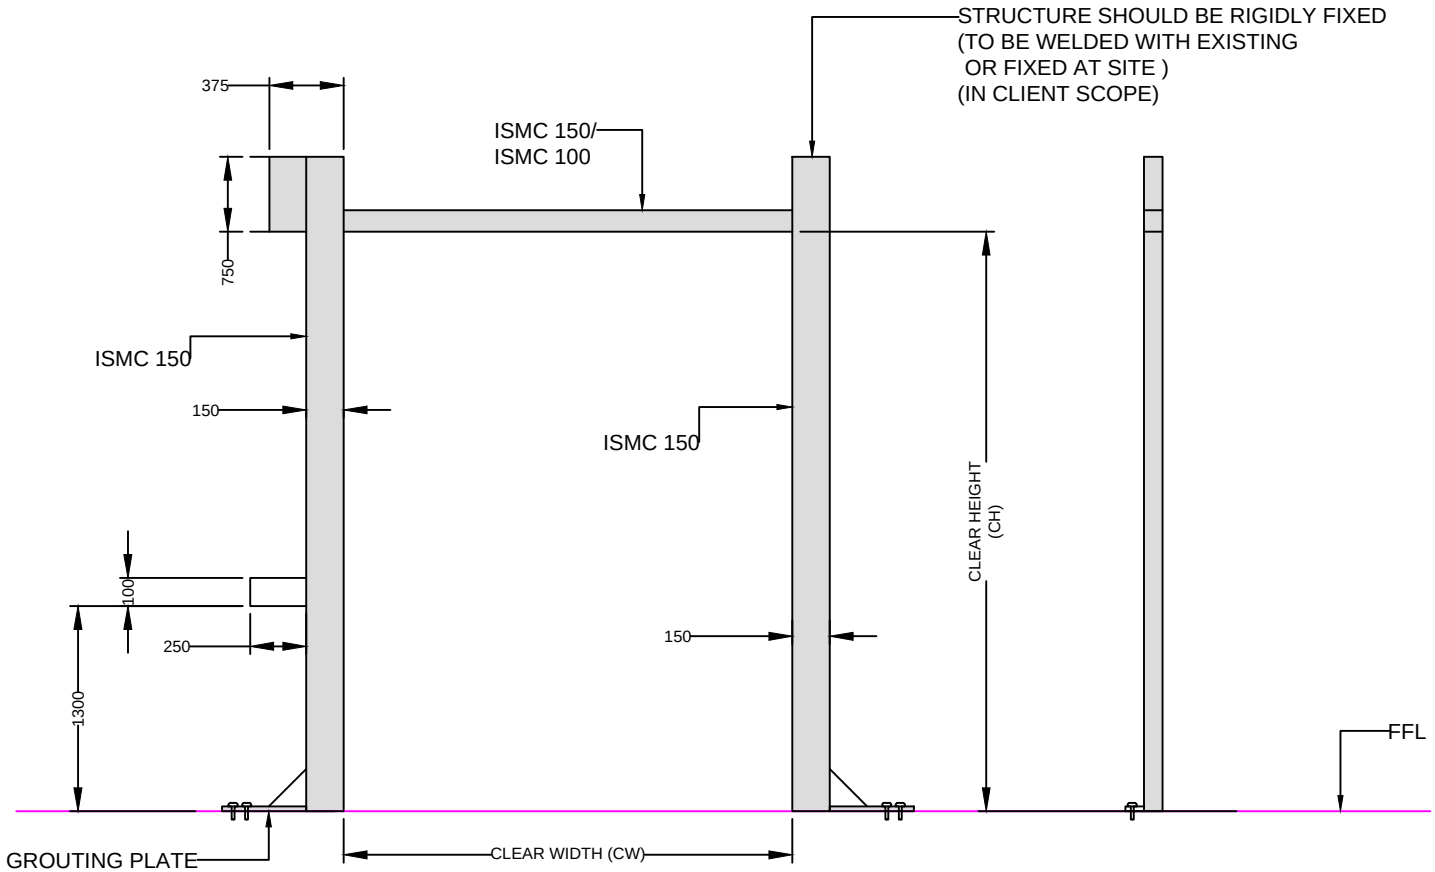

GROUTING PLATE = 250 X 150 X 12 MM THK

KINDLY NOTE THAT REQUIRED MS STRUCTURE ,
FITTING & ALL CIVIL WORK IN CLIENT SCOPE .

This drawing & design is the property of NIHVA TECHNOLOGIES. Not to be sold or copied to any other concern.

TITLE- HIGH SPEED DOOR
M.S. STRUCTURE

	NAME	SIGN	DATE
DRAWN	SIDDHESHWAR		3.12.2020
CHECK	K.P.		3.12.2020
APPRD.			

NIHVA TECHNOLOGIES PVT. LTD.
NIHVA TECHNOLOGIES PVT. LTD. PUNE
Tel : 020 66304033
Email:- info@nihva.com
Website:- www.nihva.com

CLIENT - CONGLOMERATE
PROJECT - CONGLOMERATE
SITE LOCATION - PUNE

If any queries contact : projectsupport@nihva.com
DWG. NO. : NIHVA/20-21/0100 REV- R00
ALL DIMENSION ARE IN mm
SCALE: NTS WT: SHEET: