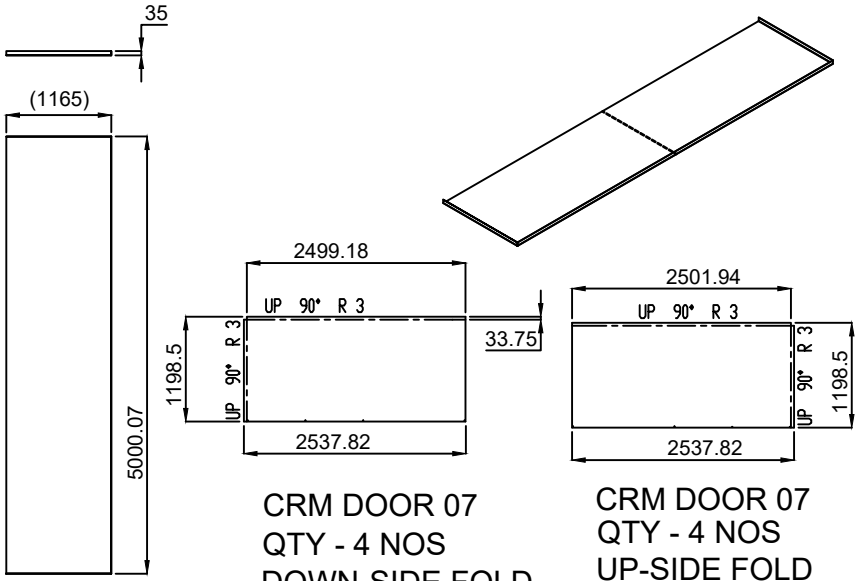
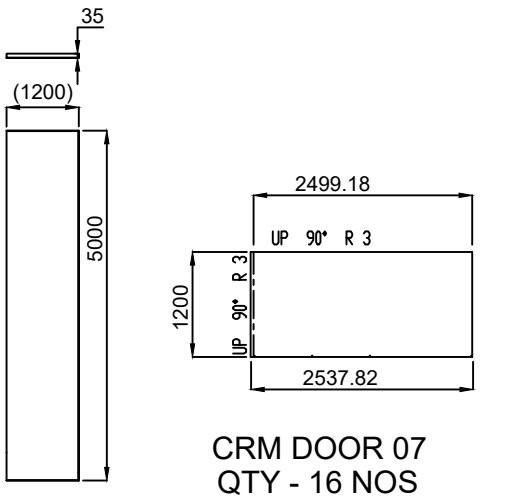
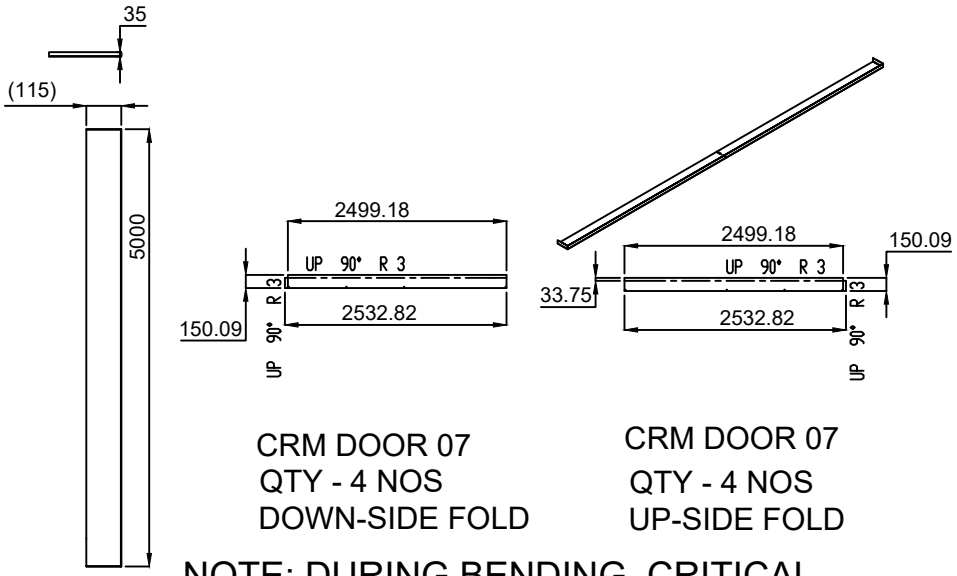



CRM DOOR 07
QTY - 4 NOS
DOWN-SIDE FOLD

CRM DOOR 07
QTY - 4 NOS
UP-SIDE FOLD



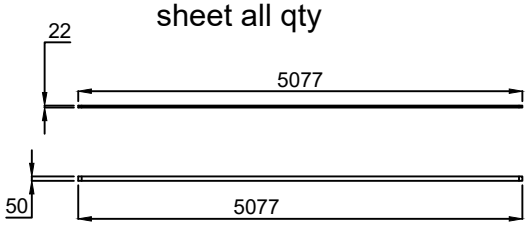

CRM DOOR 07
QTY - 16 NOS
DOWN-SIDE/UPSIDE
FOLD




CRM DOOR 07
QTY - 4 NOS
DOWN-SIDE FOLD

CRM DOOR 07
QTY - 4 NOS
UP-SIDE FOLD

CRM DOOR ALL
QTY - 16 NOS / each
sheet all qty




PPGI SHEET 1 MM

NOTE: DURING BENDING CRITICAL DIMENSION SHOULD BE MANDETORY

| REV. | REVISION DESCRIPTION | Date | Revised By |
|---|---|---|---|
| | | | |
| 000 | MODIFIED DUE TO RECIEVED COIL SIZE 1210 MM INSTEAD OF 1250 MM | 22/05/2022 | MAHESH S. |
| | | | |
| | | | |

This drawing & design is the property of NIHVA TECHNOLOGIES. Not to be sold or copied to any other concern.

TITLE:- 2 LEAF BOTH SIDE CRM DOOR 07

NIHVA TECHNOLOGIES PVT. LTD.

NIHVA TECHNOLOGIES PVT. LTD. PUNE
Tel : 020 66304033
Email:- info@nihva.com
Website:- www.nihva.com

| | NAME | DATE | SIGN |
|---|---|---|---|
| DRAWN | M.SUTAR | 22/05/2022 | |
| CHECK | M.SUTAR | 22/05/2022 | |
| APPRD. | | | |

CLIENT - NIHVA TECHNOLOGIES PVT.LTD
LOCATION -
PRODUCT - SLIDING DOOR - PPGI CLADDING

If any queries contact : design@nihva.com
DWG NO:-NIHVA/22-23/VDR/0015 REV- 0
ALL DIMENSION ARE IN mm
SCALE: NTS SCALE:-- 1:1 SHEET: 02 OF 02